




INSIDE ELEVATION

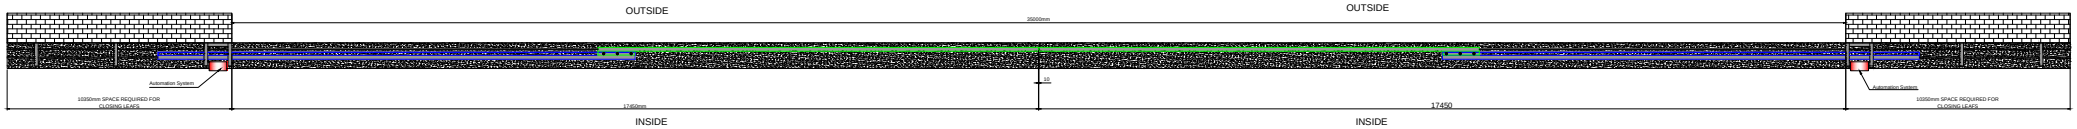


PLAN

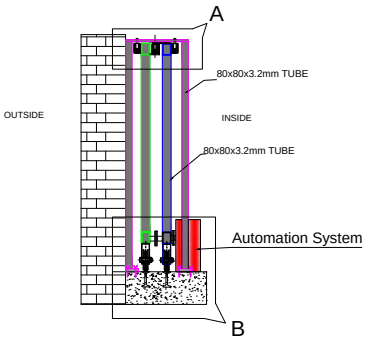

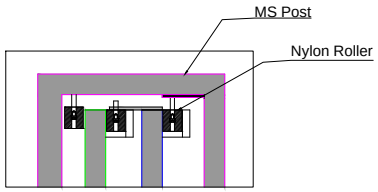

Detailed View of A

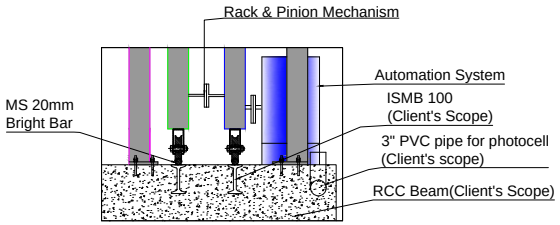

Detailed View of B

SR NO	TUBE SPECIFICATION	
1	80X80X3.2mm	OUTER TUBE
2	40X40X2mm	INTERMEDIATE TUBE
3	125mm	GAP BETWEEN TUBE
4	80X80X3.2mm	POST TUBE

04	RAL 7035	LIGHT GREY
03	RAL 5002	ULTRAMARINE BLUE
02	RAL 9002	GREY WHITE
01	RAL 1004	GOLDEN YELLOW
SR.NO	RAL CODE	RAL COLOR

CLEAR WIDTH	CLEAR HEIGHT	QUANTITY
35000mm	1800mm	1 NOS

NOTE-
1. ALL REQUIRED CIVIL WORK WILL BE IN CLIENTS SCOPE.
2. ONE COAT OF RED OXIDE & TWO COAT OF APPROVED RAL SHADE WILL BE GIVEN TO THE GATE.
3. IN NECESSARY GATE LEAF WILL BE IN TWO PARTS FOR TRANSPORTATION AND ILL BE WELDED TOGETHER ON SITE

This drawing & designing is the property of NIHVA TECHNOLOGIES. Not to be sold or copied to any other concern.

TITLE: Motorised telescopic Sliding gate 35m x 1.8m

NIHVA TECHNOLOGIES PVT. LTD. PUNE
Tel : 020 66304033
Email:- info@nihva.com
Website:- www.nihva.com

	NAME	SIGN	DATE
DRAWN	SURAJ		08/12/18
CHECK	PRADEEP		08/12/18
APPROVAL	R.D		08/12/18

CLIENT - INDAMER TECHNICS PVT. LTD.
PROJECT -
SITE LOCATION -
DWG. NO. : NIHVA/18-19/0196 Rev- 0
If any queries contact : design@nihva.com
SCALE: NTS WT: SHEET: 01 OF 01
ALL DIMENSION ARE IN mm