


SLIDING DIRECTION

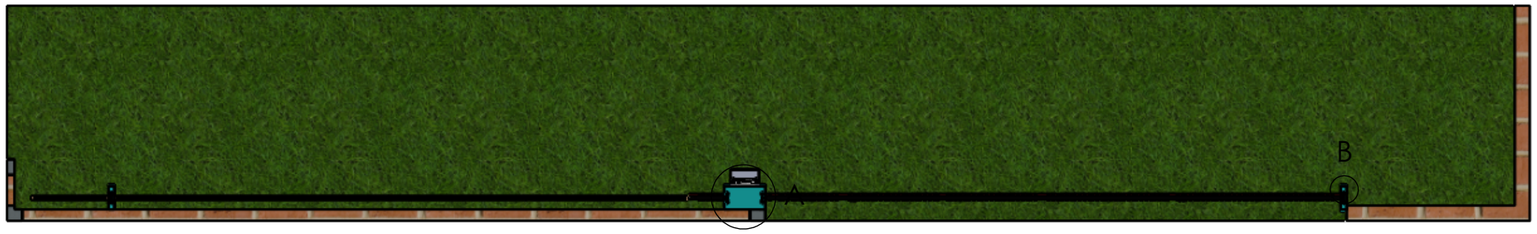


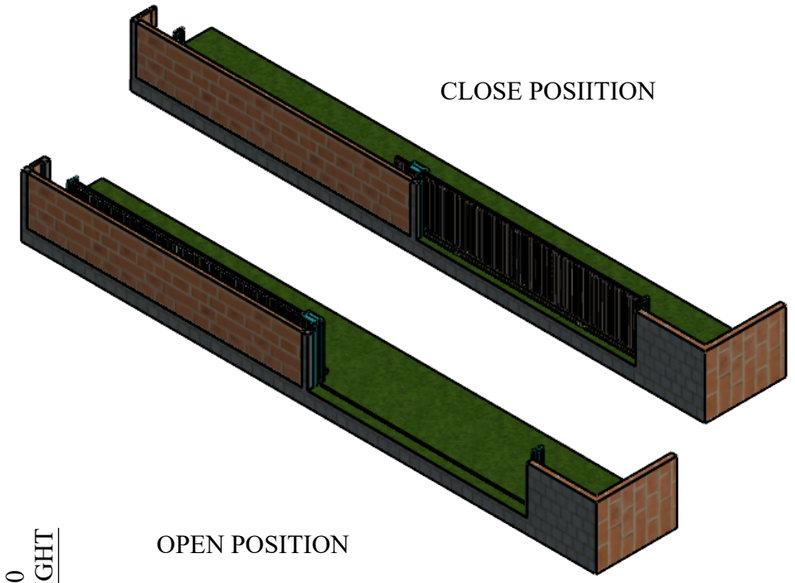


CLOSE POSIITION

OPEN POSITION

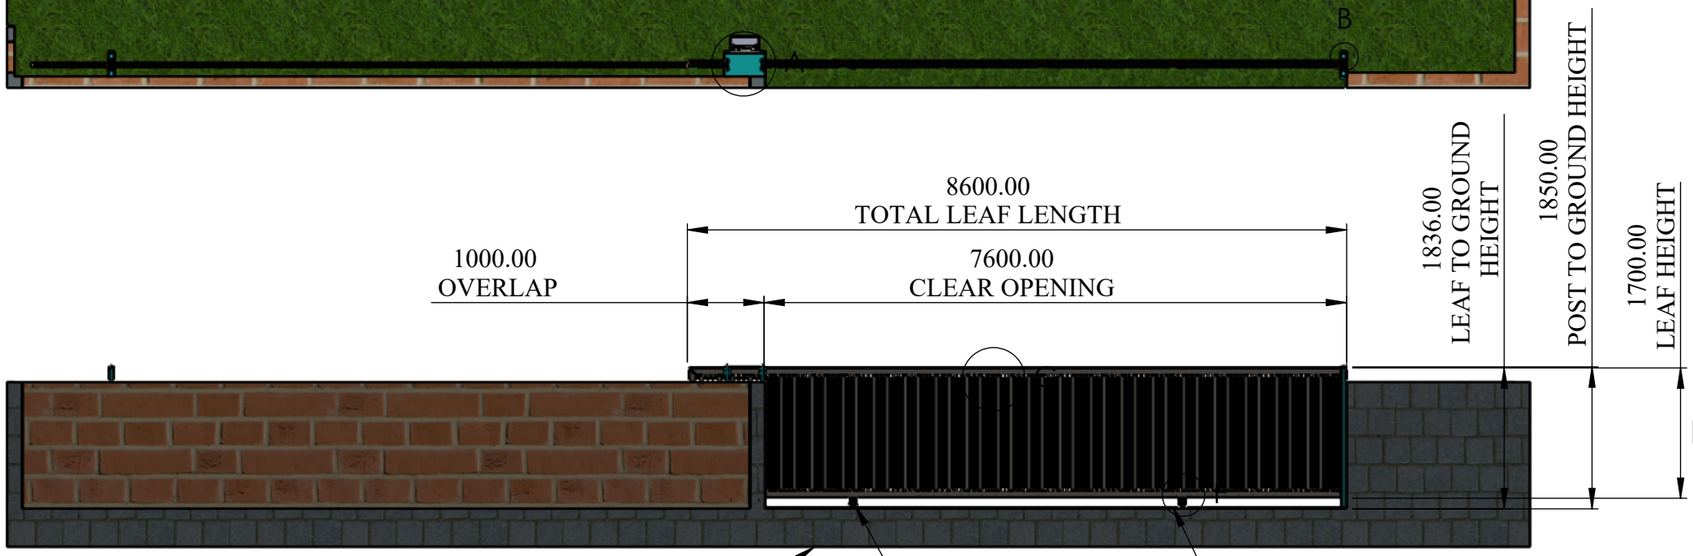

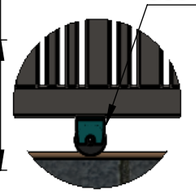


DETAIL F
SCALE 1 : 20

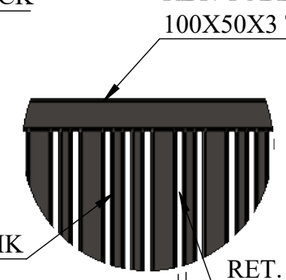


DETAIL G
SCALE 1 : 20

RACK AND PINION
LINEAR AND
ROTATORY MOVEMENT

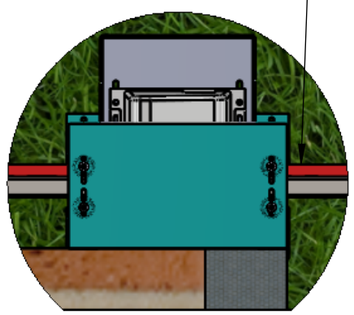


DETAIL A
SCALE 1 : 15

POST 1 NYLON
BEARING ASM

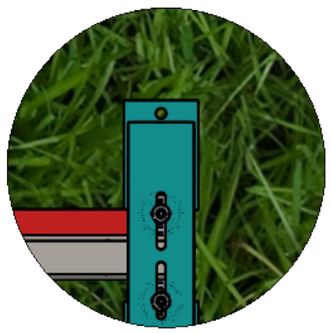

DETAIL B
SCALE 1 : 7


POST 2 NYLON
BEARING ASM

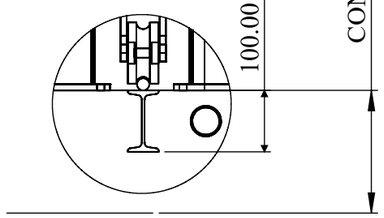


DETAIL E
SCALE 1 : 10


MOTORIZED SLIDING GATE
8600L X 1700 H (OVELAPPING +MOTOR MOUNTING DISTANCE CONSIDER)
PARKING AREA IS 8.6M

TITLE - GATE				NIHVA TECHNOLOGIES PVT.LTD.PUNE
DWG NO - NTPL			QTY - 1	Website - www.nihva.com
	NAME	SIGNATURE	DATE	PROJECT NO - NTPL
DRAWN	V.B.		09-05-25	PRODUCT - MOTORIZED SLIDING GATE
CHK'D	S.W.		09-05-25	SITE LOCATION - LUCKNOW
APPV'D	V.T.		09-05-25	
if any queries contact - supportautomation@nihva.com				REVISION -
ALL DIMENSION ARE IN mm			A3	SCALE -

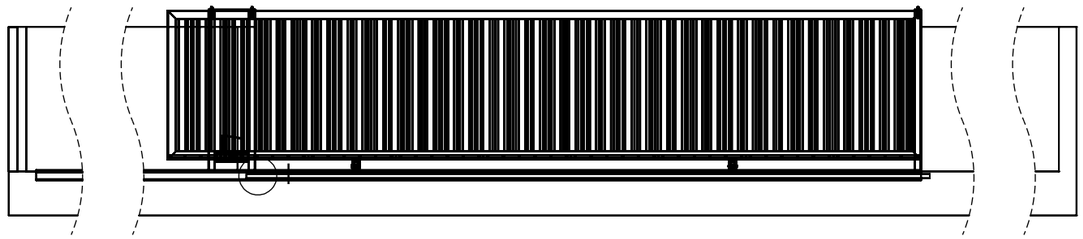

ITEM NO.	PART NUMBER	DESCRIPTION	QTY.
1	CIVIL AREA	AS PER CLIENT	1
2	GATE TRACK	(L) - 17200MM	1
9	SLIDING LEAF ASM	(L)-8600MM (H)-1700MM	1
4	POST 1 ASM 75X75	(L)-304MM (H)-1850MM	2
5	NYLON ROLLER AND BOLT ASM	(DIA)- 50MM (H)- 72MM	8
6	RACK ASM	STD	1
7	MOTOR	STD	1
8	POST 2 ASM 75X75	(L)-304 MM (H)-1850MM	1
9	NLYLON WHEEL	4 INCH	2
10	PVC PIPE	DIA- 50MM THK-3 7800MM LONG	1

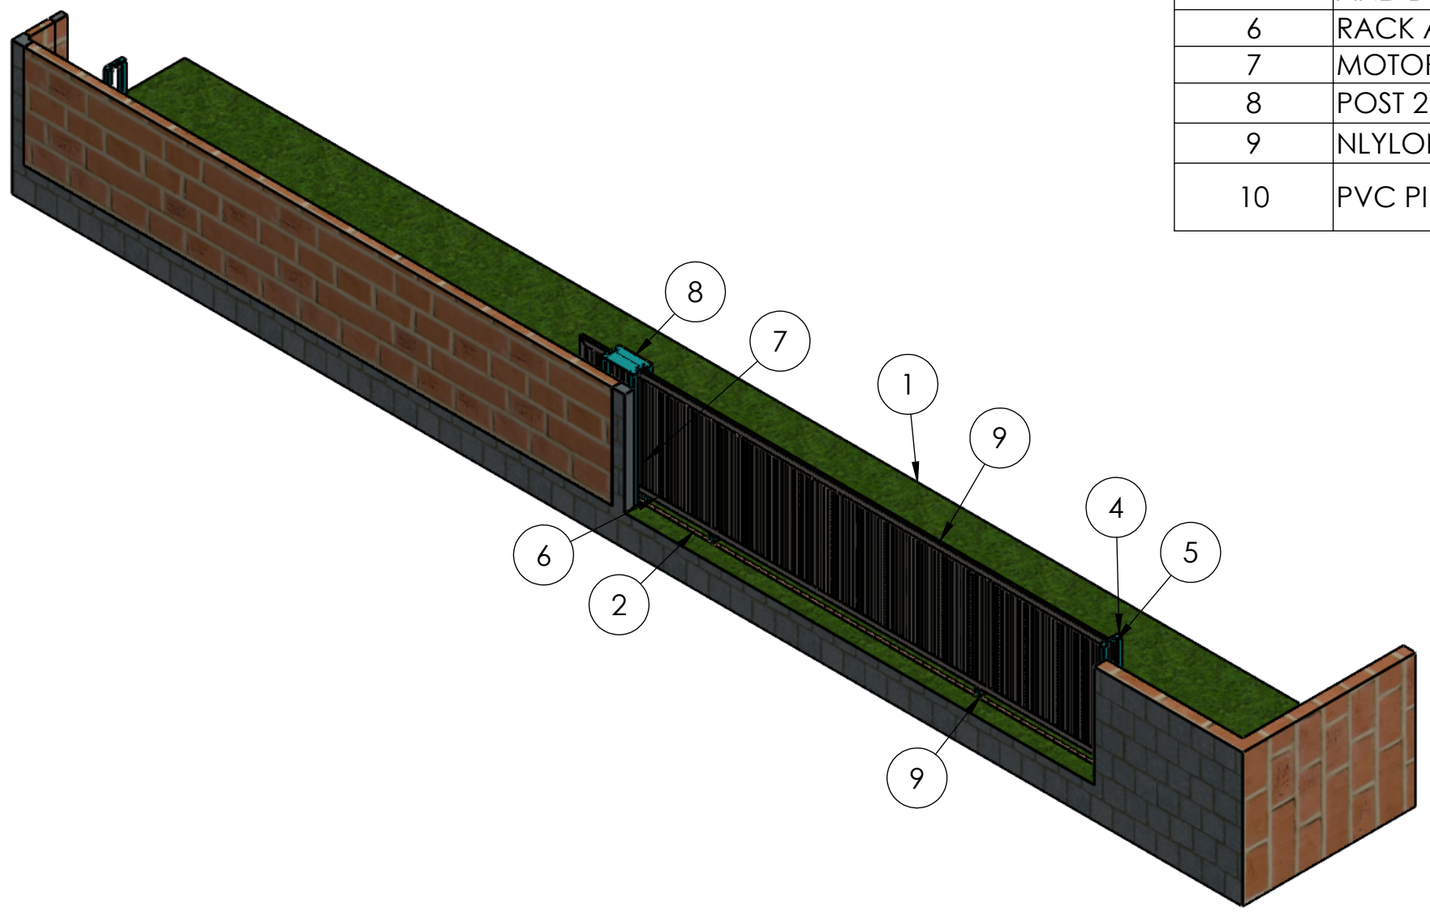


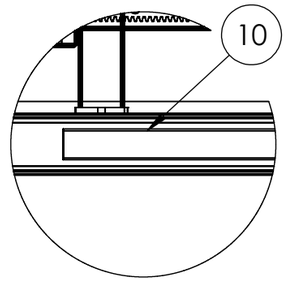

DETAIL I
SCALE 1 : 10

ISOMETRIC VIEW OF SLIDING GATE


TITLE - GATE AUTOMATION				NIHVA TECHNOLOGIES PVT.LTD.PUNE Website - www.nihva.com
DWG NO - NTPL			QTY - 1	
	NAME	SIGNATURE	DATE	PROJECT NO - NTPL
DRAWN	V.B.		05-06-25	PRODUCT - SLIDING GATE
CHK'D	S.W.		05-06-25	SITE LOCATION - LUCKNOW
APPV'D	V.T.		05-06-25	
if any queries contact - supportautomation@nihva.com				REVISION -
ALL DIMENSION ARE IN mm			A3	SCALE - SHEET 2 OF 21

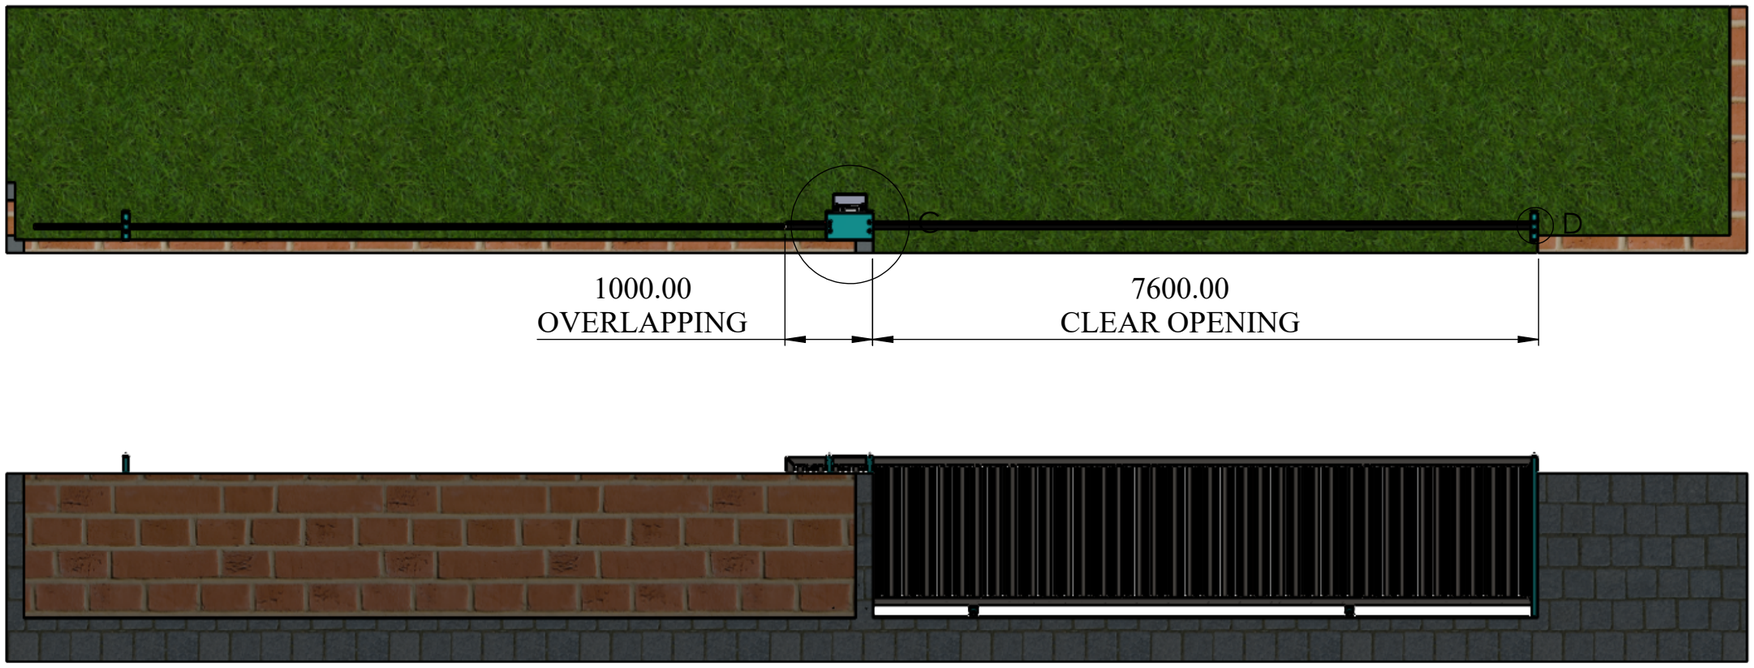



DETAIL D
SCALE 1 : 7

POST 1 NYLON
BEARING ASM

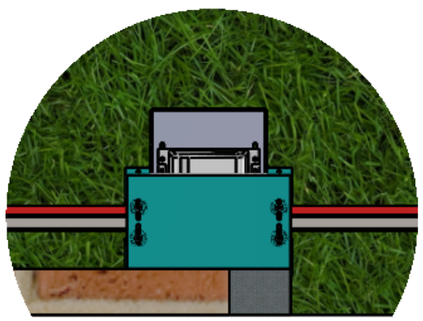



DETAIL C
SCALE 1 : 20


POST 2 NYLON
BEARING ASM

TITLE - GATE AUTOMATION				NIHVA TECHNOLOGIES PVT.LTD.PUNE Website - www.nihva.com
DWG NO - NTPL			QTY - 1	
	NAME	SIGNATURE	DATE	PROJECT NO - NTPL
DRAWN	V.B.		05-06-2025	PRODUCT - SLIDING GATE
CHK'D	S.W.		05-06-2025	SITE LOCATION - LUCKNOW
APPV'D	V.T.		05-06-2025	
if any queries contact - supportautomation@nihva.com				REVISION -
ALL DIMENSION ARE IN mm			A3	SCALE - SHEET 3 OF 21

ITEM NO.	PART NUMBER	DESCRIPTION	QTY.
1	SLIDING GATE	(L):- 8600 (H):- 1700	1
2	125 height wheel-WHEEL AND PLATE ASM	4 INCH WHEEL	2

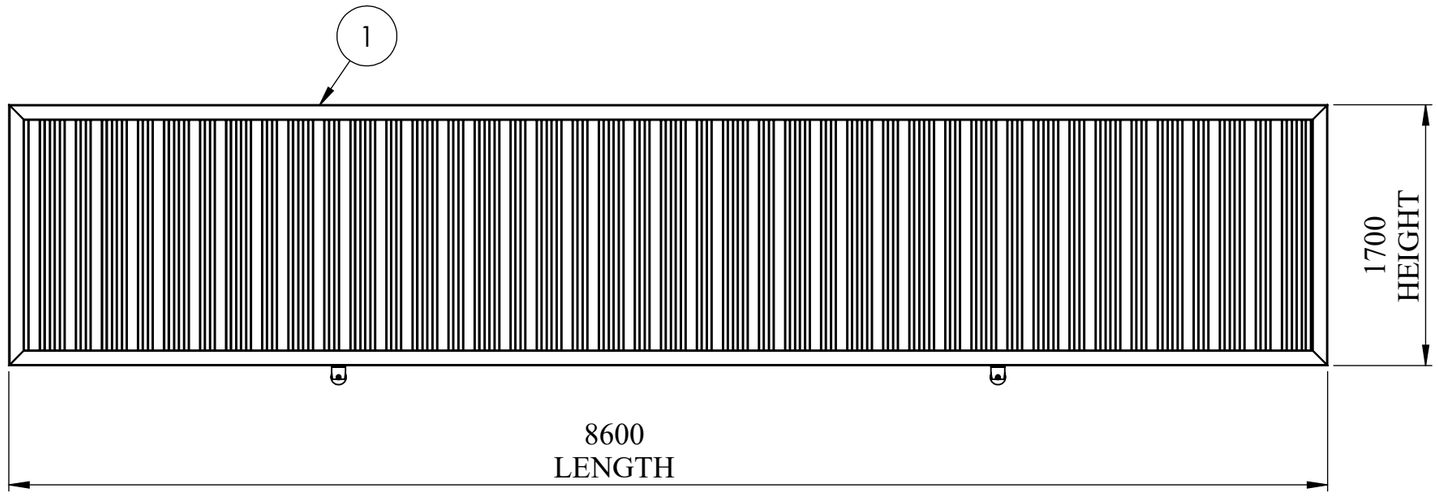

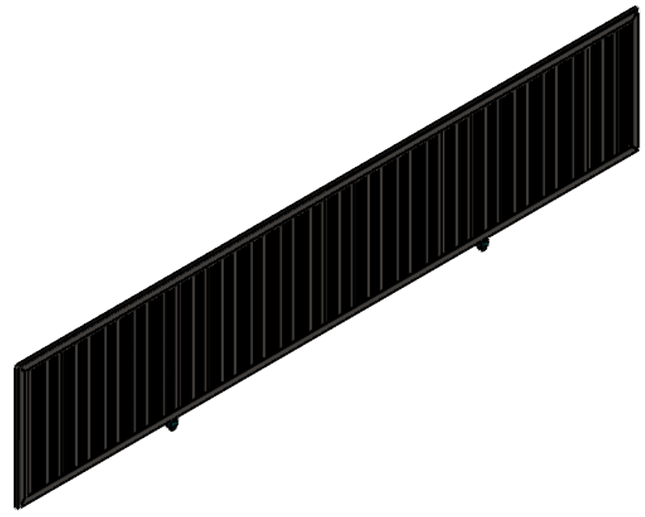


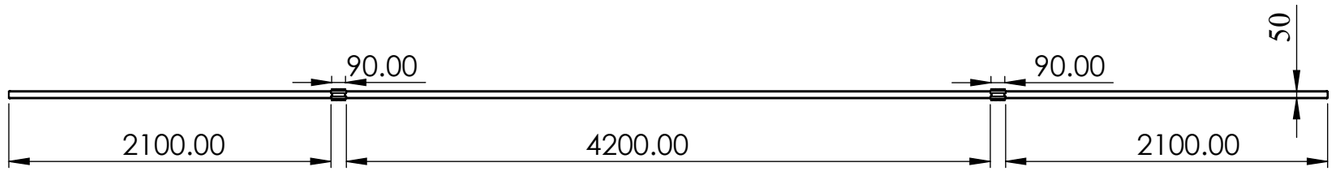


SLIDING LEAF:-1NOS


TITLE - GATE AUTOMATION				NIHVA TECHNOLOGIES PVT.LTD.PUNE
DWG NO - NTPL			QTY - 1	Website - www.nihva.com
	NAME	SIGNATURE	DATE	PROJECT NO - NTPL
DRAWN	V.B.		05-06-2025	PRODUCT - SLIDING GATE
CHK'D	S.W.		05-06-2025	SITE LOCATION - LUCKNOW
APPV'D	V.T.		05-06-2025	
if any queries contact - supportautomation@nihva.com				REVISION -
ALL DIMENSION ARE IN mm			A3	SCALE -

ITEM NO.	PART NUMBER	DESCRIPTION	QTY.
		TUBE, RECTANGULAR 50.00 X 100.00 X 3.00	4
		TUBE, RECTANGULAR 50.00 X 80.00 X 3.00	41
		TUBE, RECTANGULAR 50.00 X 40.00 X 3.00	63

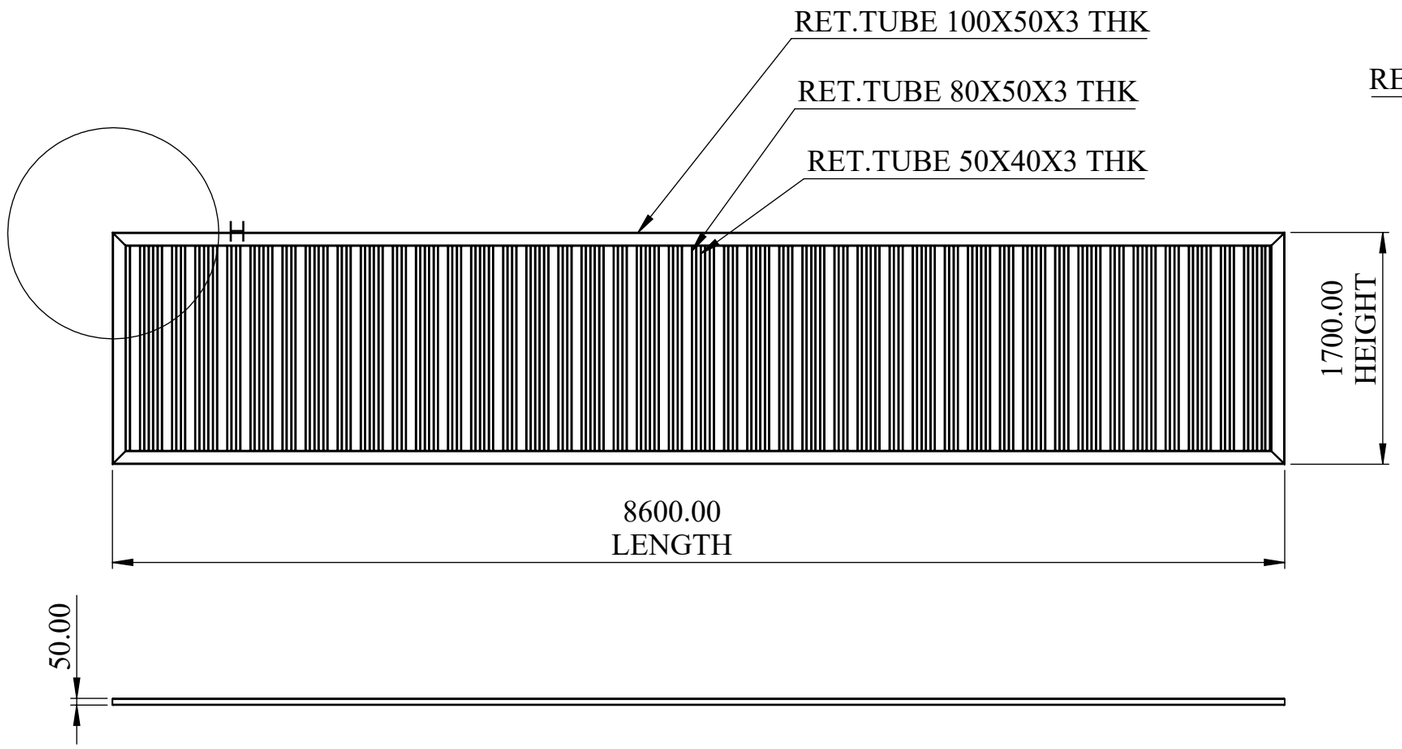

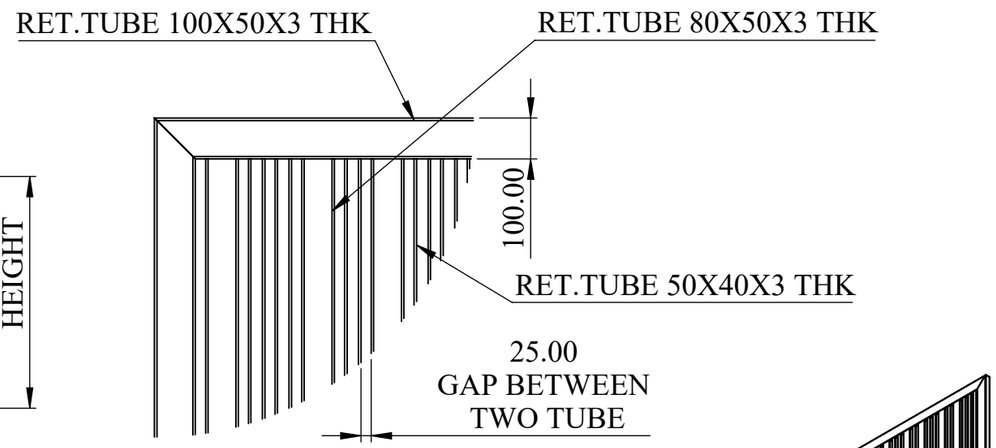


DETAIL H
SCALE 1 : 15

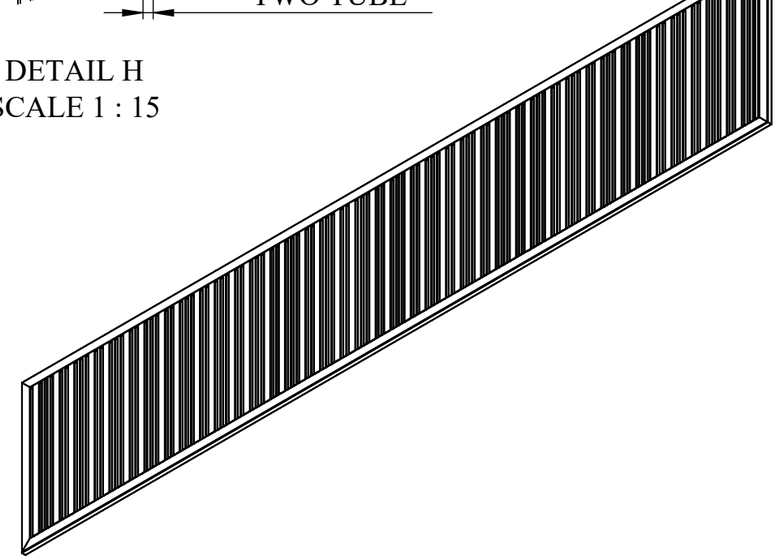



SUPPORT TUBE
QTY- 41 NOS (RET.TUBE 80X50X3 THK)
63 NOS (RET.TUBE 50X40X3 THK)

TITLE - GATE AUTOMATION				NIHVA TECHNOLOGIES PVT.LTD.PUNE
DWG NO - NTPL			QTY - 1	Website - www.nihva.com
	NAME	SIGNATURE	DATE	PROJECT NO - NTPL
DRAWN	V.B.		05-06-2025	PRODUCT - SLIDING GATE
CHK'D	S.W.		05-06-2025	SITE LOCATION - LUCKNOW
APPV'D	V.T.		05-06-2025	
if any queries contact - supportautomation@nihva.com				REVISION -
ALL DIMENSION ARE IN mm			A3	SCALE - SHEET 5 OF 21

ITEM NO.	PART NUMBER	DESCRIPTION	QTY.
1	GUIDE PLATE	ID-28 (H)-79 (W)-10	4
2	SUPPORT PLATE	(L)-90 (W)- 74	2
3	WHEEL	OD-100 (W)-50	2

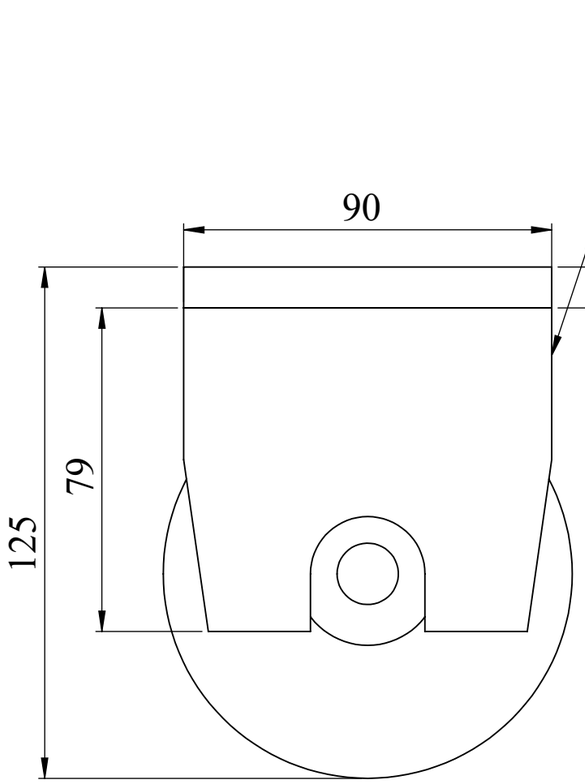

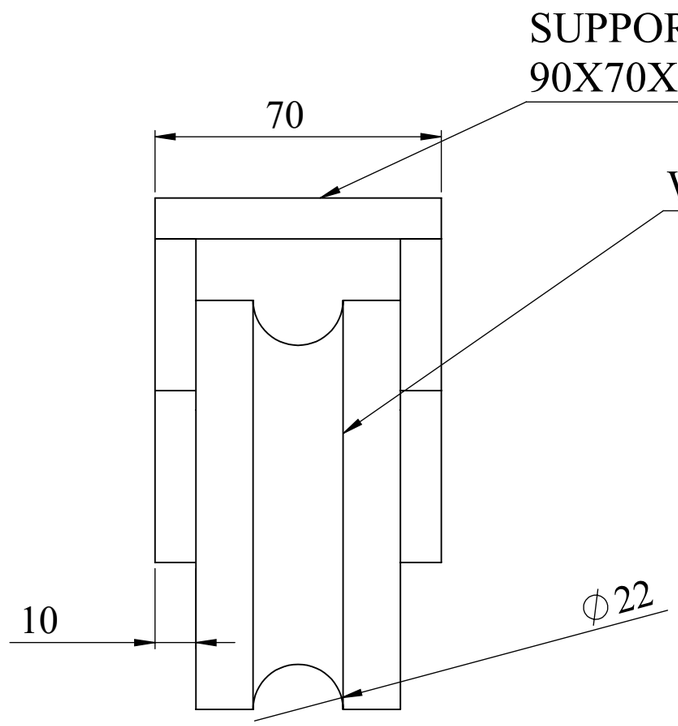


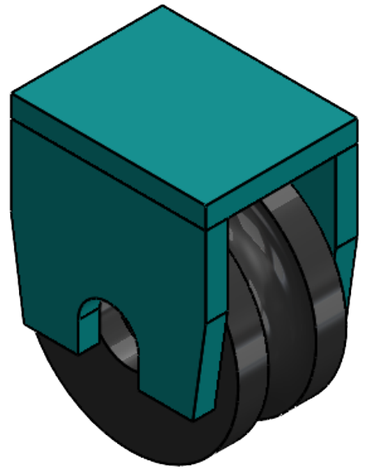


QTY- 2 NOS

TITLE - GATE AUTOMATION				NIHVA TECHNOLOGIES PVT.LTD.PUNE
DWG NO - NTPL			QTY - 1	Website - www.nihva.com
	NAME	SIGNATURE	DATE	PROJECT NO - NTPL268-PM- AD
DRAWN	V.B.		05-06-25	PRODUCT - SLIDING GATE
CHK'D	S.W.		05-06-25	SITE LOCATION -
APPV'D	V.T.		05-06-25	
if any queries contact - supportautomation@nihva.com				REVISION -
ALL DIMENSION ARE IN mm			A3	SCALE - SHEET 6 OF 21

ITEM NO.	PART NUMBER	DESCRIPTION	QTY.
1	SUPPORT PLATE	90x74x10	2

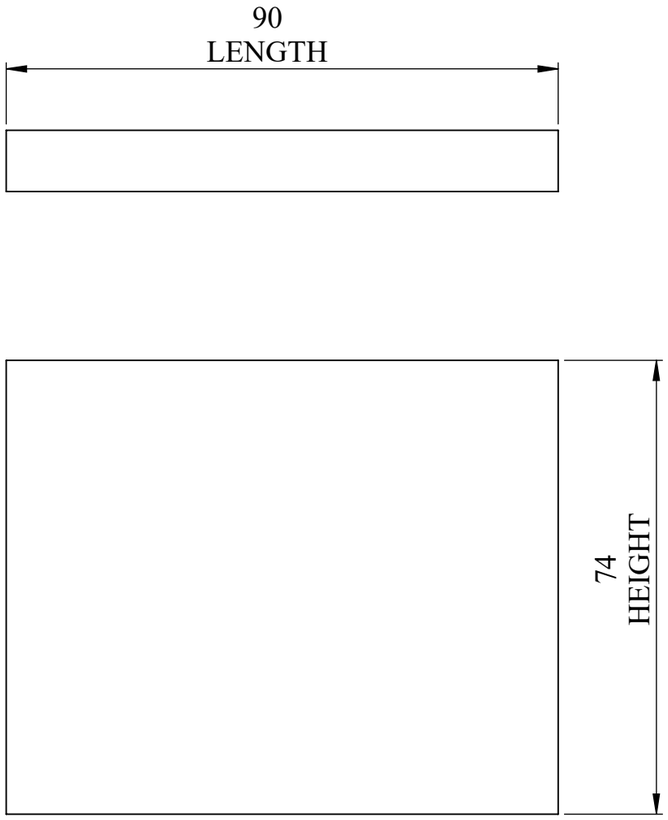


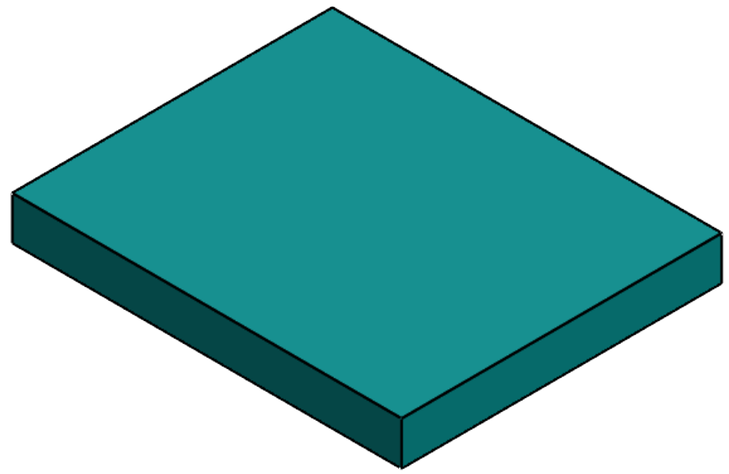



SUPPORT PLATE
QTY- 2NOS

TITLE - GATE AUTOMATION				NIHVA TECHNOLOGIES PVT.LTD.PUNE Website - www.nihva.com
DWG NO - NTPL268-PM			QTY - 1	
	NAME	SIGNATURE	DATE	PROJECT NO - NTPL268-PM- AD
DRAWN	V.B.		05-06-2025	PRODUCT - SLIDING GATE
CHK'D	S.W.		05-06-2025	SITE LOCATION -LUCKNOW
APPV'D	V.T.		05-06-2025	
if any queries contact - supportautomation@nihva.com				REVISION -
ALL DIMENSION ARE IN mm			A3	SCALE -

ITEM NO.	PART NUMBER	DESCRIPTION	QTY.
1	GUIDE PLATE	ID-28 (H)-79 (W)-10	4

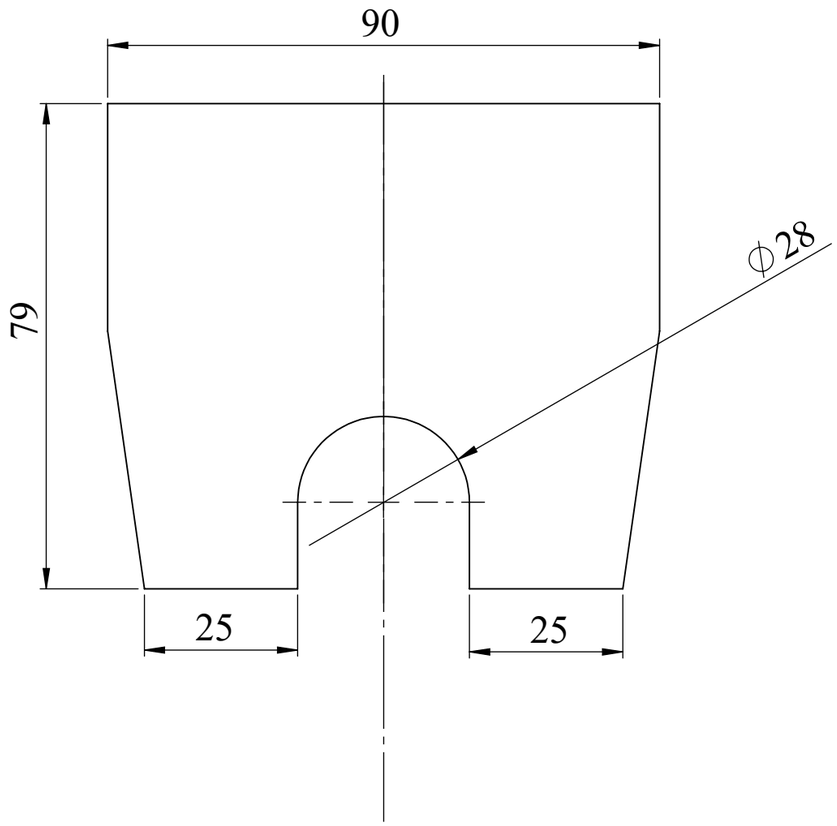

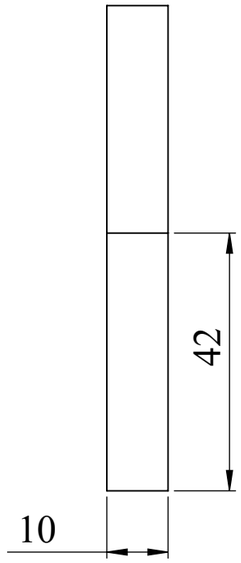


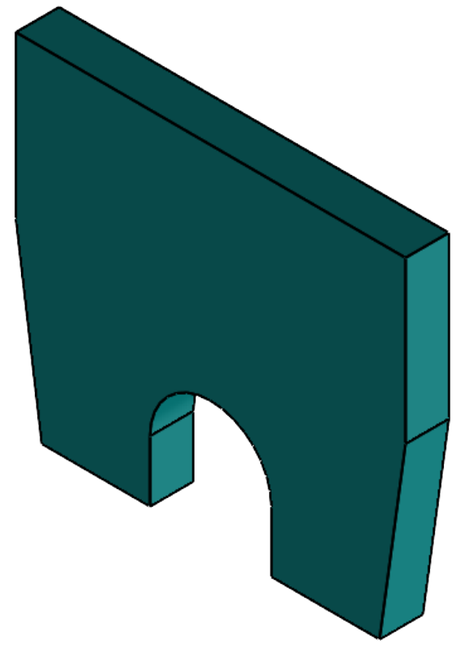


GUIDE PLATE
QTY- 4 NOS

TITLE - GATE AUTOMATION				NIHVA TECHNOLOGIES PVT.LTD.PUNE
DWG NO - NTPL			QTY - 1	Website - www.nihva.com
	NAME	SIGNATURE	DATE	PROJECT NO - NTPL268-PM- AD
DRAWN	V.B.		05-06-2025	PRODUCT - SLIDING GATE
CHK'D	S.W.		05-06-2025	SITE LOCATION -LUCKNOW
APPV'D	V.T.		05-06-2025	
if any queries contact - supportautomation@nihva.com				REVISION -
ALL DIMENSION ARE IN mm			A3	SCALE - SHEET 8 OF 21

ITEM NO.	PART NUMBER	DESCRIPTION	QTY.
1	WHEEL	OD-100 (W)-50	2

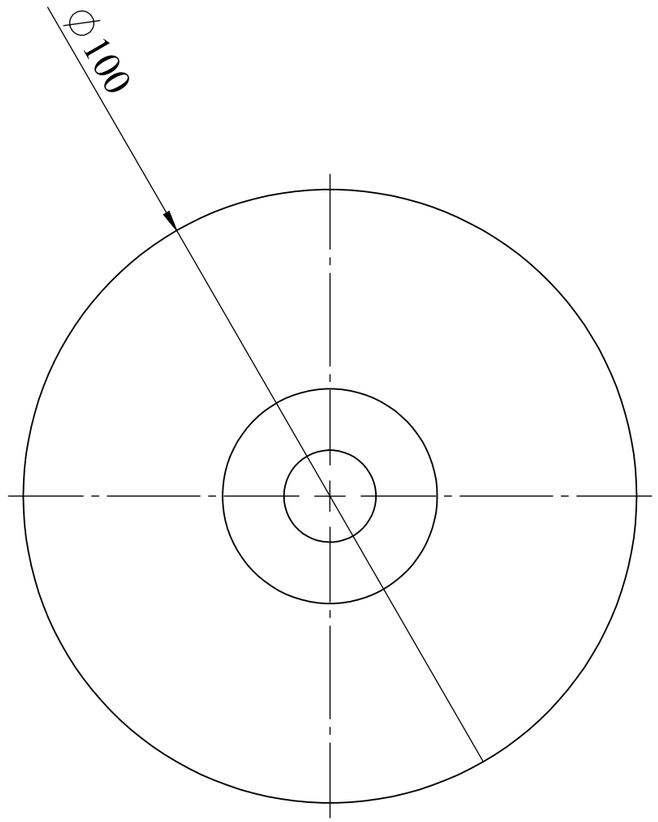

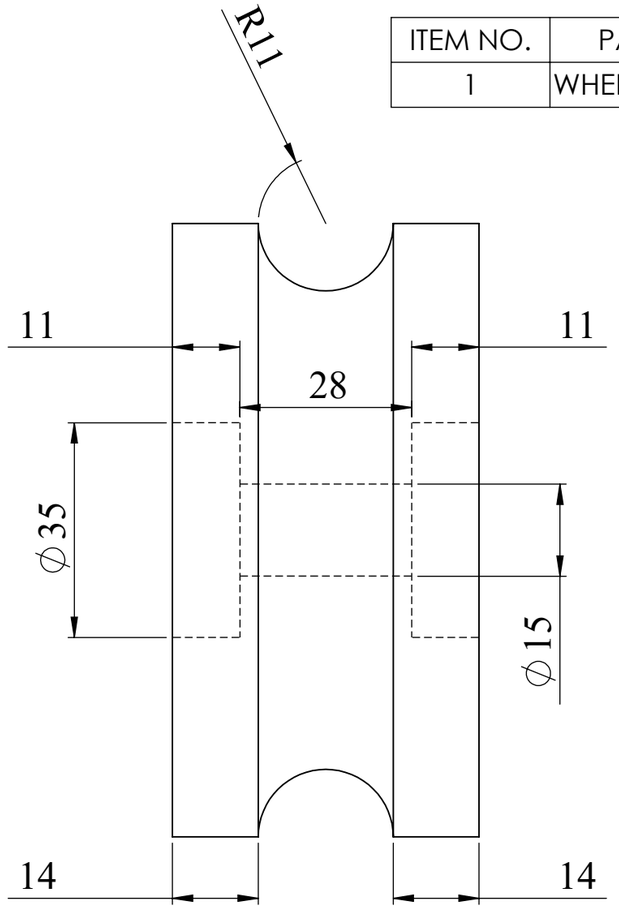






WHEEL
QTY- 2 NOS

TITLE - GATE AUTOMATION				NIHVA TECHNOLOGIES PVT.LTD.PUNE Website - www.nihva.com
DWG NO - NTPL			QTY - 1	
	NAME	SIGNATURE	DATE	PROJECT NO - NTPL
DRAWN	V.B.		05-06-2025	PRODUCT - SLIDING GATE
CHK'D	S.W.		05-06-2025	SITE LOCATION -
APPV'D	V.T.		05-06-2025	
if any queries contact - supportautomation@nihva.com				REVISION -
ALL DIMENSION ARE IN mm			A3	SCALE -

ITEM NO.	PART NUMBER	DESCRIPTION	QTY.
1	nylon roller asm	STD	8

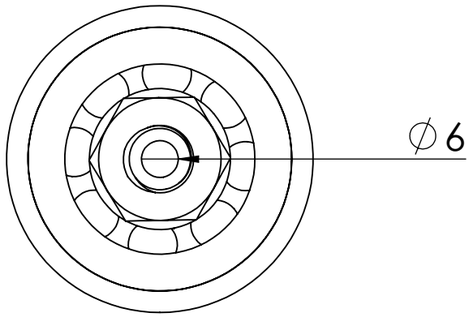

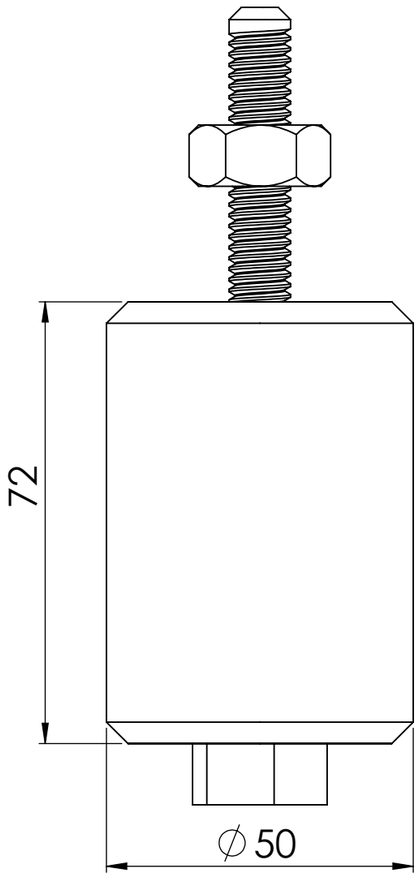

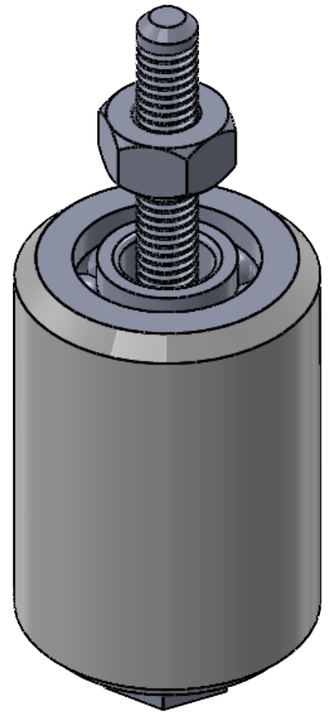



NYLON ROLLER ASM (STD)


QTY- 8 NOS

TITLE - GATE AUTOMATION				NIHVA TECHNOLOGIES PVT.LTD.PUNE Website - www.nihva.com
DWG NO - NTPL			QTY - 1	
	NAME	SIGNATURE	DATE	PROJECT NO - NTPL
DRAWN	V.B.		05-06-2025	PRODUCT - SLIDING GATE
CHK'D	S.W.		05-06-2025	SITE LOCATION - LUCKNOW
APPV'D	V.T.		05-06-2025	
if any queries contact - supportautomation@nihva.com				REVISION -
ALL DIMENSION ARE IN mm			A3	SCALE - SHEET 10 OF 21

ITEM NO.	PART NUMBER	DESCRIPTION	QTY.
1	Nylon Roller	STD	8

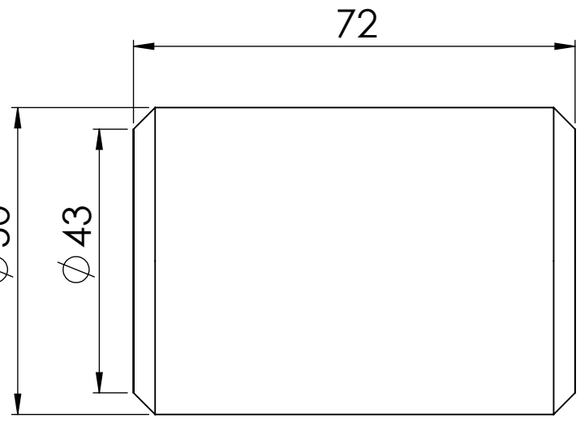

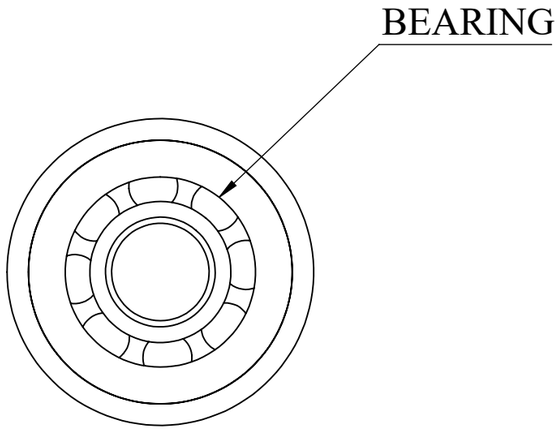


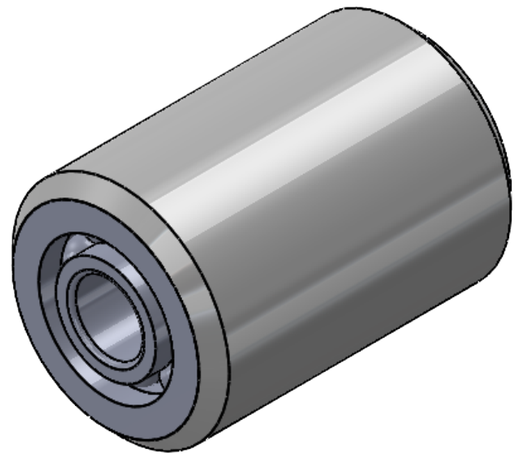


QTY:- 8 NOS


NYLON ROLLER


TITLE - GATE AUTOMATION				NIHVA TECHNOLOGIES PVT.LTD.PUNE
DWG NO - NTPL			QTY - 1	Website - www.nihva.com
	NAME	SIGNATURE	DATE	PROJECT NO - NTPL
DRAWN	V.B.		05-06-2025	PRODUCT - SLIDING GATE
CHK'D	S.W.		05-06-2025	SITE LOCATION - LUCKNOW
APPV'D	V.T.		05-06-2025	
if any queries contact - supportautomation@nihva.com				REVISION -
ALL DIMENSION ARE IN mm			A3	SCALE -

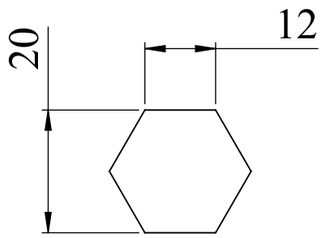

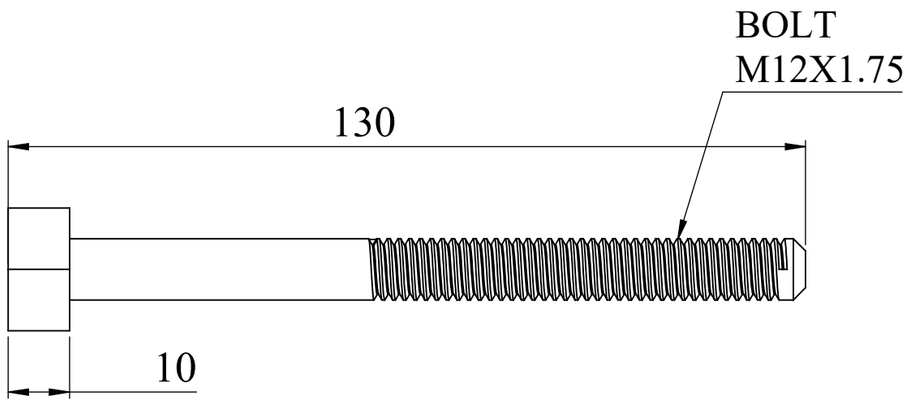

BOLT

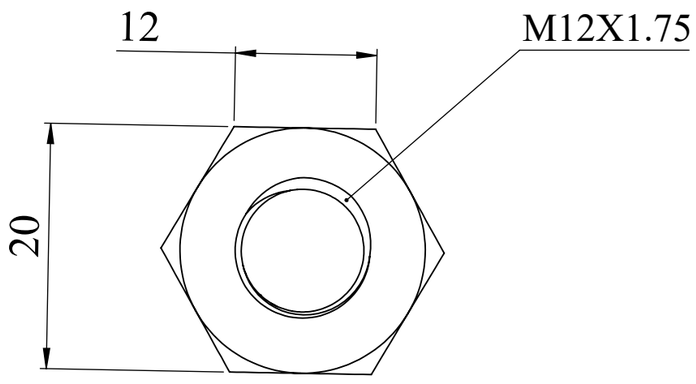

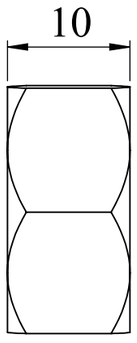



QTY- 8 NOS

NUT

TITLE - GATE AUTOMATION				NIHVA TECHNOLOGIES PVT.LTD.PUNE Website - www.nihva.com
DWG NO - NTPL			QTY - 1	
	NAME	SIGNATURE	DATE	PROJECT NO - NTPL
DRAWN	V.B.		05-06-2025	PRODUCT - SLIDING GATE
CHK'D	S.W.		05-06-2025	SITE LOCATION - LUCKNOW
APPV'D	V.T.		05-06-2025	
if any queries contact - supportautomation@nihva.com				REVISION -
ALL DIMENSION ARE IN mm			A3	SCALE - SHEET 12 OF 21

ITEM NO.	PART NUMBER	DESCRIPTION	QTY.
1	VERTICAL SQ TUBE	75.00 X 75.00 X 3.00	2
2	ROLLER SUPPORT PLATE	304X75X10	4
3	PRJ-PANKAJ-bottom plate for post		4

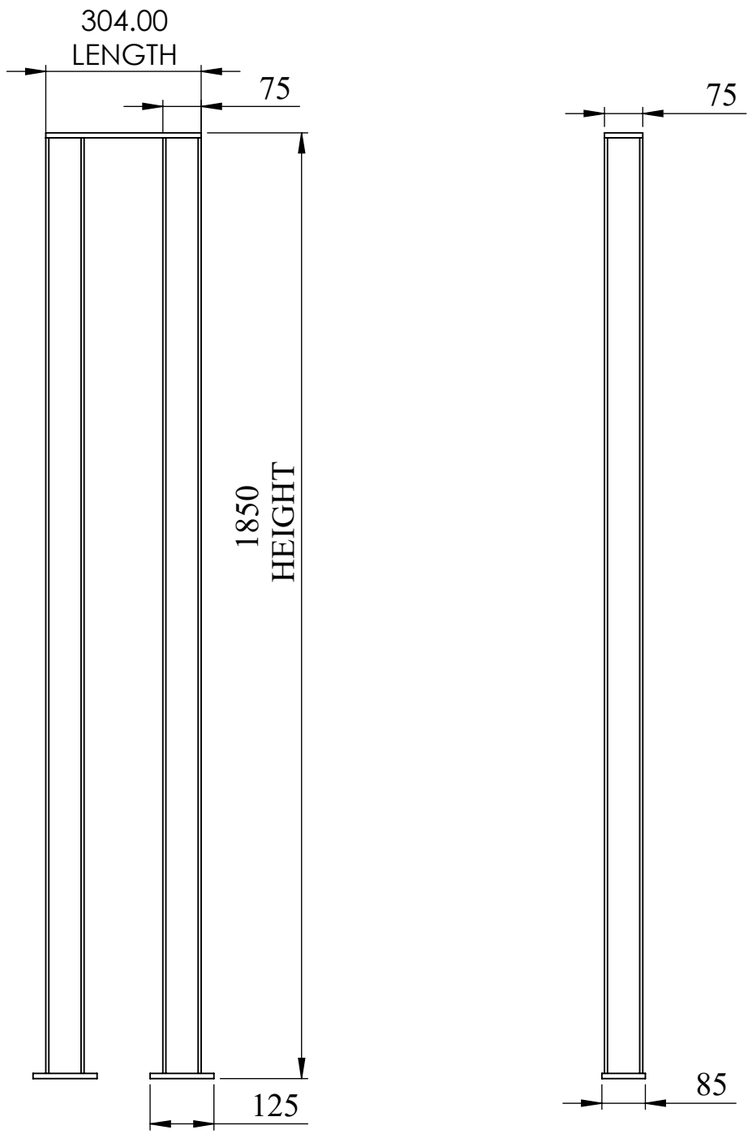


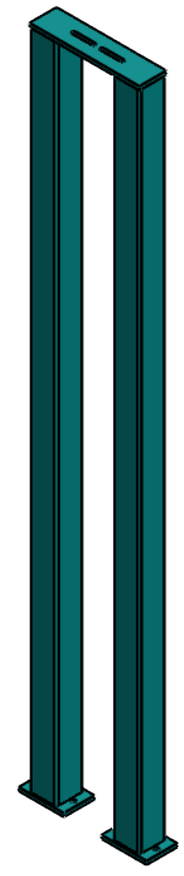


POST 1 ASM
QTY- 2NOS

TITLE - GATE AUTOMATION				NIHVA TECHNOLOGIES PVT.LTD.PUNE Website - www.nihva.com
DWG NO - NTPL			QTY - 1	
	NAME	SIGNATURE	DATE	PROJECT NO - NTPL
DRAWN	V.B.		05-06-2025	PRODUCT - SLIDING GATE
CHK'D	S.W.		05-06-2025	SITE LOCATION - LUCKNOW
APPV'D	V.T.		05-06-2025	
if any queries contact - supportautomation@nihva.com				REVISION -
ALL DIMENSION ARE IN mm			A3	SCALE - SHEET 13 OF 21

ITEM NO.	PART NUMBER	DESCRIPTION	QTY.
1	ROLLER SUPPORT PLATE	304X75X10	2

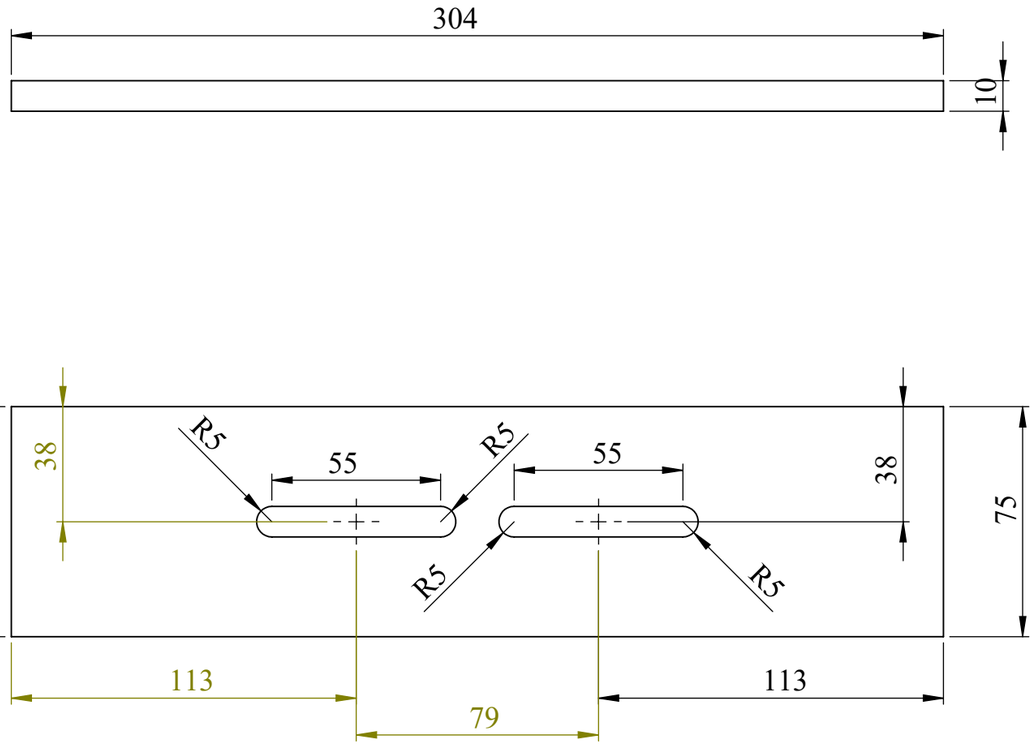


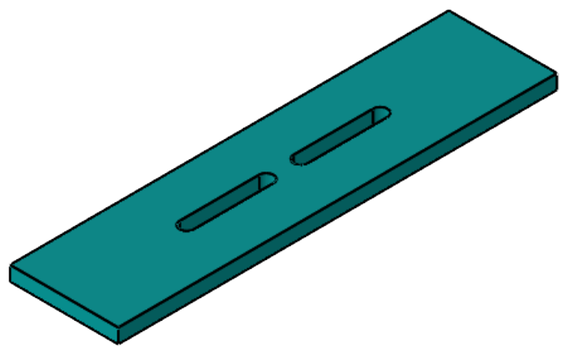

POST 1 ROLLER SUPPORT PLATE
304X75X10 THK
QTY : 2NOS

TITLE - GATE AUTOMATION				NIHVA TECHNOLOGIES PVT.LTD.PUNE Website - www.nihva.com
DWG NO - NTPL			QTY - 1	
	NAME	SIGNATURE	DATE	PROJECT NO - NTPL
DRAWN	V.B.		05-06-2025	PRODUCT - SLIDING GATE
CHK'D	S.W.		05-06-2025	SITE LOCATION - LUCKNOW
APPV'D	V.T.		05-06-2025	
if any queries contact - supportautomation@nihva.com				REVISION -
ALL DIMENSION ARE IN mm			A3	SCALE - SHEET 14 OF 21

ITEM NO.	PART NUMBER	DESCRIPTION	QTY.
1	VERTICAL SQ TUBE	75.00 X 75.00 X 3.00	8

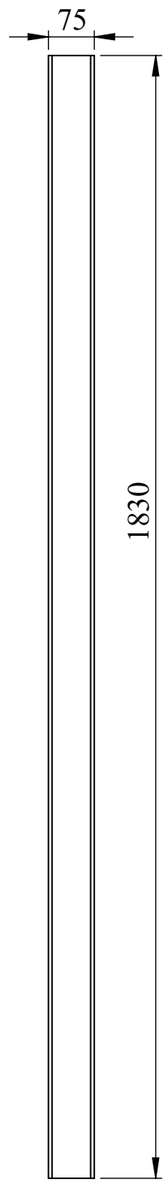






POST VERTICAL SQ. TUBE
75X75X3 THK
QTY : 8NOS

TITLE - GATE AUTOMATION				NIHVA TECHNOLOGIES PVT.LTD.PUNE Website - www.nihva.com
DWG NO - NTPL			QTY - 1	
	NAME	SIGNATURE	DATE	PROJECT NO - NTPL
DRAWN	V.B.		05-06-2025	PRODUCT - SLIDING GATE
CHK'D	S.W.		05-06-2025	SITE LOCATION - LUCKNOW
APPV'D	V.T.		05-06-2025	
if any queries contact - supportautomation@nihva.com				REVISION -
ALL DIMENSION ARE IN mm			A3	SCALE - SHEET 15 OF 21

ITEM NO.	PART NUMBER	DESCRIPTION	QTY.
1	BOTTOM PLATE FOR POST	125X85X10	8

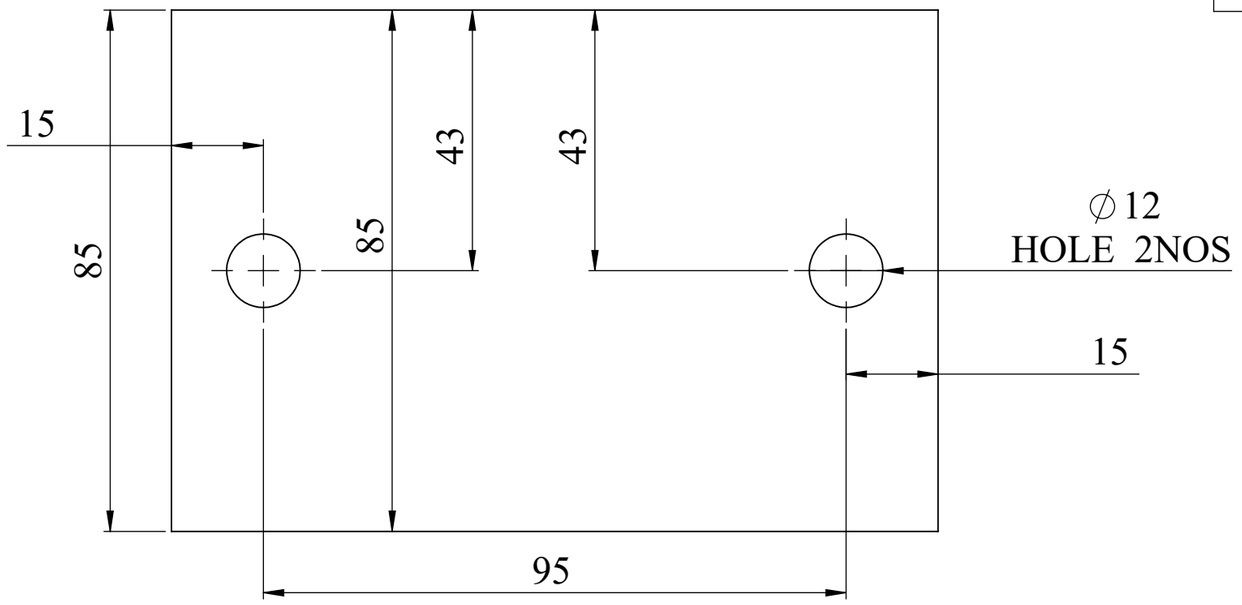

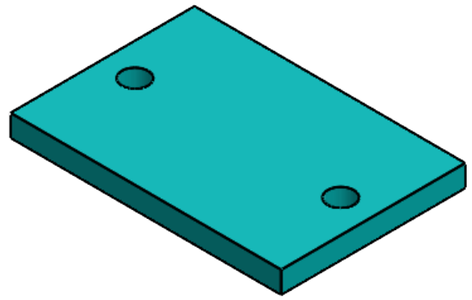

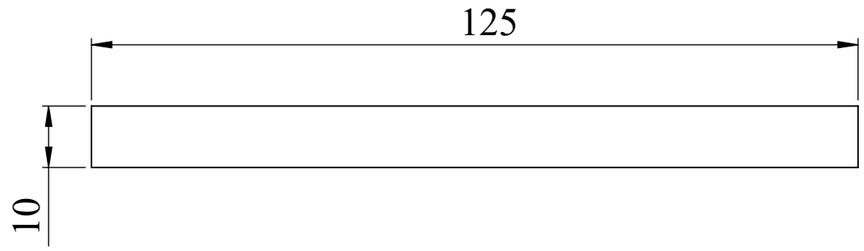


NOTE:
POST BOTTOM PLATE
MS 117X85X10 THK


THIS BOTTOM PLATE
USED SAME FOR POST 2

QTY:- 8 NOS

TITLE - GATE AUTOMATION				NIHVA TECHNOLOGIES PVT.LTD.PUNE Website - www.nihva.com
DWG NO - NTPL			QTY - 1	
	NAME	SIGNATURE	DATE	PROJECT NO - NTPL
DRAWN	V.B.		05-06-2025	PRODUCT - SLIDING GATE
CHK'D	S.W.		05-06-2025	SITE LOCATION - LUCKNOW
APPV'D	V.T.		05-06-2025	
if any queries contact - supportautomation@nihva.com				REVISION -
ALL DIMENSION ARE IN mm			A3	SCALE -

ITEM NO.	PART NUMBER	DESCRIPTION	QTY.
1	ROLLER SUPPORT PLATE	535X320X10	1
2	BOTTOM PLATE	125X85X10	8
3	BOTTOM PLATE	125X85X10	8

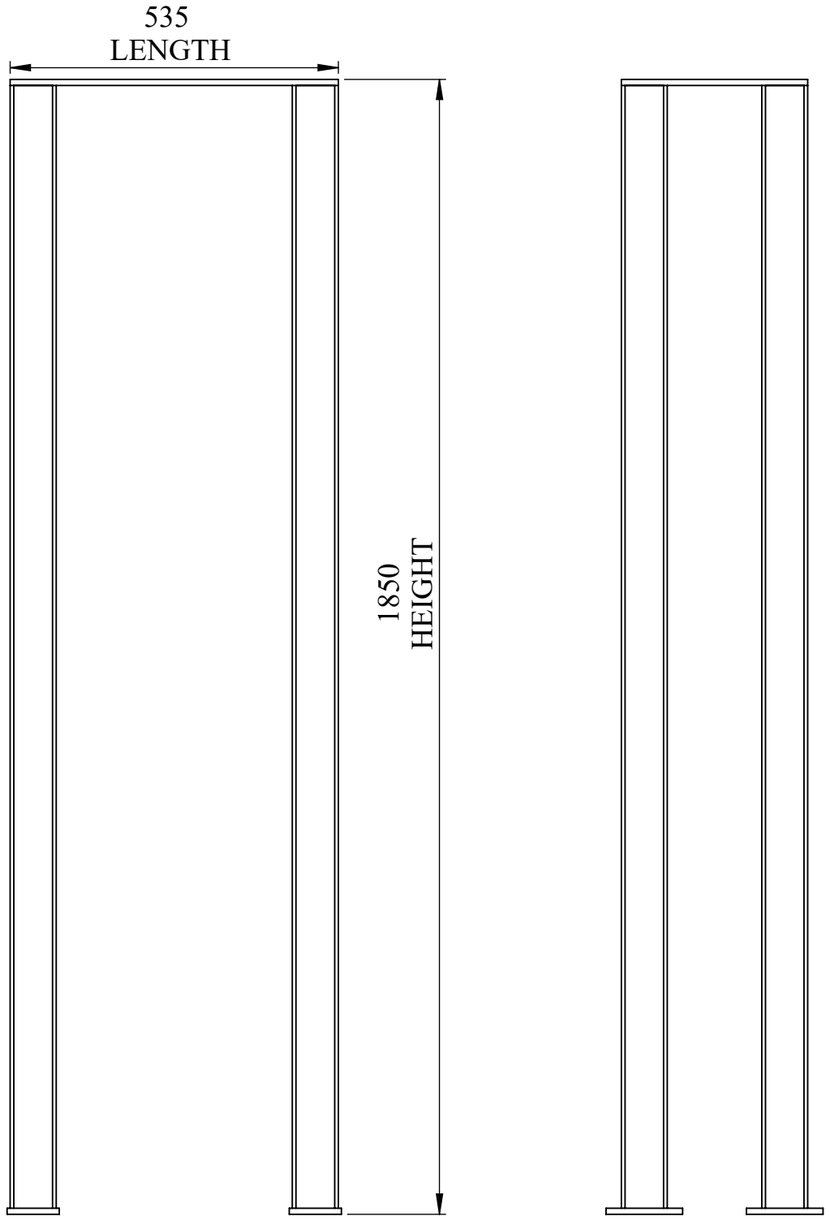


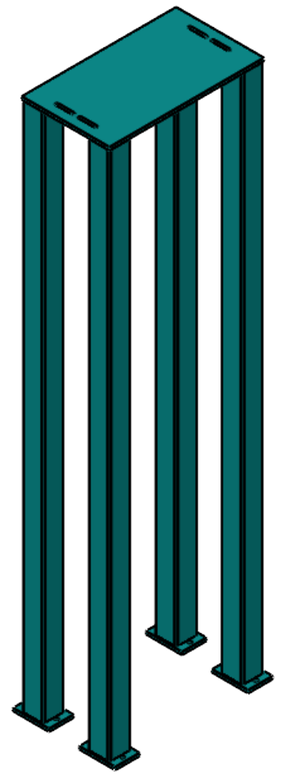


POST 2 ASM
QTY- 1NOS

TITLE - GATE AUTOMATION				NIHVA TECHNOLOGIES PVT.LTD.PUNE Website - www.nihva.com
DWG NO - NTPL			QTY - 1	
	NAME	SIGNATURE	DATE	PROJECT NO - NTPL
DRAWN	V.B.		05-06-2025	PRODUCT - SLIDING GATE
CHK'D	S.W.		05-06-2025	SITE LOCATION - LUCKNOW
APPV'D	V.T.		05-06-2025	
if any queries contact - supportautomation@nihva.com				REVISION -
ALL DIMENSION ARE IN mm			A3	SCALE - SHEET 17 OF 21

ITEM NO.	PART NUMBER	DESCRIPTION	QTY.
1	ROLLER SUPPORT PLATE	535X304X10	1

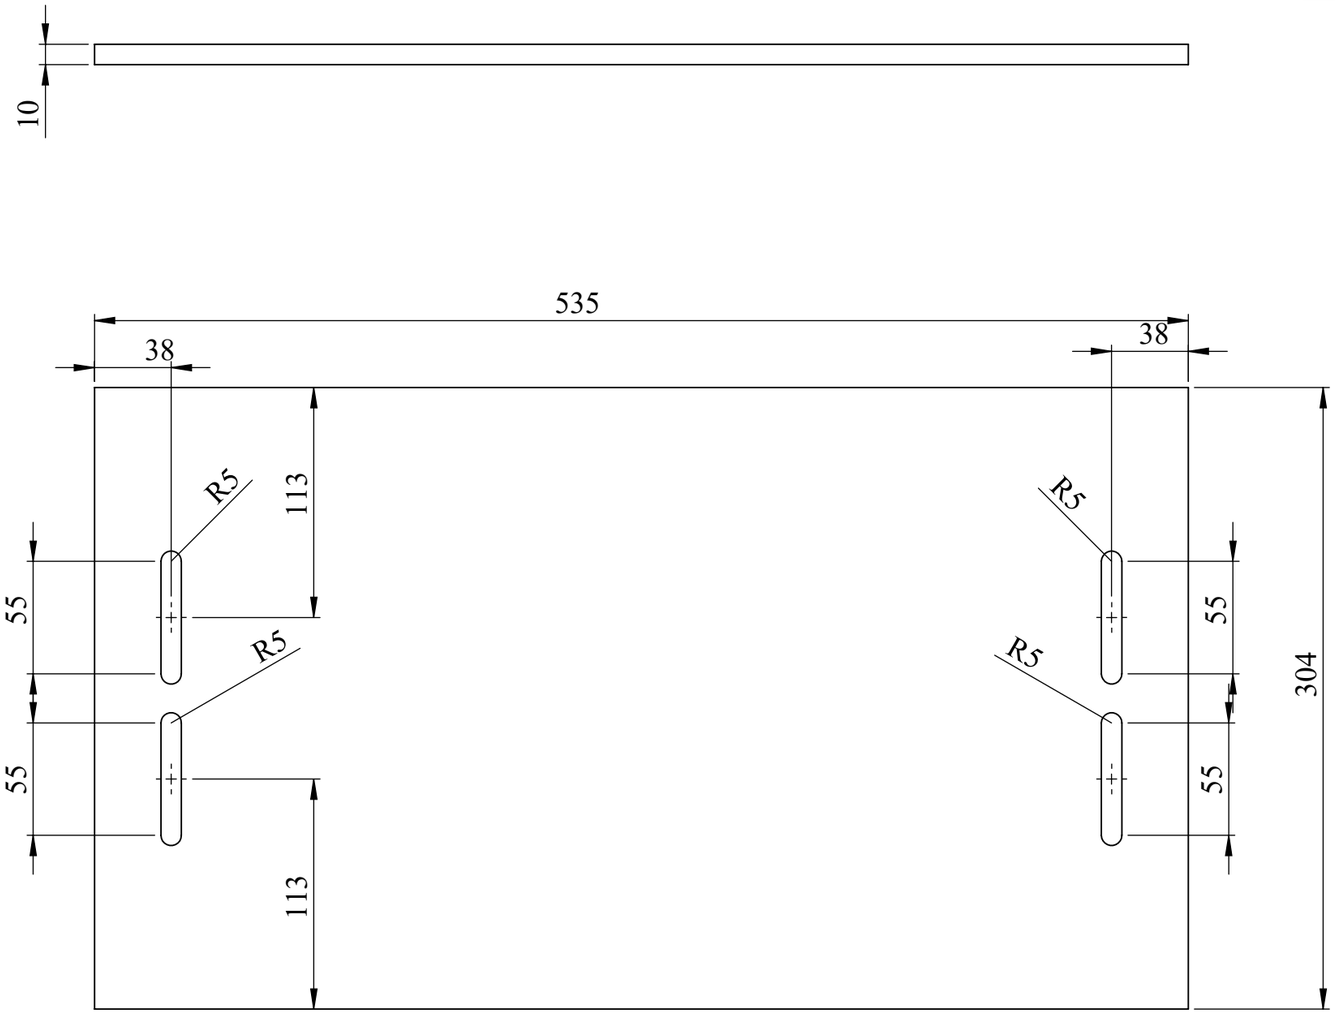


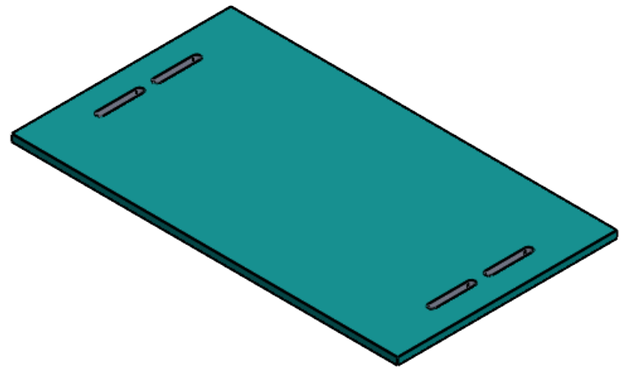



POST 2 ROLLER SUPPORT PLATE
535X304X10 THK
QTY : 1NOS

TITLE - GATE AUTOMATION				NIHVA TECHNOLOGIES PVT.LTD.PUNE
DWG NO - NTPL			QTY - 1	Website - www.nihva.com
	NAME	SIGNATURE	DATE	PROJECT NO - NTPL
DRAWN	V.B.		05-06-2025	PRODUCT - SLIDING GATE
CHK'D	S.W.		05-06-2025	SITE LOCATION - LUCKNOW
APPV'D	V.T.		05-06-2025	
if any queries contact - supportautomation@nihva.com				REVISION -
ALL DIMENSION ARE IN mm			A3	SCALE - SHEET 18 OF 21

ITEM NO.	PART NUMBER	DESCRIPTION	QTY.
1	GATE TRACK	(L) - 17200MM	1
	ISMB BEAM	100.00 X 8	1

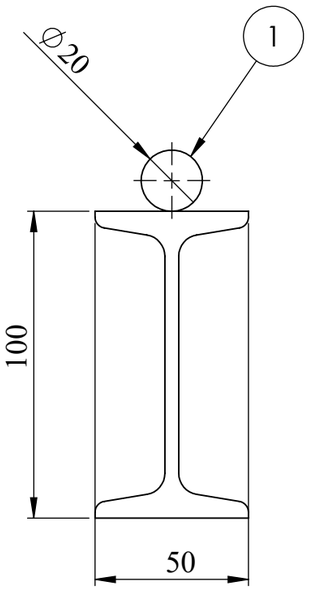

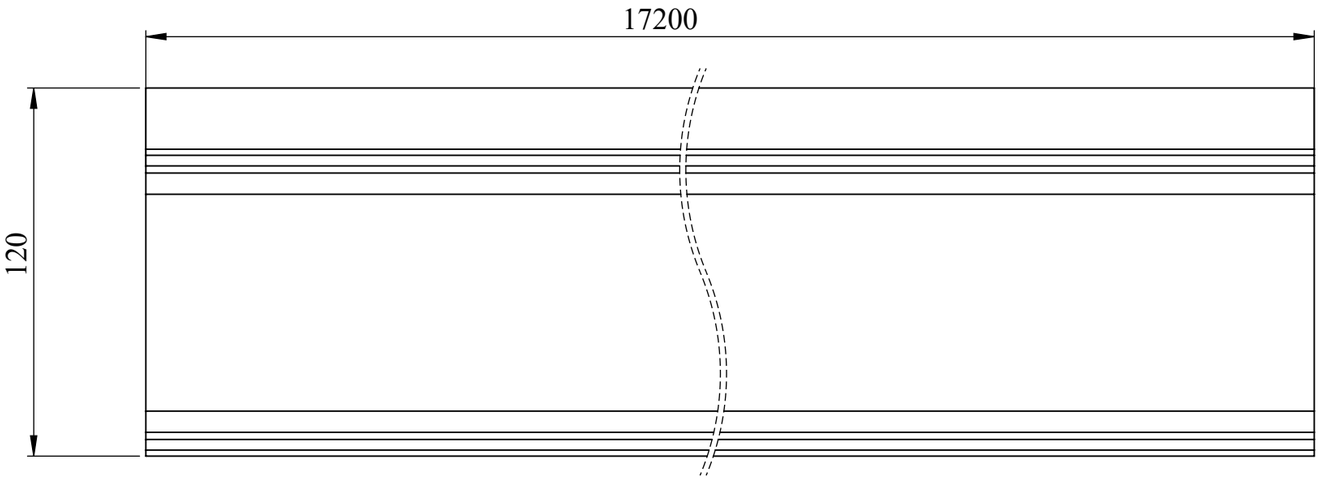


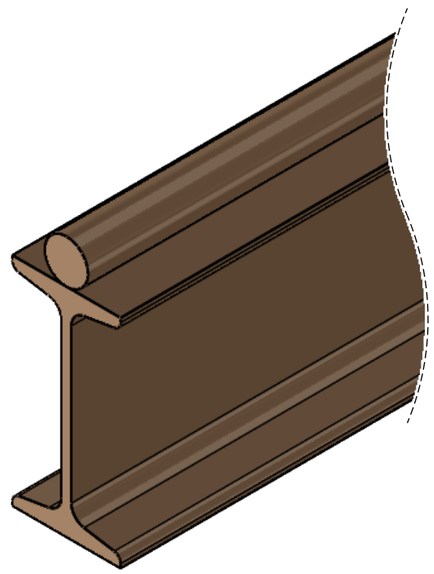


GATE TRACK
QTY-1NOS

TITLE - GATE AUTOMATION				NIHVA TECHNOLOGIES PVT.LTD.PUNE Website - www.nihva.com
DWG NO - NTPL			QTY - 1	
	NAME	SIGNATURE	DATE	PROJECT NO - NTPL
DRAWN	V.B.		05-06-2025	PRODUCT - SLIDING GATE
CHK'D	S.W.		05-06-2025	SITE LOCATION - LUCKNOW
APPV'D	V.T.		05-06-2025	
if any queries contact - supportautomation@nihva.com				REVISION -
ALL DIMENSION ARE IN mm			A3	SCALE -

ITEM NO.	PART NUMBER	DESCRIPTION	QTY.
1	RACK	STD (1000MM)	8

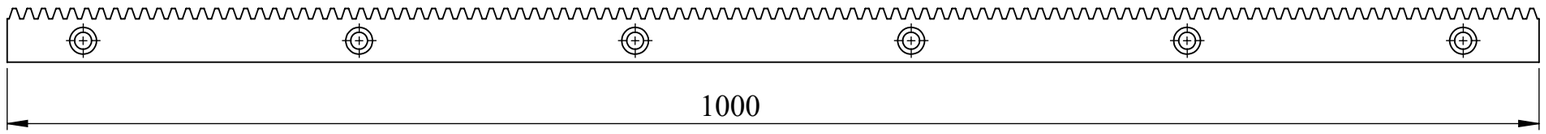


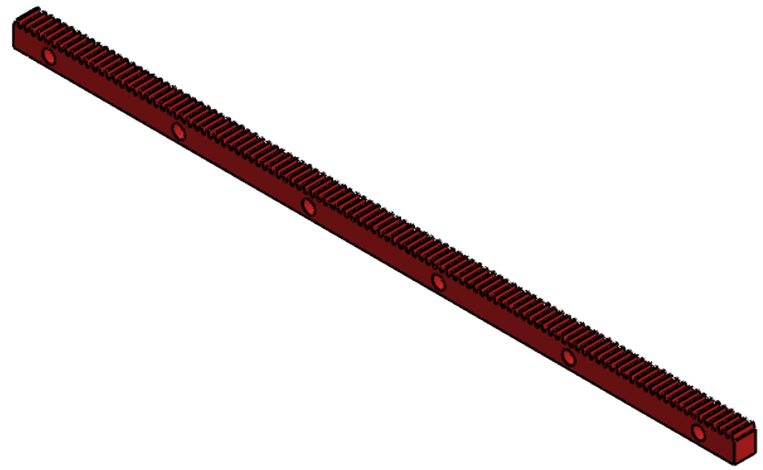


RACK
QTY-8NOS

TITLE - GATE AUTOMATION				NIHVA TECHNOLOGIES PVT.LTD.PUNE Website - www.nihva.com
DWG NO - NTPL			QTY - 1	
	NAME	SIGNATURE	DATE	PROJECT NO - NTPL
DRAWN	V.B.		05-06-2025	PRODUCT - SLIDING GATE
CHK'D	S.W.		05-06-2025	SITE LOCATION - LUCKNOW
APPV'D	V.T.		05-06-2025	
if any queries contact - supportautomation@nihva.com				REVISION -
ALL DIMENSION ARE IN mm			A3	SCALE - SHEET 20 OF 21

ITEM NO.	PART NUMBER	DESCRIPTION	QTY.
1	CUT RACK PART	CUT RACK 600MM (L)	1

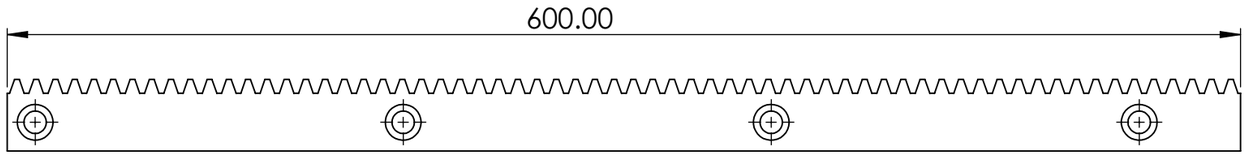

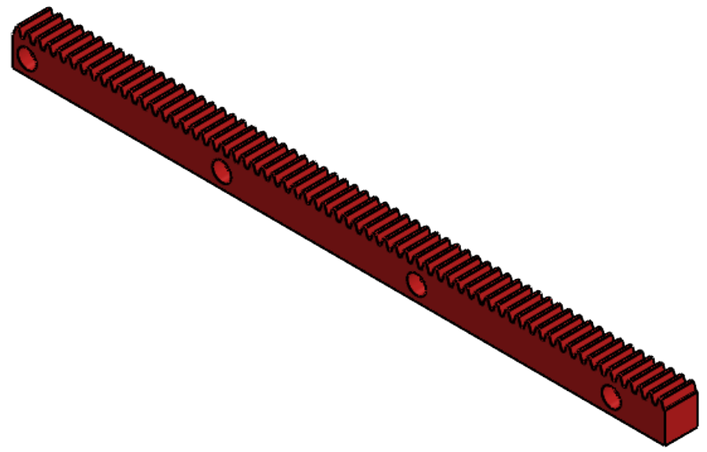

CUT RACK PART
QTY- 1NOS

TITLE - GATE AUTOMATION				NIHVA TECHNOLOGIES PVT.LTD.PUNE Website - www.nihva.com
DWG NO - NTPL			QTY - 1	
	NAME	SIGNATURE	DATE	PROJECT NO - NTPL
DRAWN	V.B.		05-06-2025	PRODUCT - SLIDING GATE
CHK'D	S.W.		05-06-2025	SITE LOCATION - LUCKNOW
APPV'D	V.T.		05-06-2025	
if any queries contact - supportautomation@nihva.com				REVISION -
ALL DIMENSION ARE IN mm			A3	SCALE - SHEET 21 OF 21