Revision		Date	By
A	Corrected mullion hoist positions, floor pits altered	2022-09-02	EB

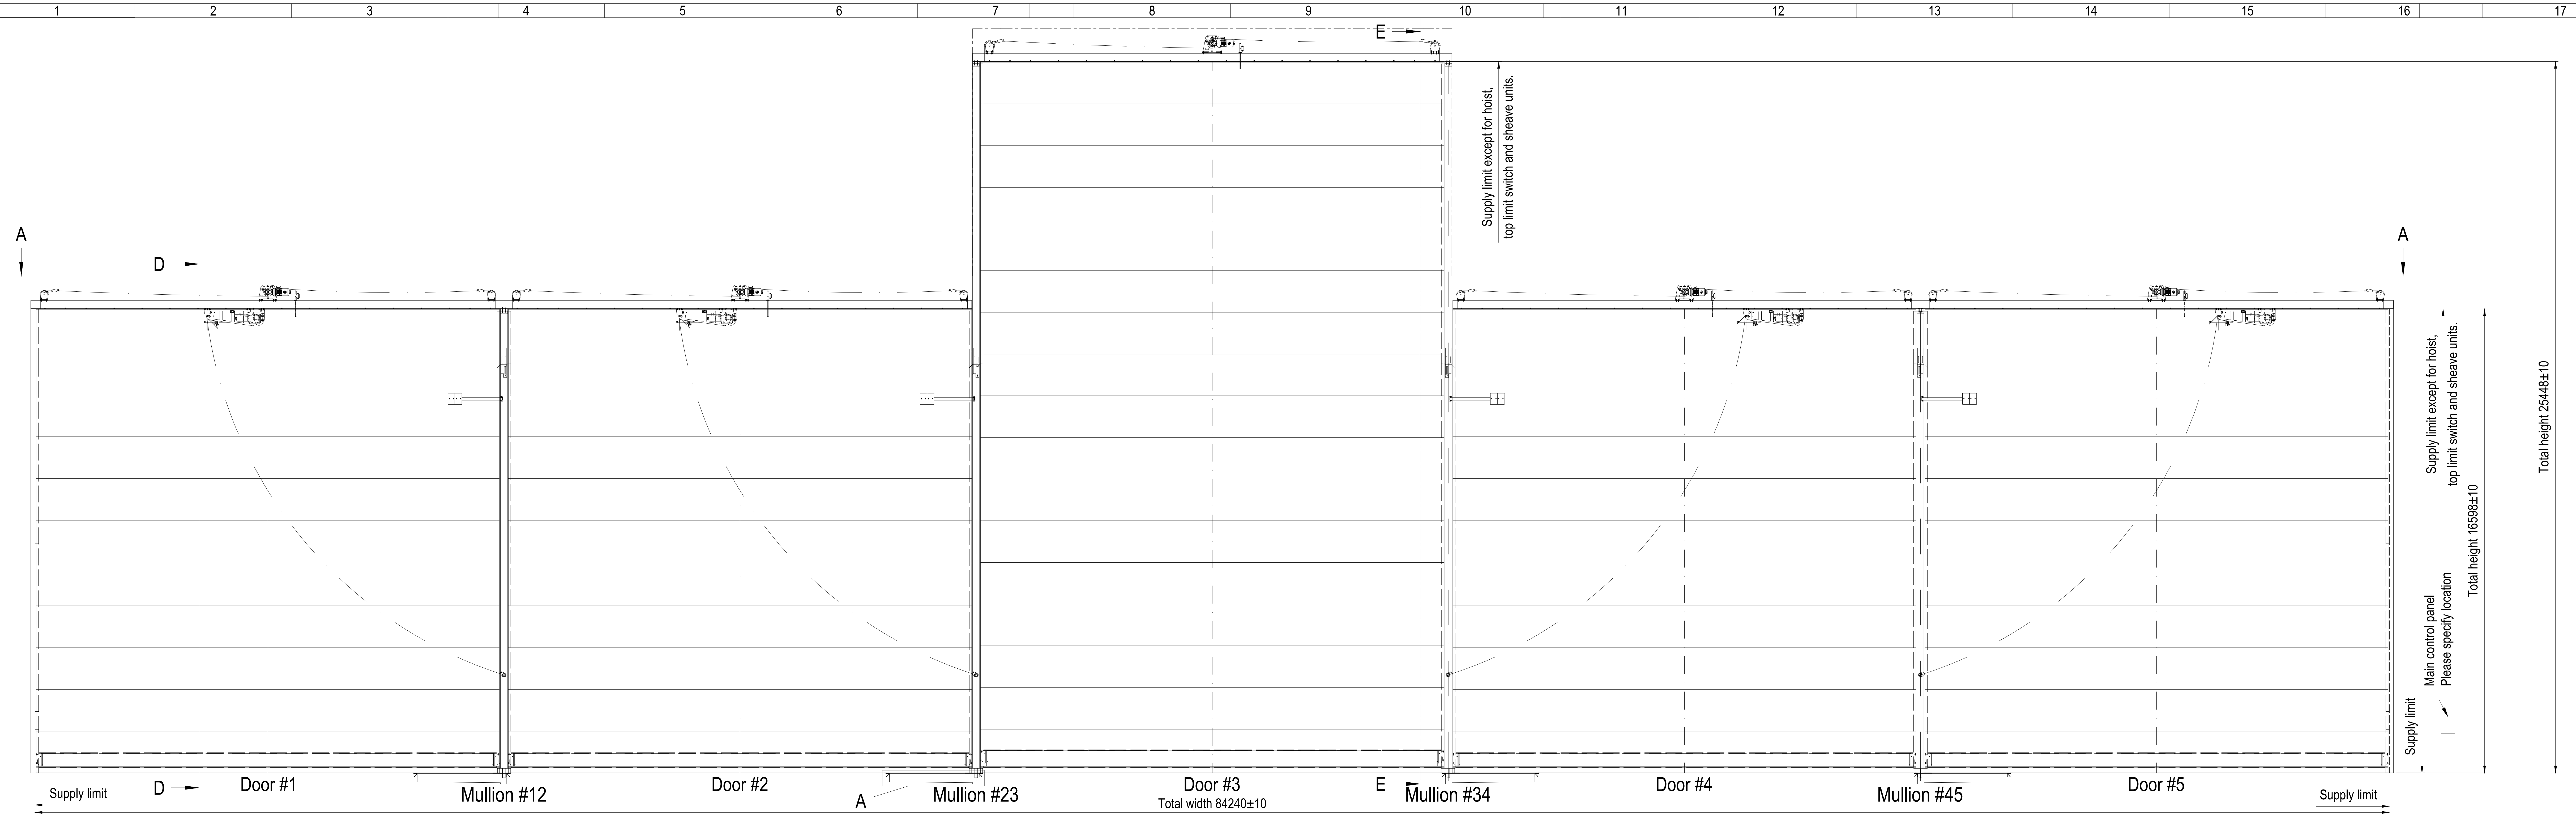

Interior view, door closed

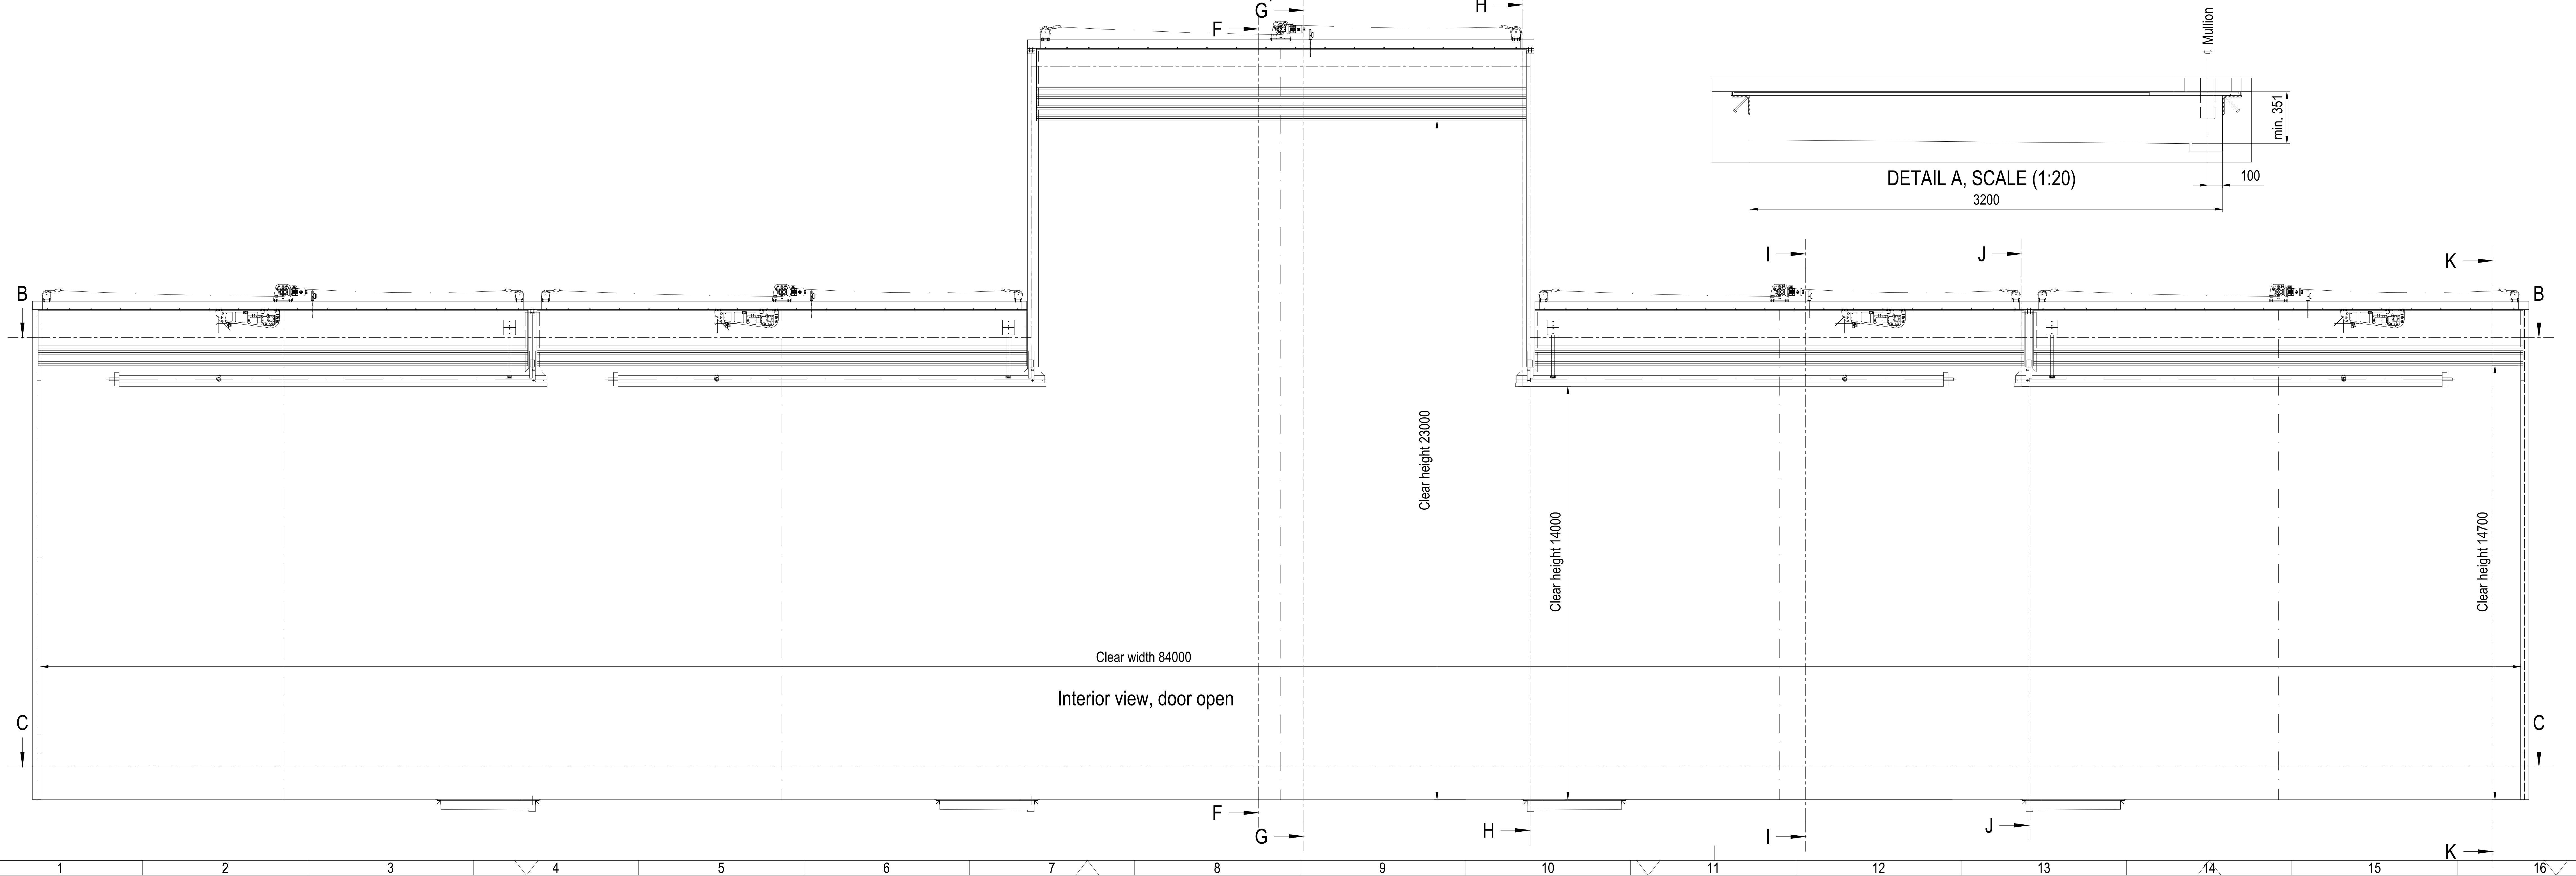

DETAIL A, SCALE (1:20)

Interior view, door open

5.9T/27 Door #3

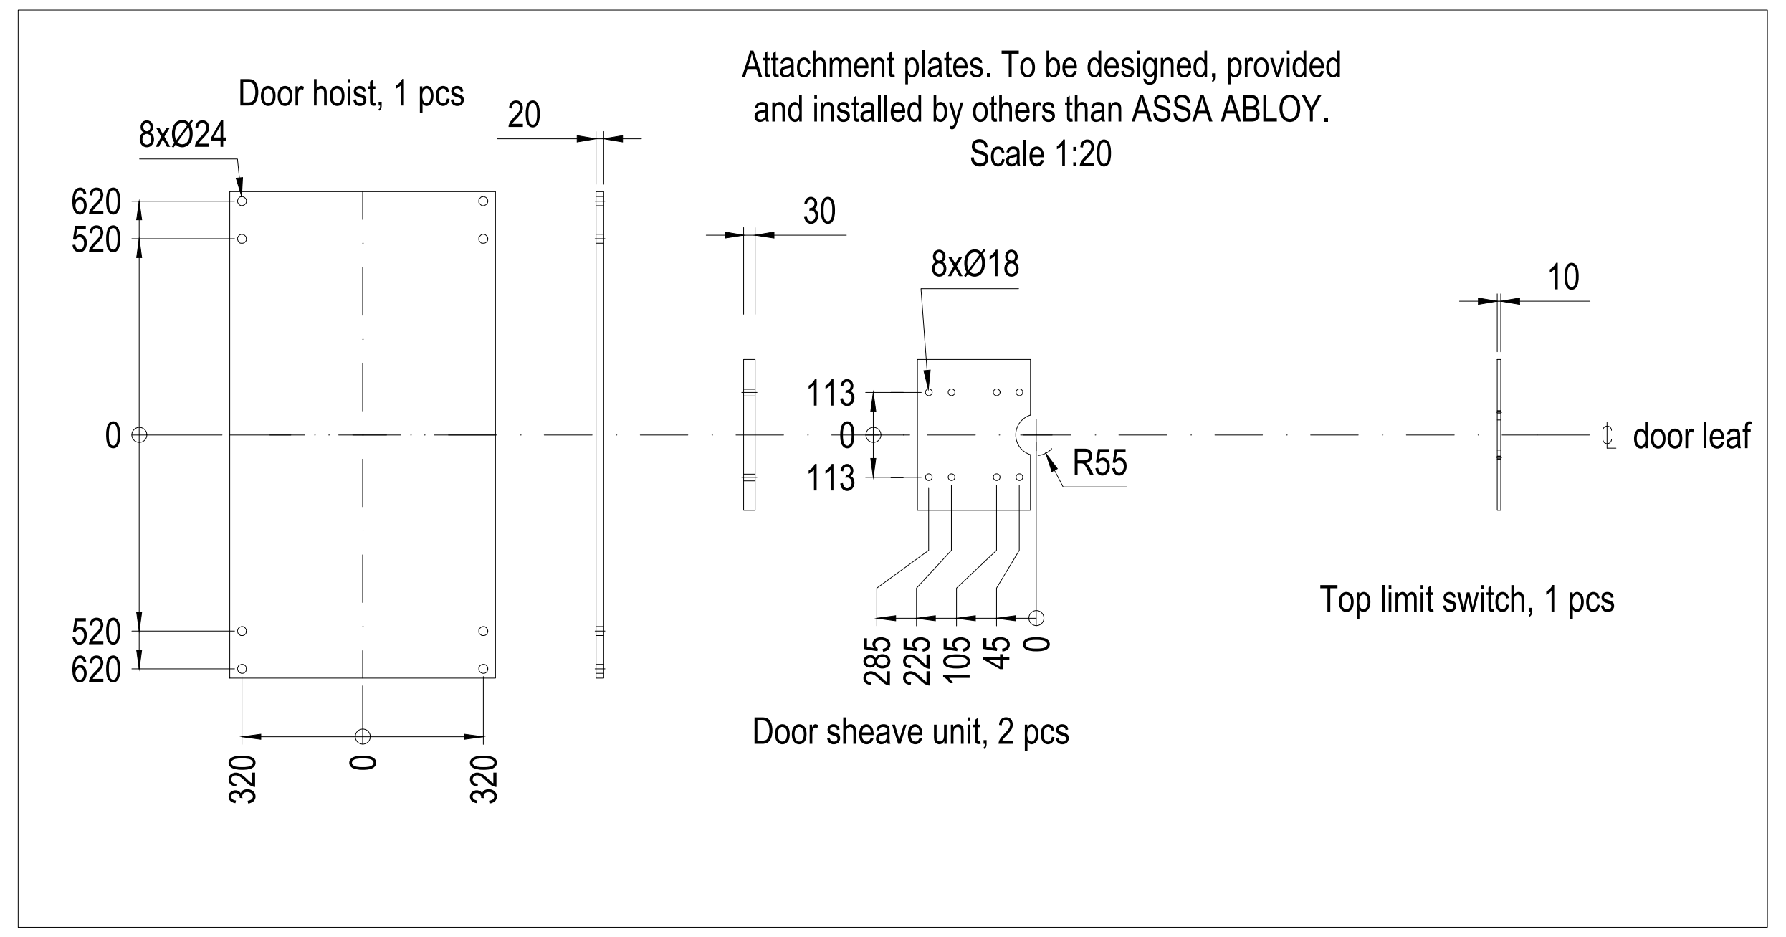

Attachment plates. To be designed, provided and installed by others than ASSA ABLOY.
Scale 1:20

Door sheave unit, 2 pcs

Top limit switch, 1 pcs

4.9T/27 Door #1, 2, 4 & 5

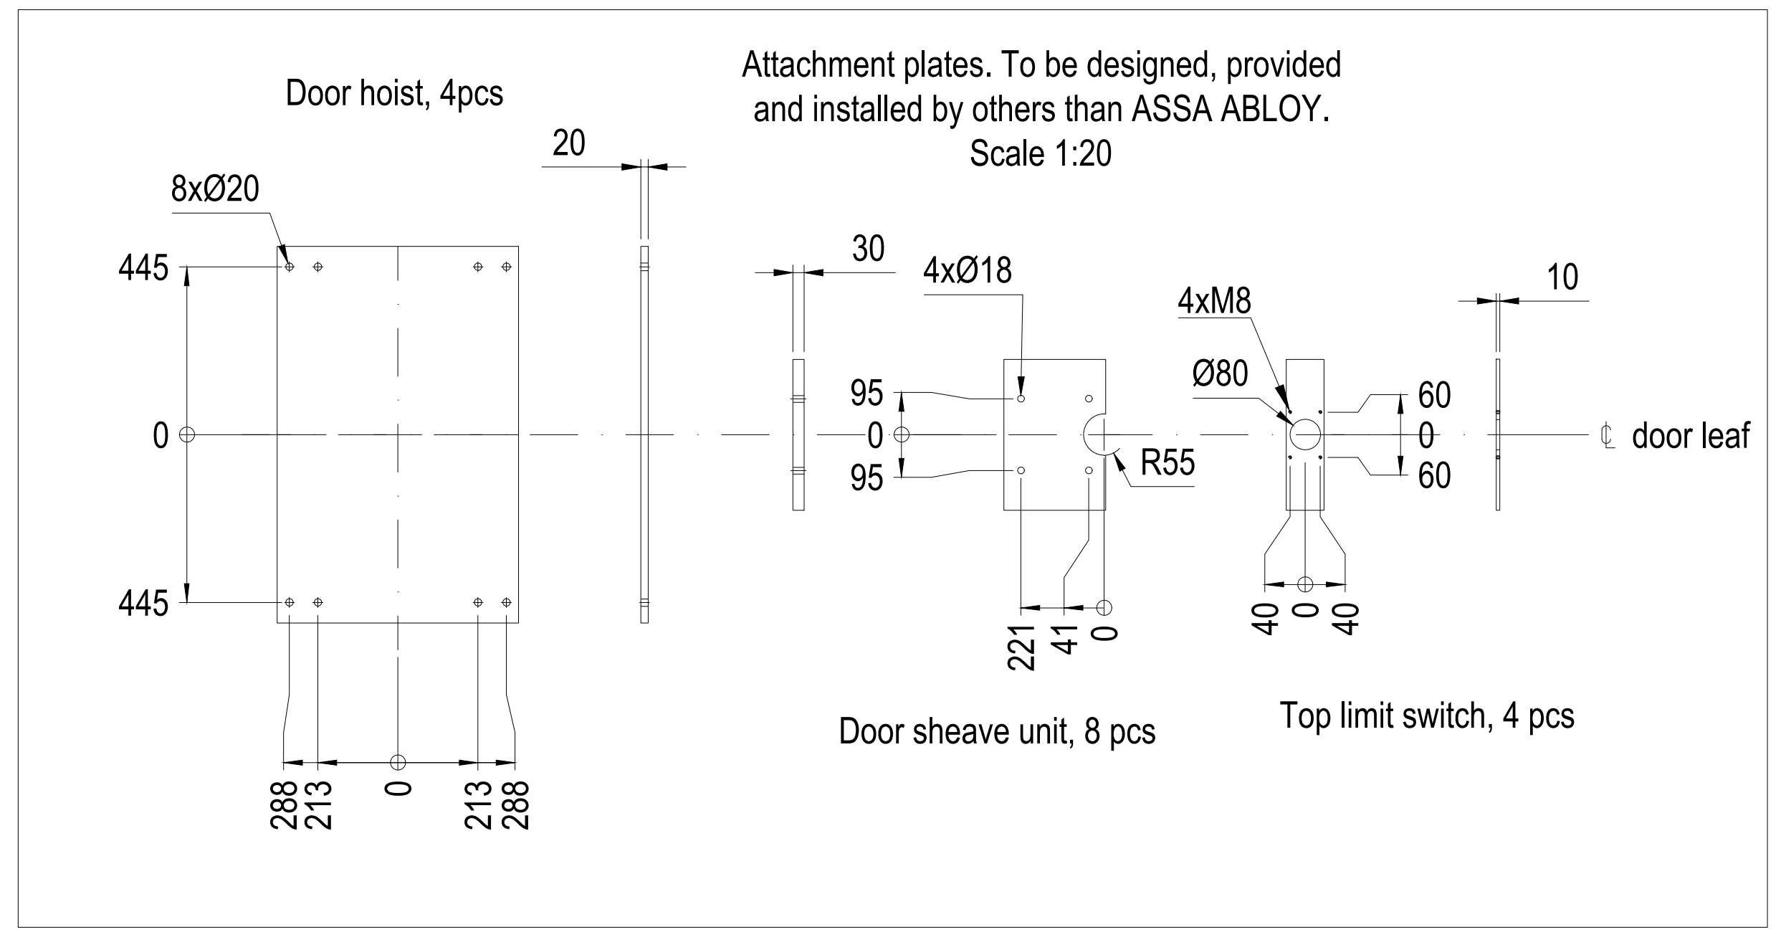

Attachment plates. To be designed, provided and installed by others than ASSA ABLOY.
Scale 1:20

Door sheave unit, 8 pcs

Top limit switch, 4 pcs

DOOR IDENTITY NUMBER: 84800001

LOAD DIAGRAM & NOTES, ref. to drwng. no. 77446

INTERFACE, SECTIONS ref. to drwng. no. 77445

INTERFACE, PLAN VIEWS ref. to drwng. no. 77444

DESIGNED		SIZE	SCALE	GMR Aero Technic Hangar1 India Megadoor 84000x23000/14000 Interface, Elevation	PLOT DATE
EB		A1F	1:100		
CODE 84800		If not otherwise stated: Tolerances ISO 2768-m EN ISO 13920-B Cutting class ISO 9013-442 Weld class ISO 5817-C Surface finish Smooth raw surface			
ITEM NO					
DATE 2022-08-23				DRAWING NO 77443	REVISION A
ASSA ABLOY					

This document is the property of ASSA ABLOY Entrance Systems AB and shall not without our written permission be copied, imparted to a third party or used for any other unauthorized purpose.