



REV.	DWG NO		TITLE
XX	XXXX	1/1	TITLE

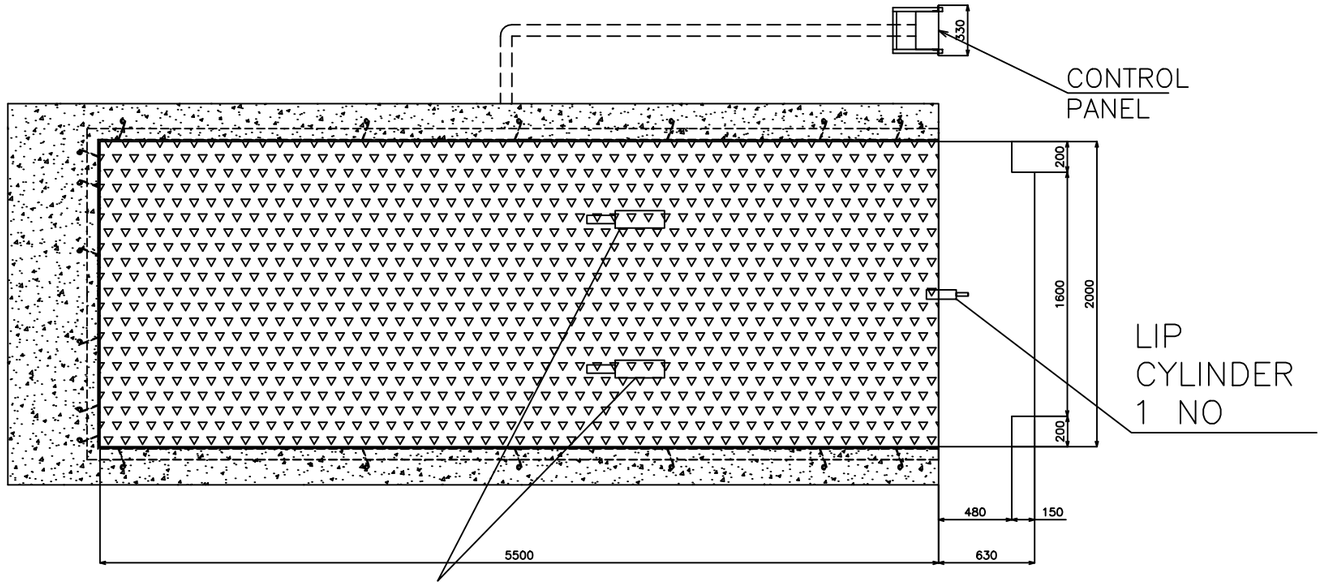

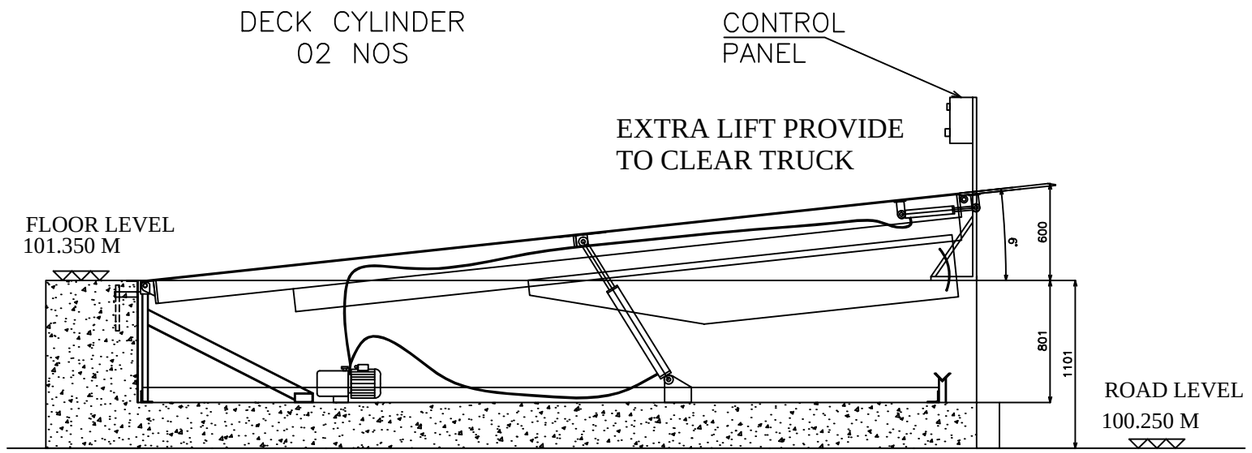

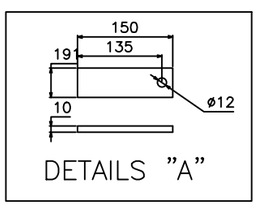

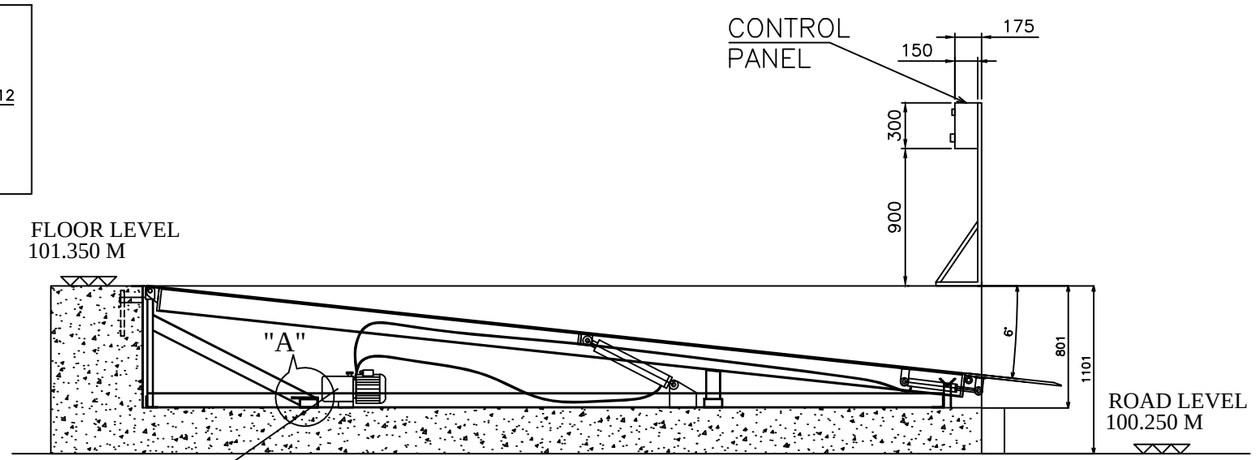

NOTE: –

1. PROPER DRAINAGE SHOULD BE DONE.
2. FABRICATION TOLERANCE FOR PLATFORM SIZE WILL BE + 10 MM.
3. PLEASE NOTE THAT THE CAPACITY OF DOCK LEVELER (6 TON) CONSIDERED IS THE CAPACITY AFTER THE LIP IS RESTED ON THE VEHICLE.
4. CYLINDERS PROVIDED ARE INDENTED TO BE USED ONLY FOR LIFTING OF BARE DOCK & CAN NOT LIFT OTHER LOADS.
5. TARE WEIGHT OF DOCK LEVELER :approx. 2000KG.

DATASHEET FOR DOCK LEVELER

Sr. No	Parameter	Remark
1	Required Capacity	06 Ton
2	Leveler operation mode	AC power pack hydraulically operated
3	Lip operation mode	hydraulic
4	Operation control	by push buttons and control panel
5	Loading platform height from roadLevel	1100 mm
6	Travel above & below dock level	600 mm
7	Platform Size (W x L)	2000 mm x 5500 mm
8	Lip size (W x L)	2000 mm x 630 mm
9	Maximum slope can be achieved	6 Degree

Drawing/ Document Category (Submission Purpose)	Drawing/Document Review Status (BY OWNER/PMC)		
	APPROVAL CODE	STATUS	ACTION REQUIRED
☑ For Approval	1	Rejected	Revise and resubmit
☐ For Review	2	Commented as noted	Work may proceed subject to acceptance and incorporation of comments.
☐ For Information	3	Acceptable with minor comments	Incorporate comments, if any. Resubmit as certified final.Work may proceed.
	4	Approved with No comments–FINAL	Work may proceed.
	5	Information Only	Accepted for information only.Work may proceed.

Date: __/__/____ Name : _____

This approval does not absolve the CONTRACTOR from meeting their contractual obligations of delivering a complete safe and efficiently operating unit facilities meeting all requirements of the contract.

REV	PURPOSE	PREPARE	CHKD	APPROVAL	DATE dd/mm/yy
A3	ADDING TARE WEIGHT OF DOCK LEVELER	PRADEEP	GAURAV	AMIT	09/07/2020
A2	ADDING CONTROL PANEL DETAILS	PRADEEP	GAURAV	AMIT	16/05/2020
A1	ISSUED FOR APPROVAL	PRADEEP	GAURAV	AMIT	19/02/2020

PROJECT
ETHYLENE GLYCOL PROJECT
PARADIP REFINERY, ODISHA-INDIA.

OWNER
INDIAN OIL CORPORATION LIMITED
PARADIP REFINERY, ODISHA, INDIA

This Drawing is the Property of INDIAN OIL CORPORATION LTD and is lent without consideration other than the Borrower's agreement that it shall not be reproduced, copied lent or disposed of directly or indirectly, nor used for any purpose other than that for which it is specifically furnished. The apparatus shown in the drawing is covered by patents information contained in this drawing may be proprietary to Indian Oil Corporation Ltd and/or licensors, and is subject to obligations of confidentiality.

L&T - CHIYODA LIMITED

- ☐ REVIEW CODE 1 – REJECTED REVISE & RESUBMIT.
- ☐ REVIEW CODE 2 – COMMENTED AS NOTED. WORK MAY PROCEED SUBJECT TO ACCEPTANCE AND INCORPORATION OF COMMENTS.
- ☐ REVIEW CODE 3 – ACCEPTABLE WITH MINOR COMMENTS INCORPORATE COMMENTS, IF ANY. RESUBMIT AS CERTIFIED FINAL. WORK MAY PROCEED.
- ☐ REVIEW CODE 4 – APPROVED WITH NO COMMENTS – FINAL WORK MAY PROCEED.
- ☐ REVIEW CODE 5 – INFORMATION ONLY ACCEPTED FOR INFORMATION ONLY. WORK MAY PROCEED.

COMMENTED BY	REVIEWED BY	APPROVED BY	DATE

THIS REVIEW / APPROVAL DOES NOT RELIEVE THE VENDOR / MANUFACTURER OF THE FULL RESPONSIBILITY AS TO DESIGN CORRECTNESS OF DIMENSIONS & COMPLIANCE WITHALL APPLICABLE REGULATIONS AND WITH THE REQUIREMENTS MADE IN PURCHASER SPECIFICATIONS.

PMC
Toyo Engineering India Private Limited
Mumbai, India

TEIPL's Job No. 6389 WORK ORDER No. 25574423

LSTK–2
L&T Hydrocarbon Engineering

LSTK–2 Job No. IOCL–O&U WORK ORDER No. LATER

DETAILED ENGINEERING CENTER: **L&T - CHIYODA LIMITED**

TITLE
UNIT NO–207D

DATA SHEET WITH GAD FOR DOCK LEVELER

SCALE 1:1 | DWG. NO. IPEG–6389–NTPL(1)–8470–DS–2070–0001 | REV. 1/1 A2

CAD FILE REF: CFR