

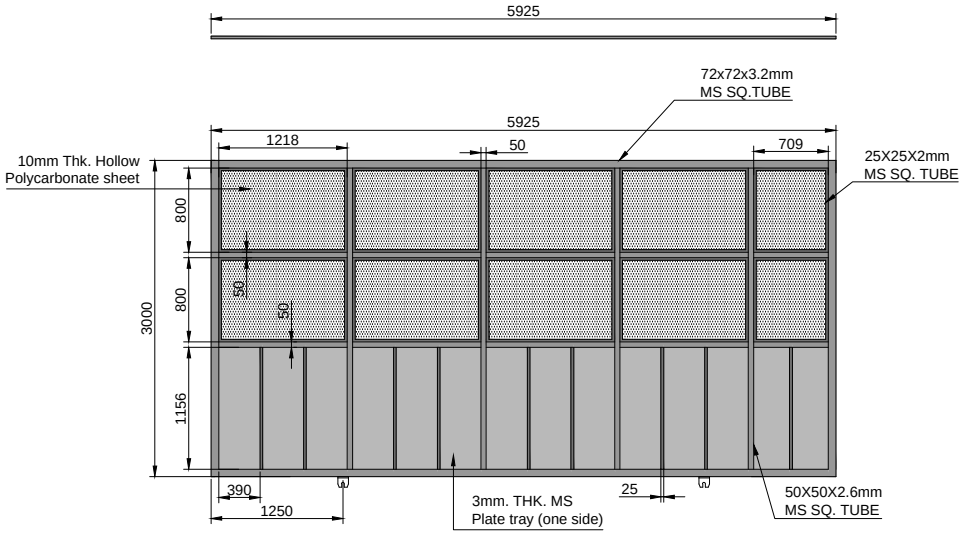



Qty- 1

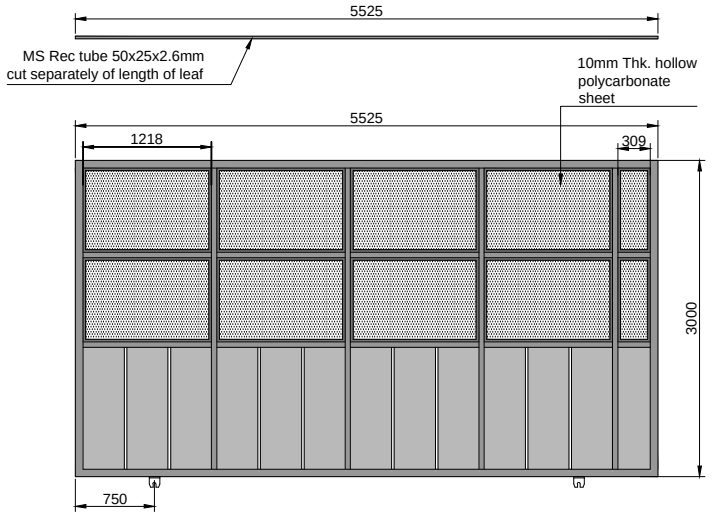


Qty- 1

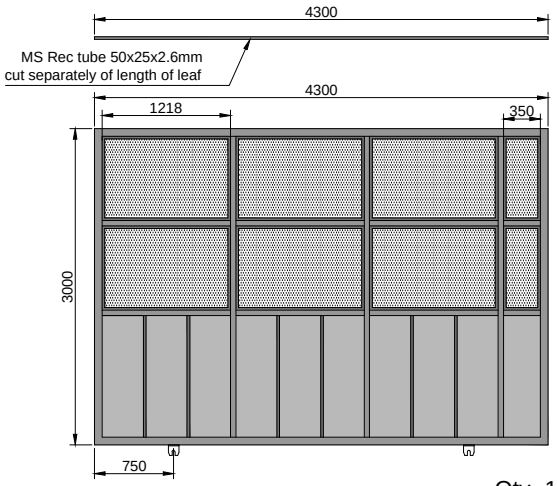

Qty- 1

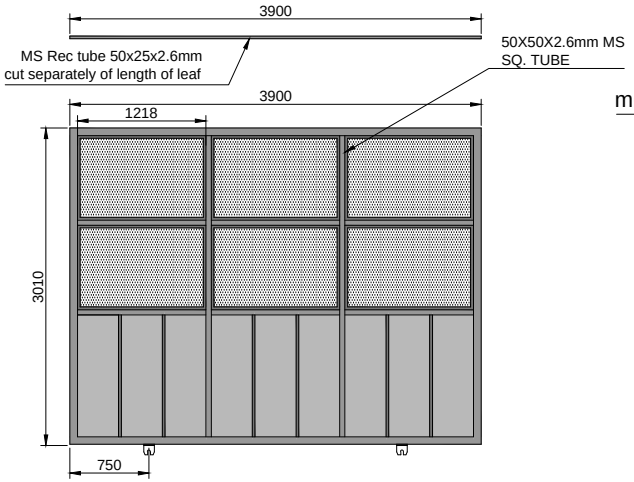


Qty- 1

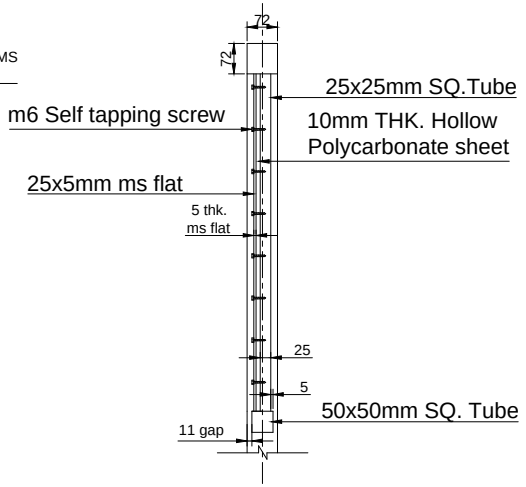

Gate leaf section details

MATERIAL SPECIFICATION		
SR NO	TUBE SIZE	
1	MS TUBE 72X72X3.2mm	OUTER TUBE
2	MS TUBE 50X50X2.6mm	INTERMEDIATE TUBE
3	MS TUBE 25X25X2mm	INNER TUBE
4	3mm MS SHEET	AT LOWER SIDE
5	10mm THK. HOLLOW POLYCARBONATE SHEET (TRANSPARENT)	AT UPPER SIDE
6	MS 25X5mm FLAT	FIXING OF POLYCARBONATE SHEET

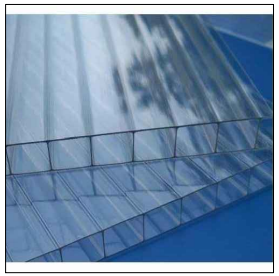

10mm THK. Hollow polycarbonate sheet(Transperent without color)

TOLERANCE - ±5mm

This drawing & design is the property of NIHVA TECHNOLOGIES. Not to be sold or copied to any other concern.

TITLE
LEAFS OF TELESCOPIC GATE

	NAME	DATE
DRAWN	OMKAR	26/02/18
CHECK	SHEKHAR	26/02/18
REV.		
APPROVAL	SHEKHAR	26/02/18

If any queries contact : projects@nihva.com

ALL DIMENSION ARE IN mm

NIHVA
NIHVA TECHNOLOGIES PVT. LTD.

NIHVA TECHNOLOGIES
PVT. LTD. PUNE
Tel : 020 66304033
Email:- info@nihva.com
Website:- www.nihva.com

CLIENT -
PROJECT -
SITE LOCATION -
DWG. NO. : NIHVA/17-18/VDR/0250 | REV-0
SCALE: NTS | WT: | SHEET: 01 OF 01