
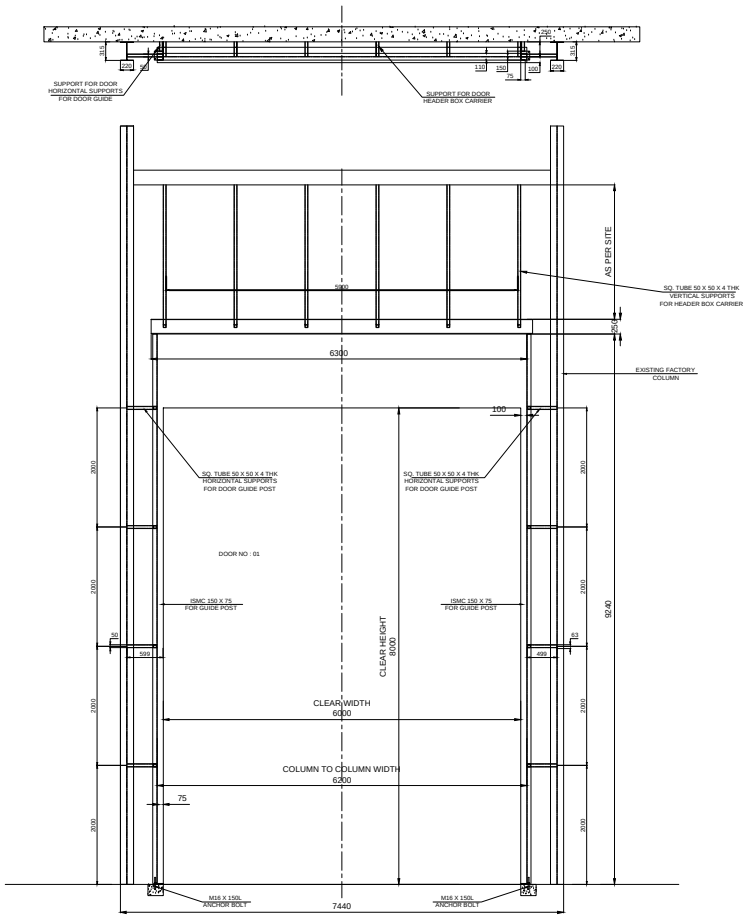


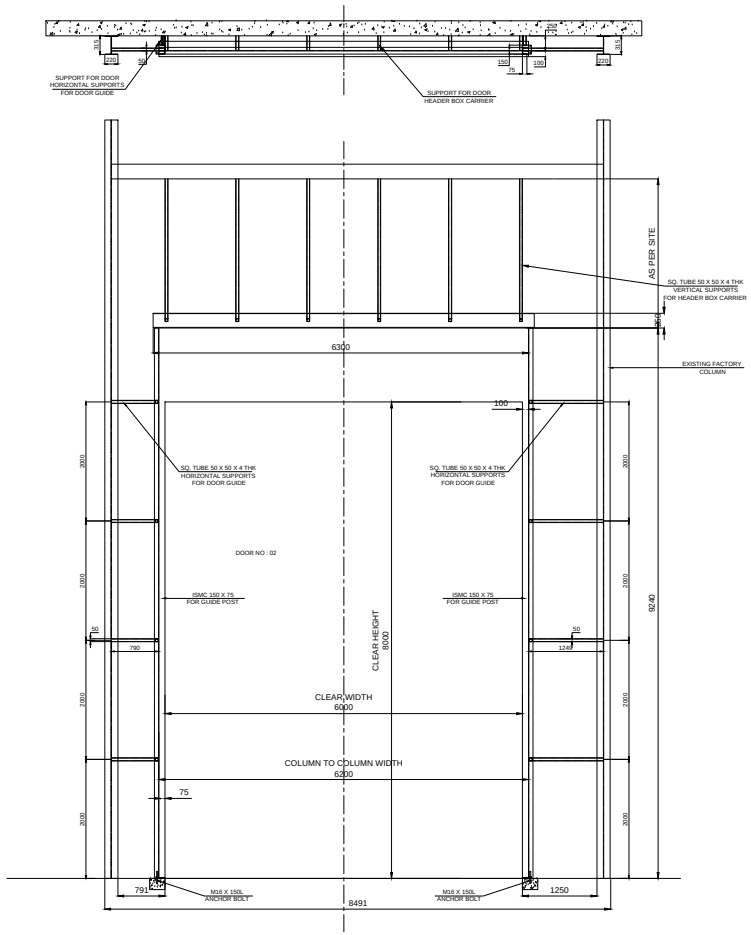

6000	8000	6200	9240
CLEAR WIDTH	CLEAR HEIGHT	TOTAL WIDTH	TOTAL HEIGHT

REV NO	REV DATE	DRAWN	REMARK
R01	01.06.19	P.V.A	1. NO. OF VERTICAL & HORIZONTAL SUPPORTS FOR HEADER BOX CARRIER INCREASES. 2. ALSO ADDING VERTICAL COLUMN SUPPORT.

This drawing & designing is the property of NIHVA TECHNOLOGIES. Not to be sold or copied to any other concern.

TITLE: STRUCTURE DRAWING

NIHVA TECHNOLOGIES PVT. LTD. PUNE
Tel : 020 66304033
Website:- www.nihva.com
Email:- info@nihva.com

	NAME	SIGN	DATE
DRAWN	P.A		31.05.19
CHECK	S.P		31.05.19
APPROVAL	V.T		31.05.19

If any queries contact : design@nihva.com

ALL DIMENSION ARE IN mm

CLIENT - LMWP

PROJECT - LMWP

SITE LOCATION - BANGALORE

DWG. NO. : NIHVA/19-20/0025/R01 REV.:- R01

SCALE: NTS WT: SHEET: 01 OF 01