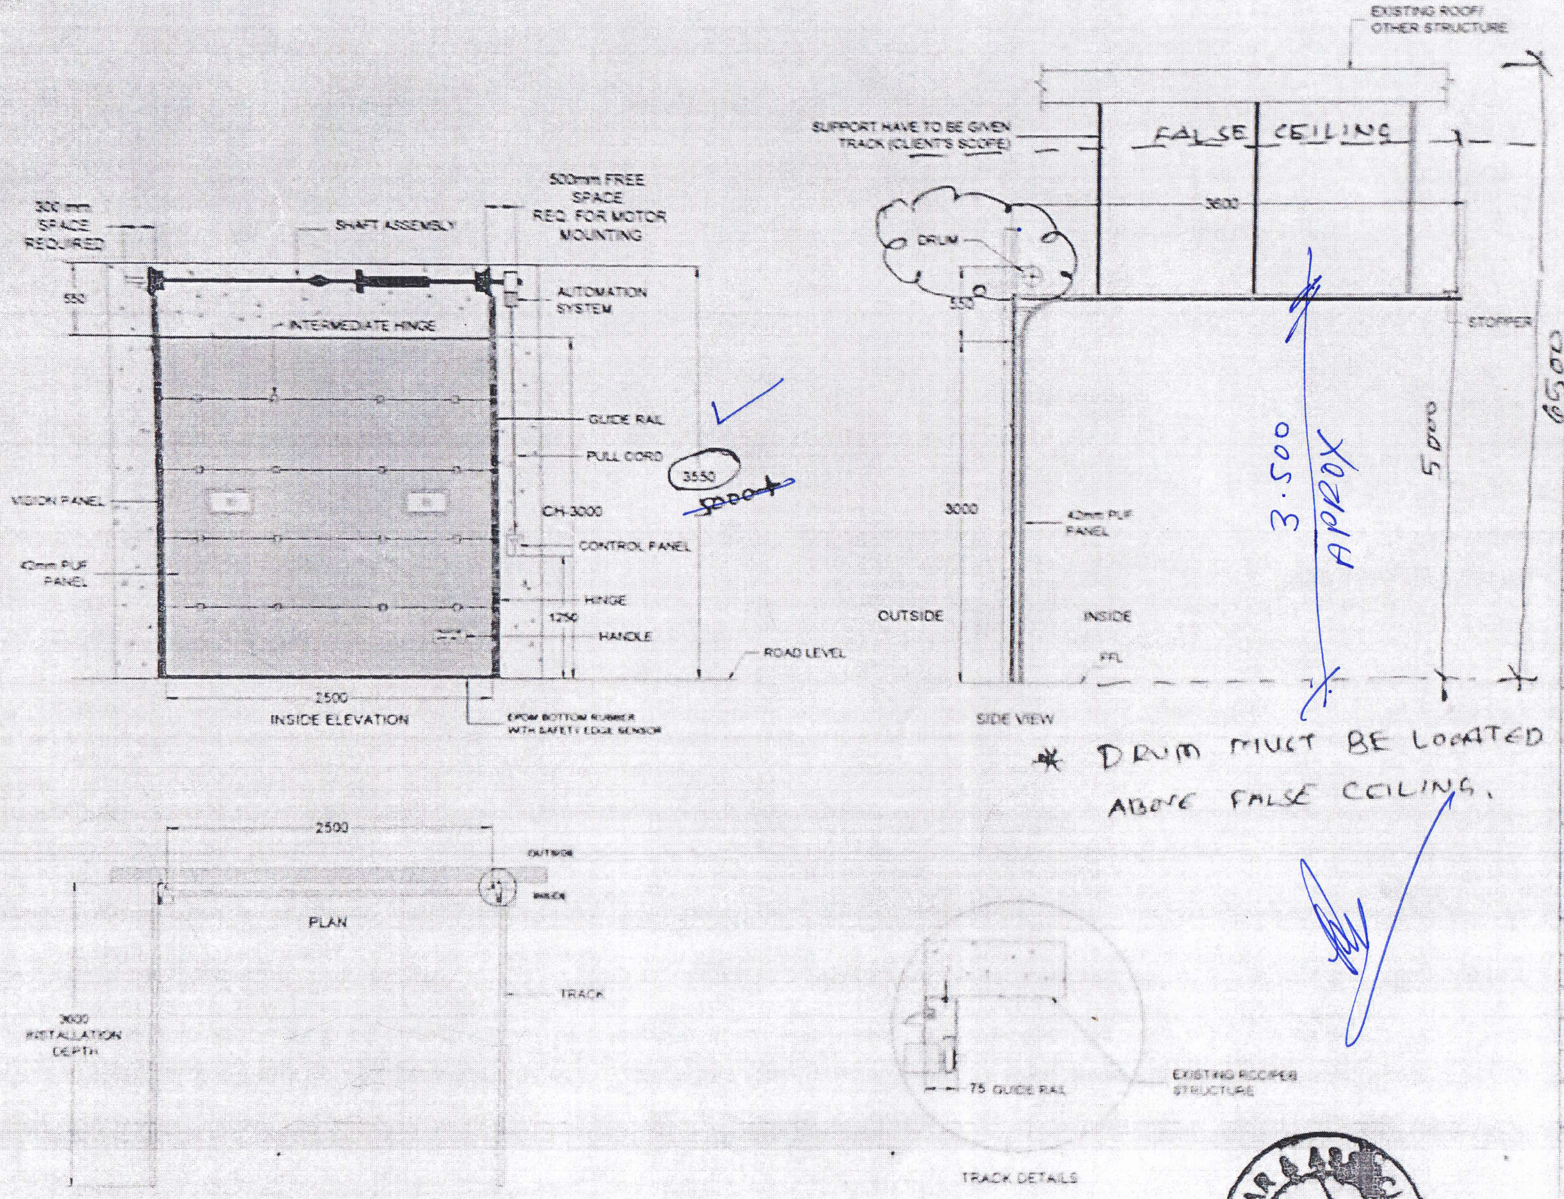

* DRUM MUST BE LOCATED ABOVE FALSE CEILING.

DANDEKAR & ASSOCIATES

Not Approved

DIMENSION :

CLEAR WIDTH	CLEAR HEIGHT	QUANTIT
2500 mm	3000 mm	4

TECHNICAL DATA :

COMPONENTS	MATERIALS	SPECIFICATIONS
DOOR PANELS	GI & PUF	42mm CFC-FREE POLYURETHANE WITH 0.5mm THK. GI PRECOATED PANELS
DOOR HINGE	———	HEAVY DUTY HINGES FOR INTERLOCKING OF PANELS
SHAFT ASSEMBLY	STD	TORSIONAL SPRING WITH SHAFT & BEARING PLATES
FINISH		PRECOATED / PRECOATED PANELS IN RAL 9002 GRAY WHITE

ACCESSORIES:
1. SAFETY EDGE SENSOR

IMPORTANT NOTES:

1. REQUIRED STRUCTURE FOR DOOR SHALL BE IN CLIENT'S SCOPE.
2. SINGLE PHASE POWER SUPPLY REQUIRED AT DOOR LOCATION.
3. ALL CIVIL WORK SHALL BE CLIENT'S SCOPE.

NIHVA
NIHVA Technologies Pvt. Ltd.

NIHVA TECHNOLOGIES
PVT. LTD. PUNE
Email - info@nihva.com
Website - www.nihva.com

TITLE:

SECTIONAL DOOR SL (MOTORIZED)

CLIENT'S APPROVAL :

CLIENT - PACK INNOVATION
PROJECT -
SITE LOCATION - CHAKAN, PUNE
DWG. NO. NIHVA/17-18/

SCALE: NTS	WT.	SHEET 1 OF 1
DRAWN BY: OMKAR		DATE: 24-08-2017
CHECK BY: SHEKHAR		DATE: 24-08-2017
APPROVED BY: SHEKHAR		DATE: 24-08-2017

If any queries contact : projects@nihva.com

NOTE: ALL DIMENSIONS ARE IN mm

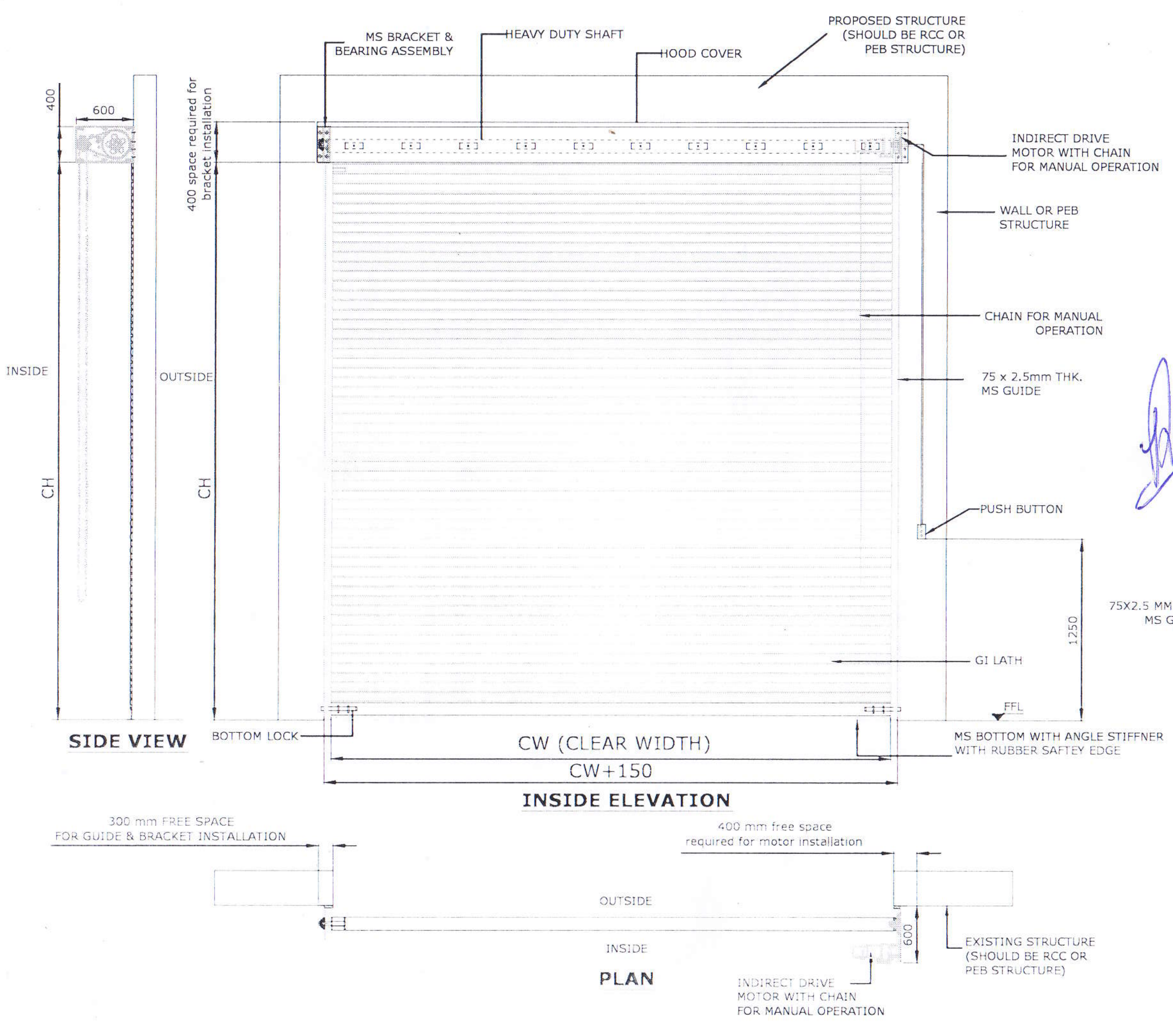
400
600
400 space required for bracket installation
INSIDE
OUTSIDE
CH
CH
MS BRACKET & BEARING ASSEMBLY
HEAVY DUTY SHAFT
HOOD COVER
PROPOSED STRUCTURE (SHOULD BE RCC OR PEB STRUCTURE)
INDIRECT DRIVE MOTOR WITH CHAIN FOR MANUAL OPERATION
WALL OR PEB STRUCTURE
CHAIN FOR MANUAL OPERATION
75 x 2.5mm THK. MS GUIDE
PUSH BUTTON
1250
GI LATH
FFL
BOTTOM LOCK
CW (CLEAR WIDTH)
CW+150
MS BOTTOM WITH ANGLE STIFFNER WITH RUBBER SAFTEY EDGE
300 mm FREE SPACE FOR GUIDE & BRACKET INSTALLATION
400 mm free space required for motor installation
OUTSIDE
INSIDE
600
EXISTING STRUCTURE (SHOULD BE RCC OR PEB STRUCTURE)
INDIRECT DRIVE MOTOR WITH CHAIN FOR MANUAL OPERATION

SIDE VIEW

INSIDE ELEVATION

PLAN

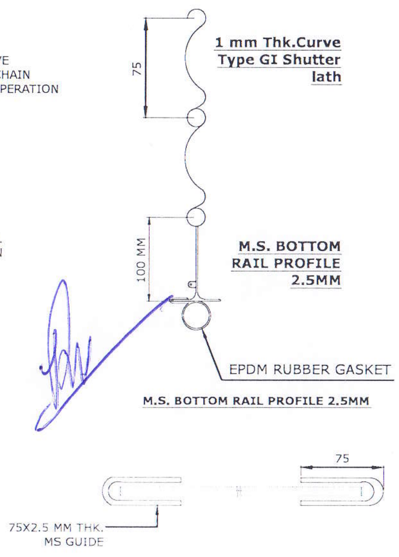

1 mm Thk.Curve Type GI Shutter lath

M.S. BOTTOM RAIL PROFILE 2.5MM

M.S. BOTTOM RAIL PROFILE 2.5MM

CLEAR WIDTH (CW)	CLEAR HEIGHT (CH)	QUANTITY
2500	2500	01 NOS

DIMENSION :

CLEAR WIDTH	CLEAR HEIGHT	QUANTITY
2500	2500	01 NOS

MATERIAL:

THICKNESS :

NOTE:
1.REQUIRED STRUCTURE FOR ROLLING SHUTTER WILL BE CLIENT'S SCOPE.
2.ONE COAT OF RED OXIDE PRIMER WILL BE GIVEN TO THE SHUTTER.
3.SINGLE PHASE. 3 CORE 1.5 SQ. CABLE REQUIRE AT SITE(CLIENT'S SCOPE)
4. FOR FINAL FINISH CLIENT SHOULD CONFIRM RAL COLOR SHADE.

NIHVA
NIHVA TECHNOLOGIES PVT. LTD.

NIHVA TECHNOLOGIES
PVT LTD PUNE
Email:- info@nihva.com
Website:- www.nihva.com

TITLE:
MOTORIZED ROLLING SHUTTER

CLIENT'S APPROVAL :

CLIENT - PACK INNOVATION
PROJECT -
SITE LOCATION - CHAKAN,PUNE
DWG. NO. : NIHVA/17-18/0175

SCALE: NTS	WT:	SHEET:1 OF 1
DRAWN BY: OMKAR	DATE: 24-08-2017	
CHECK BY : SHEKHAR	DATE: 24-08-2017	
APPROVED BY: SHEKHAR	DATE: 24-08-2017	

If any queries contact : projects@nihva.com

NOTE: ALL DIMENSIONS ARE IN mm

THIS DRAWING & DESIGN IS THE PROPERTY OF NIHVA TECHNOLOGIES. NOT TO BE SOLD OR COPIED TO ANY OTHER CONCERN.

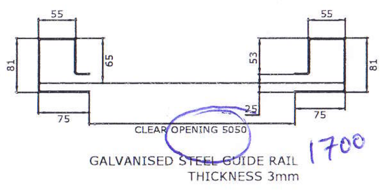

1700

GALVANISED STEEL GUIDE RAIL
THICKNESS 3mm

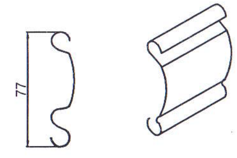

SHUTTER SLAT

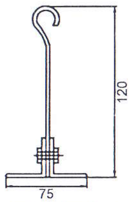

FIRE RATED BOTTOM BAR

SHUTTER TYPE	2HRS FIRE RATED SHUTTER
SHUTTER SLATS	1.0 mm GALVALUME STEEL SOLID SLATS
FINISHING OF SLATS	POWER COAT STANDARD RAL COLOUR
GUIDE RAIL	GALVANIZED ,3mm THICK
FINISHING OF GUIDE	POWDER COAT STANDARD RAL COLOUR
BOTTOM BAR	T-120
FINISHING OF B/BAR	POWDER COAT STANDARD RAL COLOUR
BOX DESIGN	MILD STEEL SECTION FRAME DESIGN
FINISHING OF BOX	POWDER COAT STANDARD RAL COLOUR
BOX COVER PLATE	0.8mm GALVANISED STEEL SHEET
FINISHING OF COVER	POWDER COAT STANDARD RAL COLOUR
OPERATION	MOTORIZE WITH MANUAL OVERRIDE CHAIN
MOTOR POWER SOURCE	230 VOLTS,1 PHASE,50HZ
FIRE MODE	THERMAL FUSIBLE LINK WILL AUTO CLOSE BY GRAVITY FORCE WHEN ROOM TEMP RISES UP TO 68°C FIRE SIGNAL FROM FIRE CONTROL ROOM AND SHUTTER SHALL CLOSE DOWN BY GRAVITY FORCE WITHOUT DELAY

LOCATION	SHUTTER NO.	CLEAR WIDTH (STRUCTURE)	CLEAR WIDTH (STRUCTURE)	QUANTITY	MOTOR POSITION
	FRS	1700 mm	3000 mm	1	RH

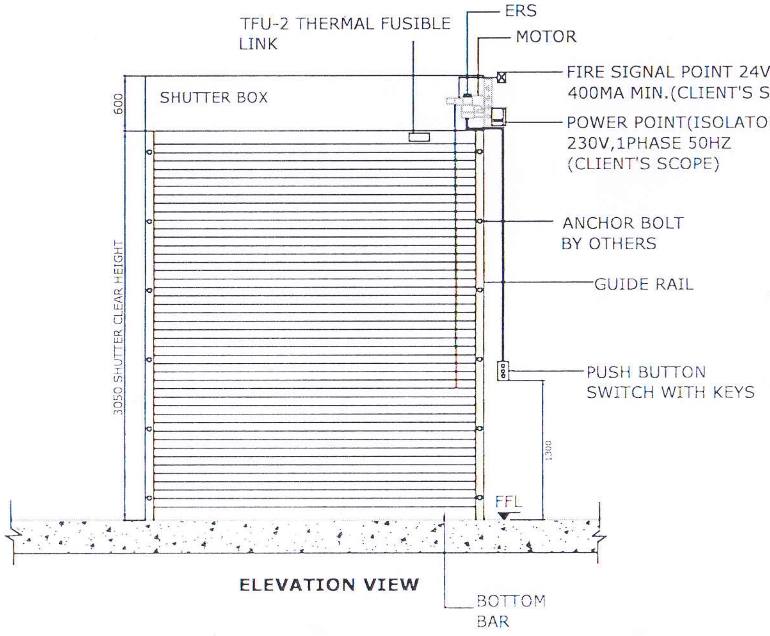
TFU-2 THERMAL FUSIBLE LINK
ERS
MOTOR
FIRE SIGNAL POINT 24VDC 400MA MIN.(CLIENT'S SCOPE)
POWER POINT(ISOLATOR) 230V,1PHASE 50HZ (CLIENT'S SCOPE)
SHUTTER BOX
600
ANCHOR BOLT BY OTHERS
GUIDE RAIL
3050 SHUTTER CLEAR HEIGHT
PUSH BUTTON SWITCH WITH KEYS
1300
FFL
BOTTOM BAR

ELEVATION VIEW

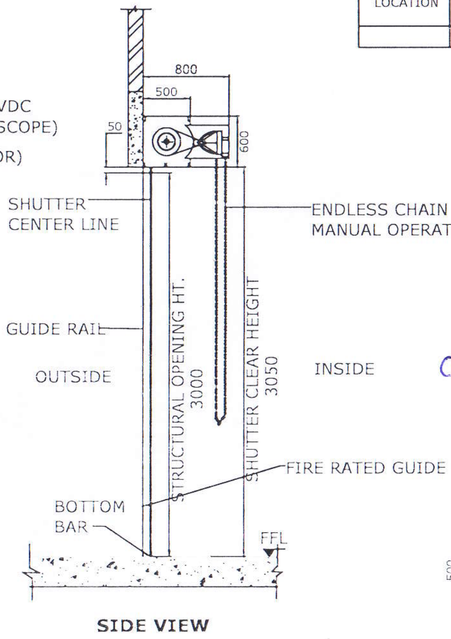

SIDE VIEW

CERTIFICATE REQUIRED

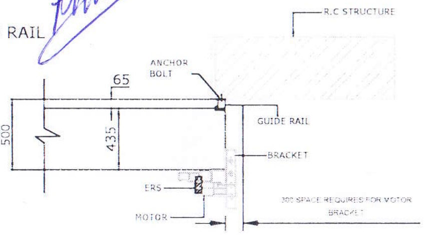

GUIDE & MOTOR ASSEMBLY DETAILS

NOTE- WIDTH & HEIGHT OF SHUTTER WILL BE 50mm
MORE THAN CLEAR WIDTH

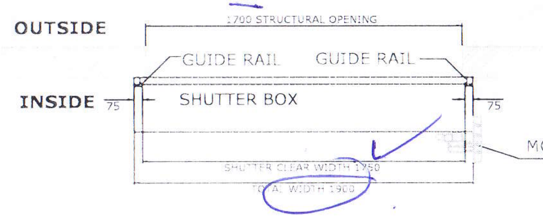

PLAN VIEW

This drawing & design is the property of NIHVA TECHNOLOGIES. Not to be sold or copied to any other concern.

TITLE	FIRE RATED ROLLING SHUTTER 1		NIHVA NIHVA TECHNOLOGIES PVT. LTD. NIHVA TECHNOLOGIES PVT. LTD. PUNE Tel : 020 66304033 Email:- info@nihva.com Website:- www.nihva.com
	SIGN	DATE	
DRAWN	OMKAR	24/08/17	CLIENT - PACK INNOVATIONS
CHECK	SHEKHAR	24/08/17	PROJECT -
REV			SITE - CHAKAN,PUNE
APPROVAL	SHEKHAR	24/08/17	DWG. NO. : NIHVA/17-18/0176
If any queries contact : projects@nihva.com			SCALE: NTS | WT: | SHEET: 01 OF 01
ALL DIMENSION ARE IN mm			

CLEAR WIDTH (CW)	CLEAR HEIGHT (CH)	QUANTITY
1700	3000	01 NOS

SHUTTER TYPE	2HRS FIRE RATED SHUTTER
SHUTTER SLATS	1.0 mm GALVALUME STEEL SOLID SLATS
FINISHING OF SLATS	POWER COAT STANDARD RAL COLOUR
GUIDE RAIL	GALVANIZED ,3mm THICK
FINISHING OF GUIDE	POWDER COAT STANDARD RAL COLOUR
BOTTOM BAR	T-120
FINISHING OF B/BAR	POWDER COAT STANDARD RAL COLOUR
BOX DESIGN	MILD STEEL SECTION FRAME DESIGN
FINISHING OF BOX	POWDER COAT STANDARD RAL COLOUR
BOX COVER PLATE	0.8mm GALVANISED STEEL SHEET
FINISHING OF COVER	POWDER COAT STANDARD RAL COLOUR
OPERATION	MOTORIZE WITH MANUAL OVERRIDE CHAIN
MOTOR POWER SOURCE	230 VOLTS,1 PHASE,50HZ
FIRE MODE	THERMAL FUSIBLE LINK WILL AUTO CLOSE BY GRAVITY FORCE WHEN ROOM TEMP RISES UP TO 68°C FIRE SIGNAL FROM FIRE CONTROL ROOM AND SHUTTER SHALL CLOSE DOWN BY GRAVITY FORCE WITHOUT DELAY

LOCATION	SHUTTER NO.	CLEAR WIDTH (STRUCTURE)	CLEAR WIDTH (STRUCTURE)	QUANTITY	MOTOR POSITION
	FRS	1700 mm	2500 mm	1	RH

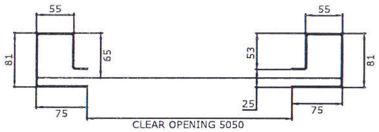

GALVANISED STEEL GUIDE RAIL
THICKNESS 3mm

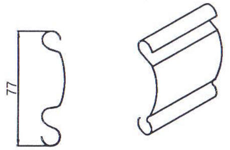

SHUTTER SLAT

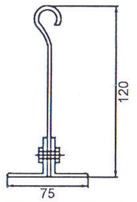

FIRE RATED BOTTOM BAR

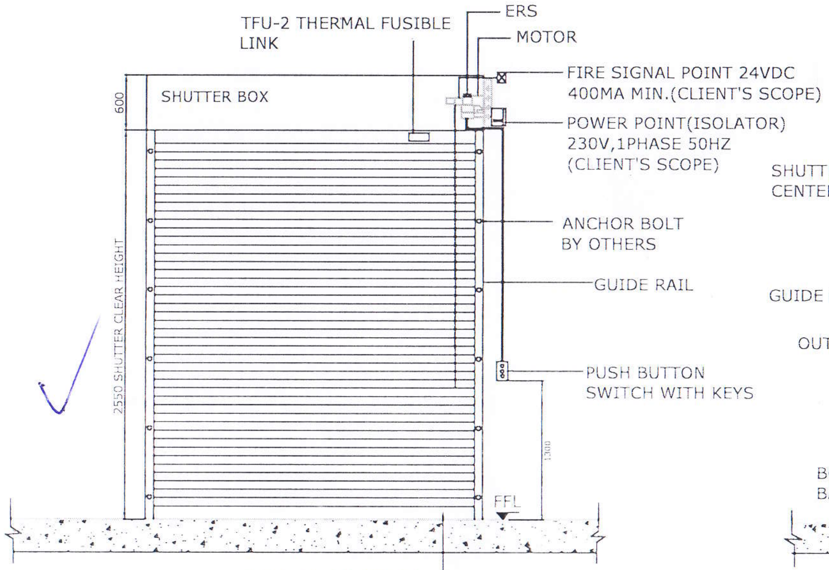
TFU-2 THERMAL FUSIBLE LINK
ERS
MOTOR
FIRE SIGNAL POINT 24VDC 400MA MIN.(CLIENT'S SCOPE)
POWER POINT(ISOLATOR) 230V,1PHASE 50HZ (CLIENT'S SCOPE)
SHUTTER BOX
600
ANCHOR BOLT BY OTHERS
GUIDE RAIL
PUSH BUTTON SWITCH WITH KEYS
2550 SHUTTER CLEAR HEIGHT
1300
FFL
BOTTOM BAR

ELEVATION VIEW

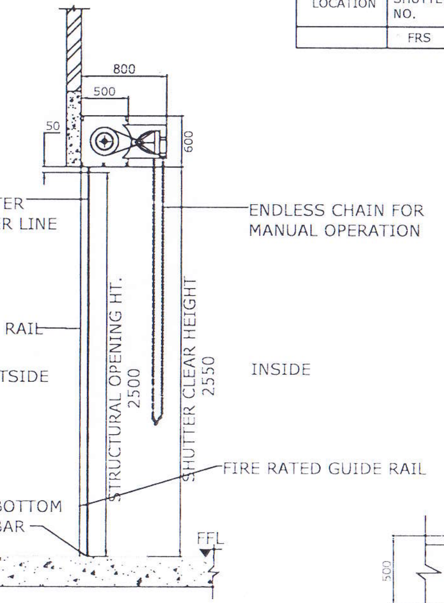

SIDE VIEW

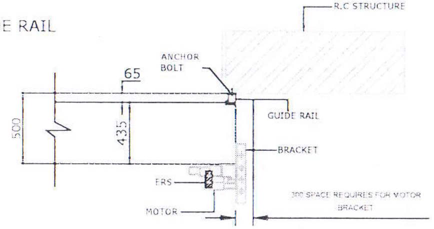

GUIDE & MOTOR ASSEMBLY DETAILS

NOTE- WIDTH & HEIGHT OF SHUTTER WILL BE 50mm
MORE THAN CLEAR WIDTH

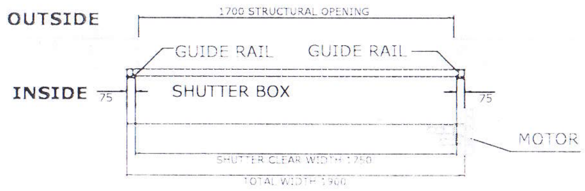

PLAN VIEW

This drawing & design is the property of NIHVA TECHNOLOGIES. Not to be sold or copied to any other concern.

TITLE	FIRE RATED ROLLING SHUTTER 2	
	SIGN	DATE
DRAWN	OMKAR	24/08/17
CHECK	SHEKHAR	24/08/17
REV.		
APPROVAL	SHEKHAR	24/08/17

If any queries contact : projects@nihva.com

ALL DIMENSIONS ARE IN mm

NIHVA
NIHVA TECHNOLOGIES PVT. LTD.

NIHVA TECHNOLOGIES
PVT. LTD. PUNE
Tel : 020 66304033
Email:- info@nihva.com
Website - www.nihva.com

CLIENT - PACK INNOVATIONS
PROJECT -
SITE - CHAKAN,PUNE
DWG. NO. : NIHVA/17-18/0183
SCALE: NTS | WT: | SHEET: 01 OF 01

CLEAR WIDTH (CW)	CLEAR HEIGHT (CH)	QUANTITY
1700	2500	01 NOS