

ROOF LAYOUT _1

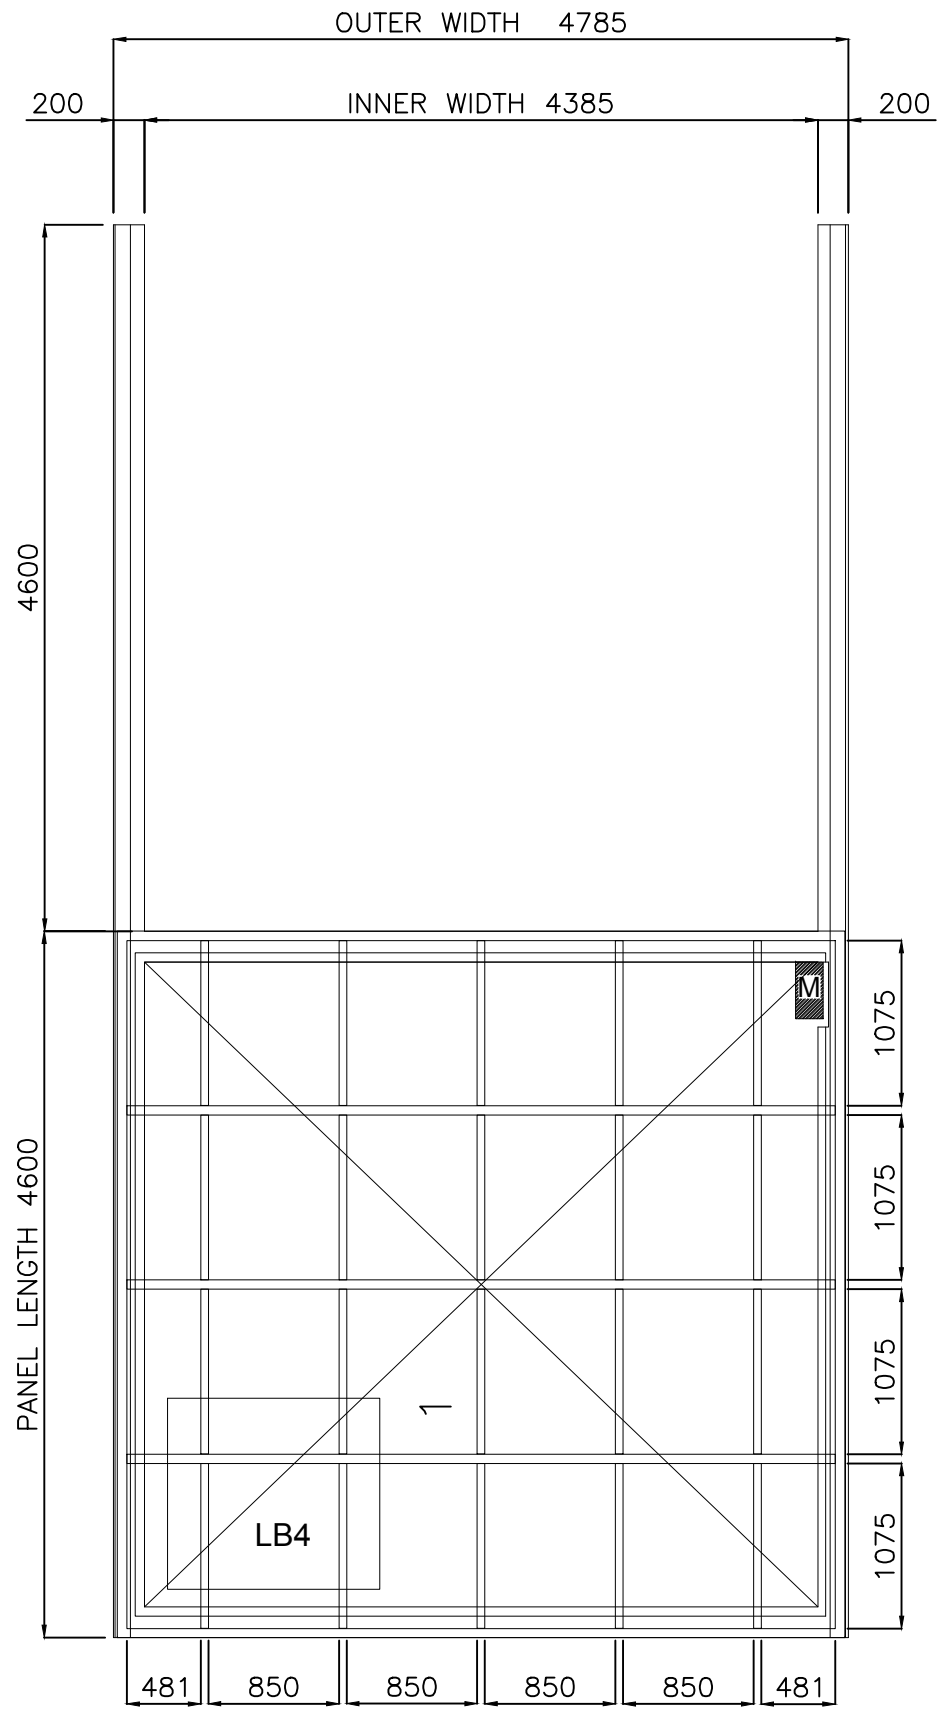

PLAN

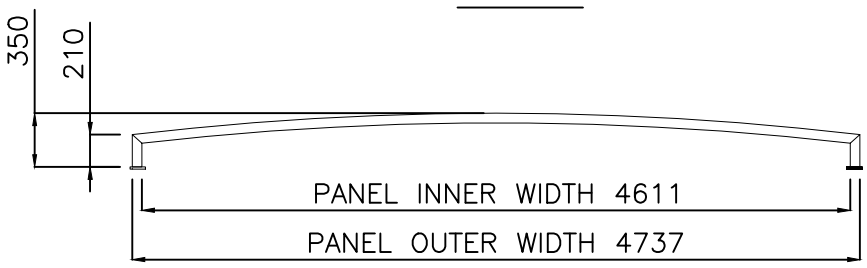

SECTION VIEW

1. BENDING PROFILE SIZE - 60X63X3MM
2. INTERMEDIATE SUPPORT TUBE - 50X50X3MM
3. WHEEL MOUNTING PROFILE SIZE -63X107X3MM
4. TRACK SIZE -100W X 3MM

This drawing & design is the property of NIHVA TECHNOLOGIES. Not to be sold or copied to any other concern.

TITLE	ROOF LAYOUT_1			NIHVA TECHNOLOGIES PVT. LTD.	
	NAME	SIGN	DATE		
DRAWN	D.V.		17.03.23	CLIENT -MAXIMA	
CHECK	P.M.		17.03.23	LOCATION - MUMBAI_IN	
APPRD.	V.T.		17.03.23	PRODUCT - RETRACTABLE ROOF	
If any queries contact : supportautomation@nihva.com				NIHVA\22-23\02XX	REV- 4
ALL DIMENSION ARE IN mm				SCALE: NTS	SHEET: 01 OF 01