
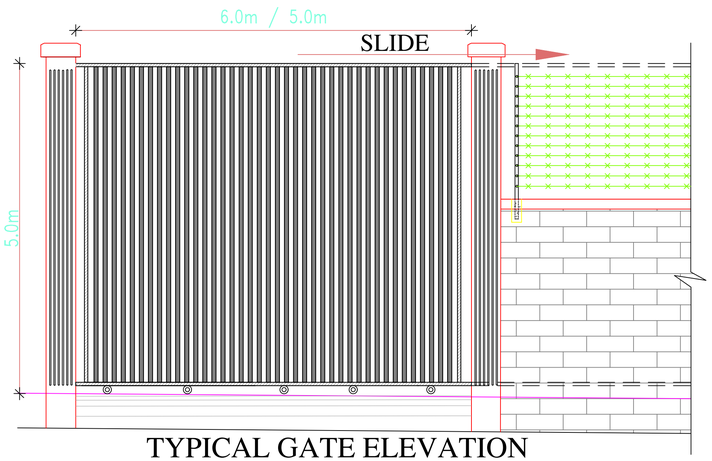


TYPICAL GATE ELEVATION

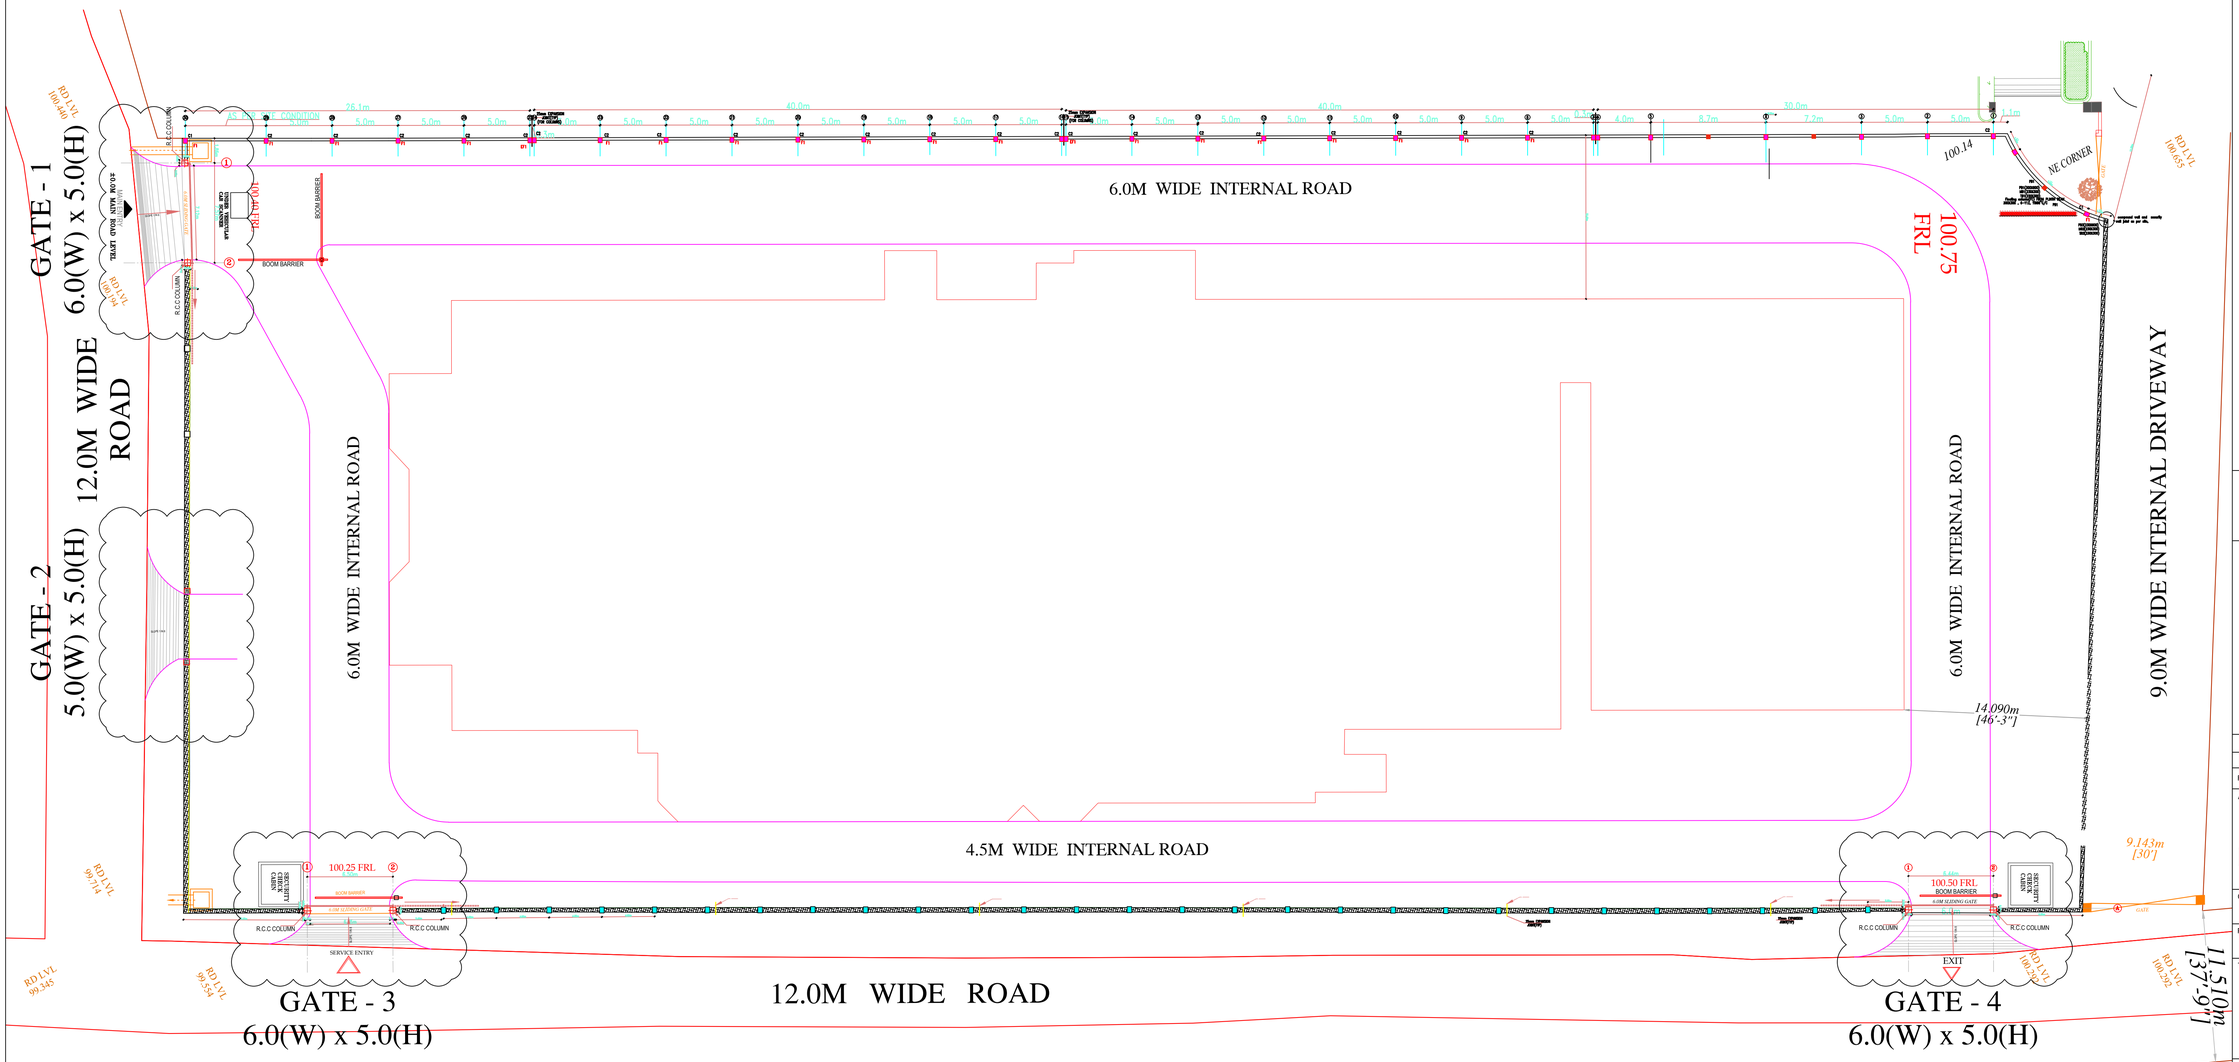

NOTE:

THE DRAWING IS THE COPYRIGHT OF SYSPLAN CONSULTANTS PVT. LTD. AND NO UNAUTHORIZED USE OR REPRODUCTION IS PERMITTED WITHOUT THE ARCHITECTS PRIOR AUTHORIZATION.

THIS DRAWING IS NOT TO BE SCALED.

ALL DIMENSIONS ARE IN MILLIMETERS UNLESS OTHERWISE INDICATED.

ALL LEVELS ARE IN METERS UNLESS OTHERWISE INDICATED.

ANY DISCREPANCY IN THE DRAWING IS TO BE BROUGHT TO THE IMMEDIATE NOTICE OF THE ARCHITECT.

THIS DRAWING IS TO BE READ IN CONJUNCTION WITH OTHER RELEVANT ARCHITECTURAL, STRUCTURAL, MECHANICAL, ELECTRICAL AND PLUMBING DRAWINGS AND ALL RELEVANT SECTIONS OF SPECIFICATION.

LEGEND:

BRICK PILLAR

R.C.C PILLAR

FINISHED GROUND LEVEL(FGL)
FININSHED ROAD LEVEL (FRL)

Rev.	Date	Description

REVISION HISTORY:

ARCHITECTS & STRUCTURAL CONSULTANTS:

SYSPLAN CONSULTANTS PVT/LTD
HYDERGUDA , HYDERABAD
PH.NO.23222695
Email: sysplan2002@gmail.com

CLIENT:
KALA JYOTHI PROCESS PVT. LTD.

PROJECT NAME:
KALA JYOTHI DATA CENTER

TITLE:
SITE PLAN & TYP. ELEVATION

Checked By:	Checked Date:	Drawn By:	Drawn Date:
MADHAVI	07.04.22	RAKESH	07.04.22
Approved By:	Approved Date:	Drawing No:	
TSS REDDY	07.04.22		
JOB NO.	Discipline:	Scale:	Revision:
SYS-21-22/07	ARCH	1 : 75	R0

GOOD FOR CONSTRUCTION