

THIS PRINT IS THE PROPERTY OF NIHVA IT IS TO BE USED ONLY FOR THE PURPOSE FOR WHICH IT WAS LENT AND MUST NOT BE USED IN ANY WAY DERTIMENTAL TO THE INTEREST OF THIS COMPANY AND IS SUBJECT TO RETURN ON DEMAND.

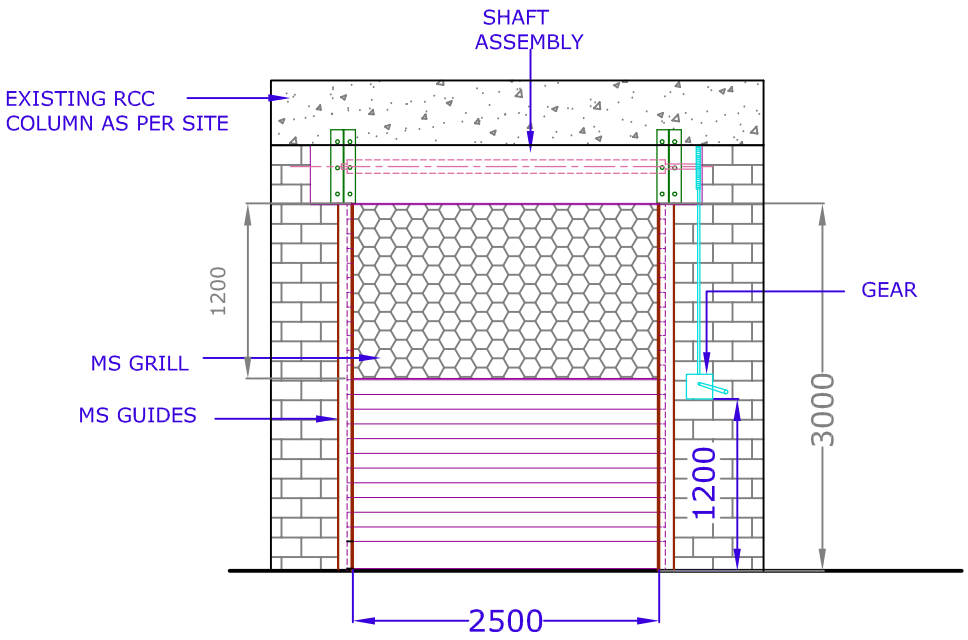


INSIDE ELEVATION


Clear opening size:-(w)2.5mx(h)3.0m.

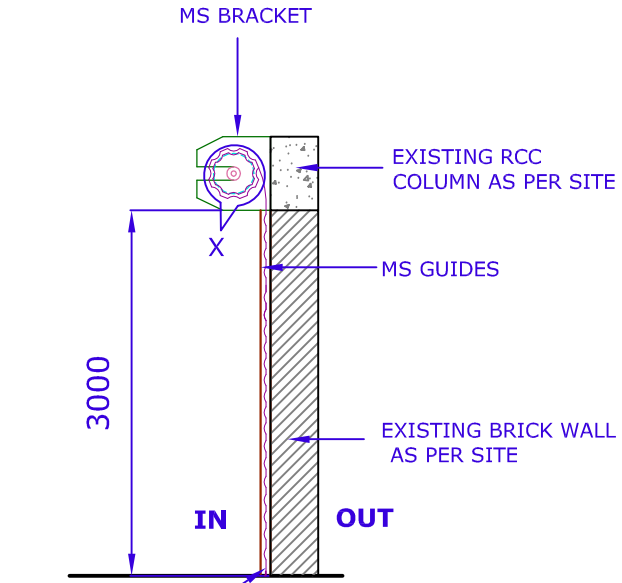

SIDE VIEW

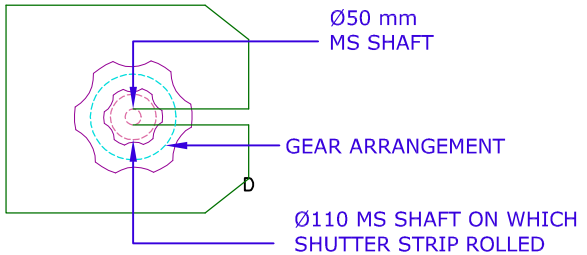

Bracket

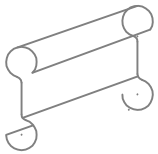

Box profile

TITLE: ROLLING SHUTTER (GEAR OPERATED)	DO NOT SCALE DRAWING	SIGN	DATE	NIHVA TECHNOLOGIES PVT. LTD. Pune:-411044 Tel :- 020 66304033 Email :- info@nihva.com
CLIENTS APPROVEL:-	DRAWN			CLIENT:
	CHECK			PROJECT / SITE:
	ENG			PRODUCT NAME:
	APPRD.			DWG. NO.:
All DIMENSION ARE IN M.M.	PROD			REV.: 0
If any queries CONTACT: projects@nihva.com	MFG			SCALE: NTS WT: SHEET: 1 OF 1
	Ref. No.			