
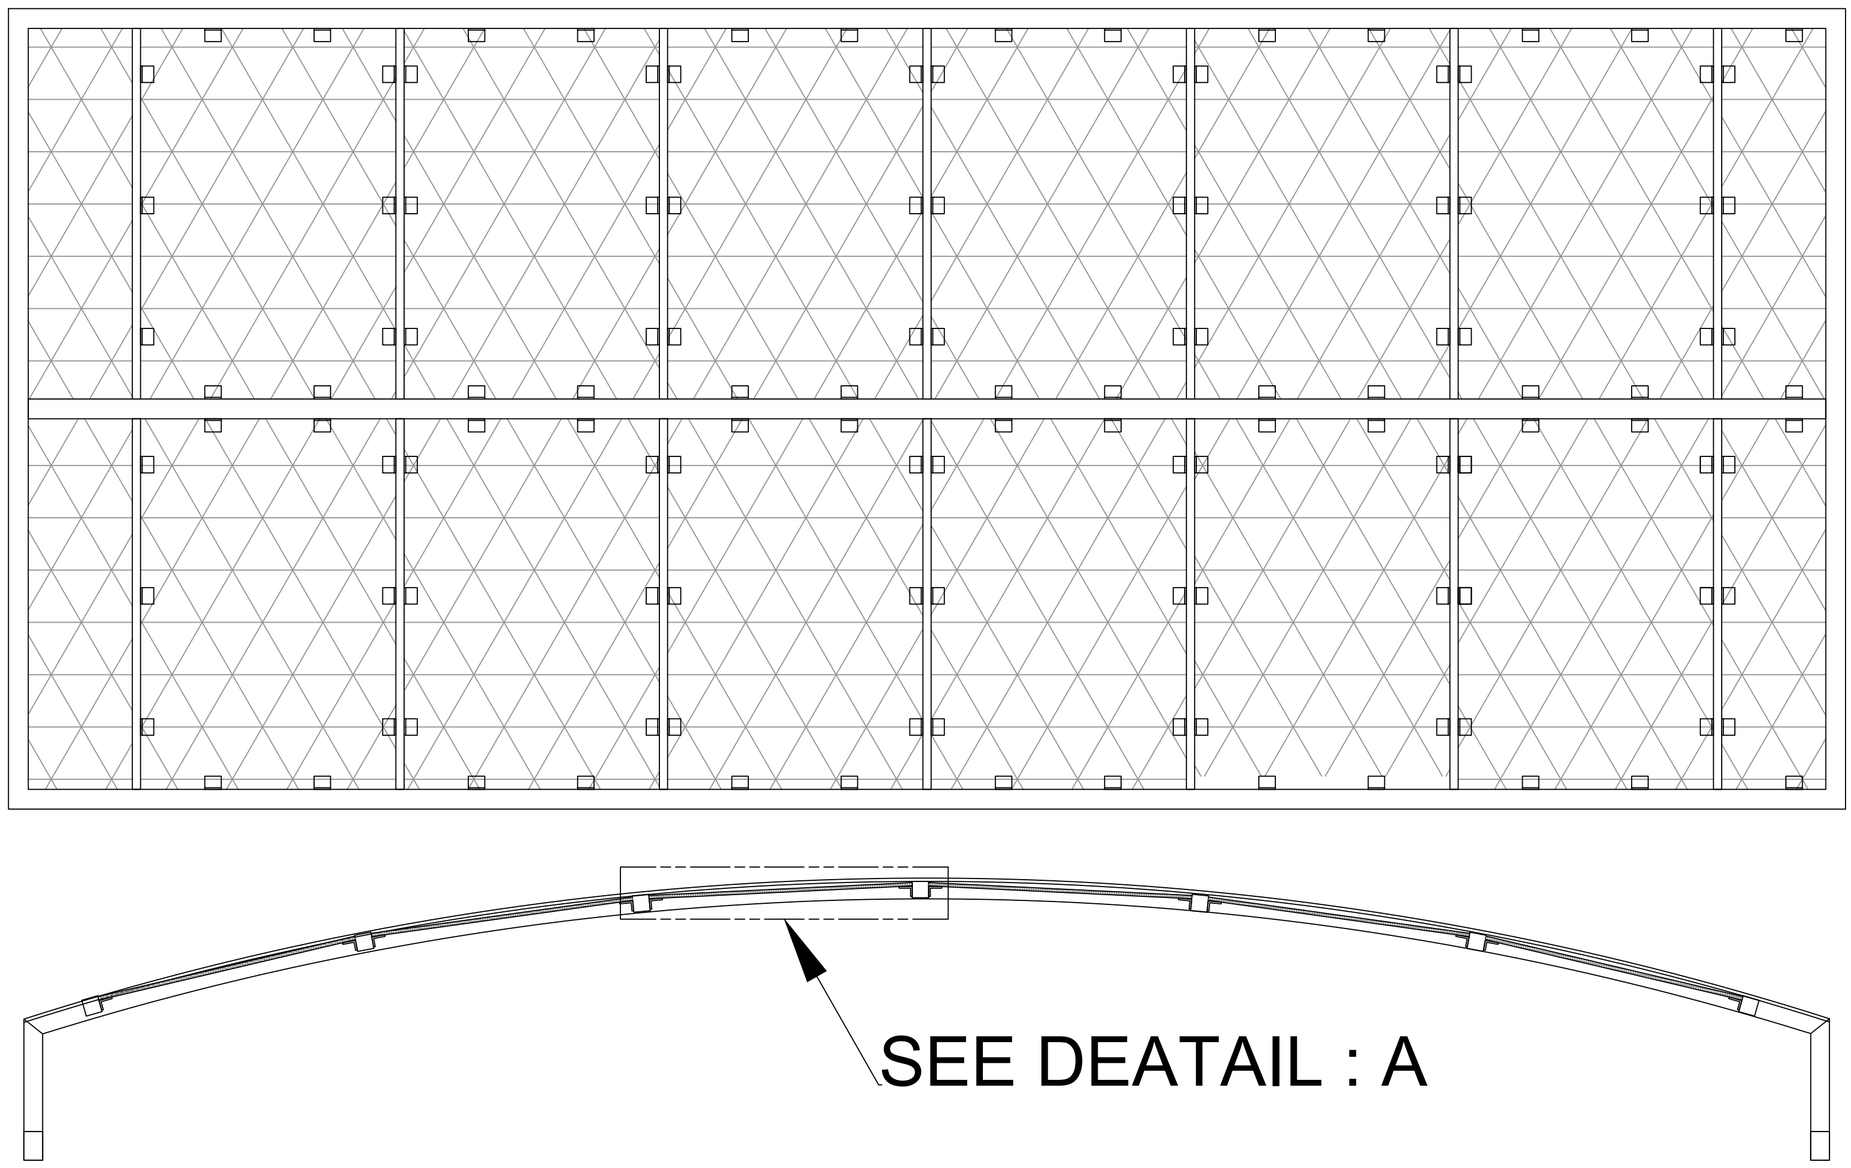


SECTION VIEW

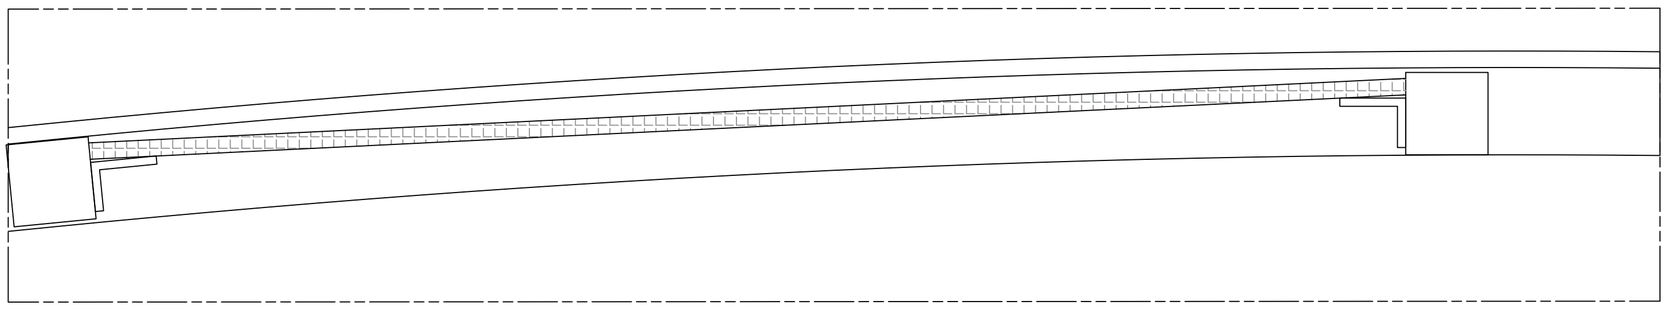

DEATAIL VIEW : A

1. FITTING OF PANEL - NIHVA SCOPE
2. ALL DIMENSION IN MM.
3. ALL WOODEN ROOF PANELS ARE IN CLIENT SCOPE
4. PANEL WOULD BE MAKE PER DIMENSIONS PROVIDED BY NIHVA.
5. DRAWING IS PROVIDED FOR REFERANCE PURPOSE & SINGLE PANEL ONLY.

This drawing & design is the property of NIHVA TECHNOLOGIES. Not to be sold or copied to any other concern.

TITLE

WOODEN ROOF PANEL LAYOUT

NIHVA TECHNOLOGIES PVT. LTD.

	NAME	SIGN	DATE
DRAWN	MAHESH S.		30.11.22
CHECK	MAHESH S.		30.11.22
APPRD.	VIJAY T.		30.11.22

If any queries contact : projectsautomation@nihva.com

CLIENT - MR. MANISH SHAHA

LOCATION - AHMEDABAD_IN

PRODUCT - RETRACTABLE ROOF

NIHVA\22-23\02XX | REV- 0

ALL DIMENSION ARE IN mm | SCALE: NTS | SHEET: 01 OF 01