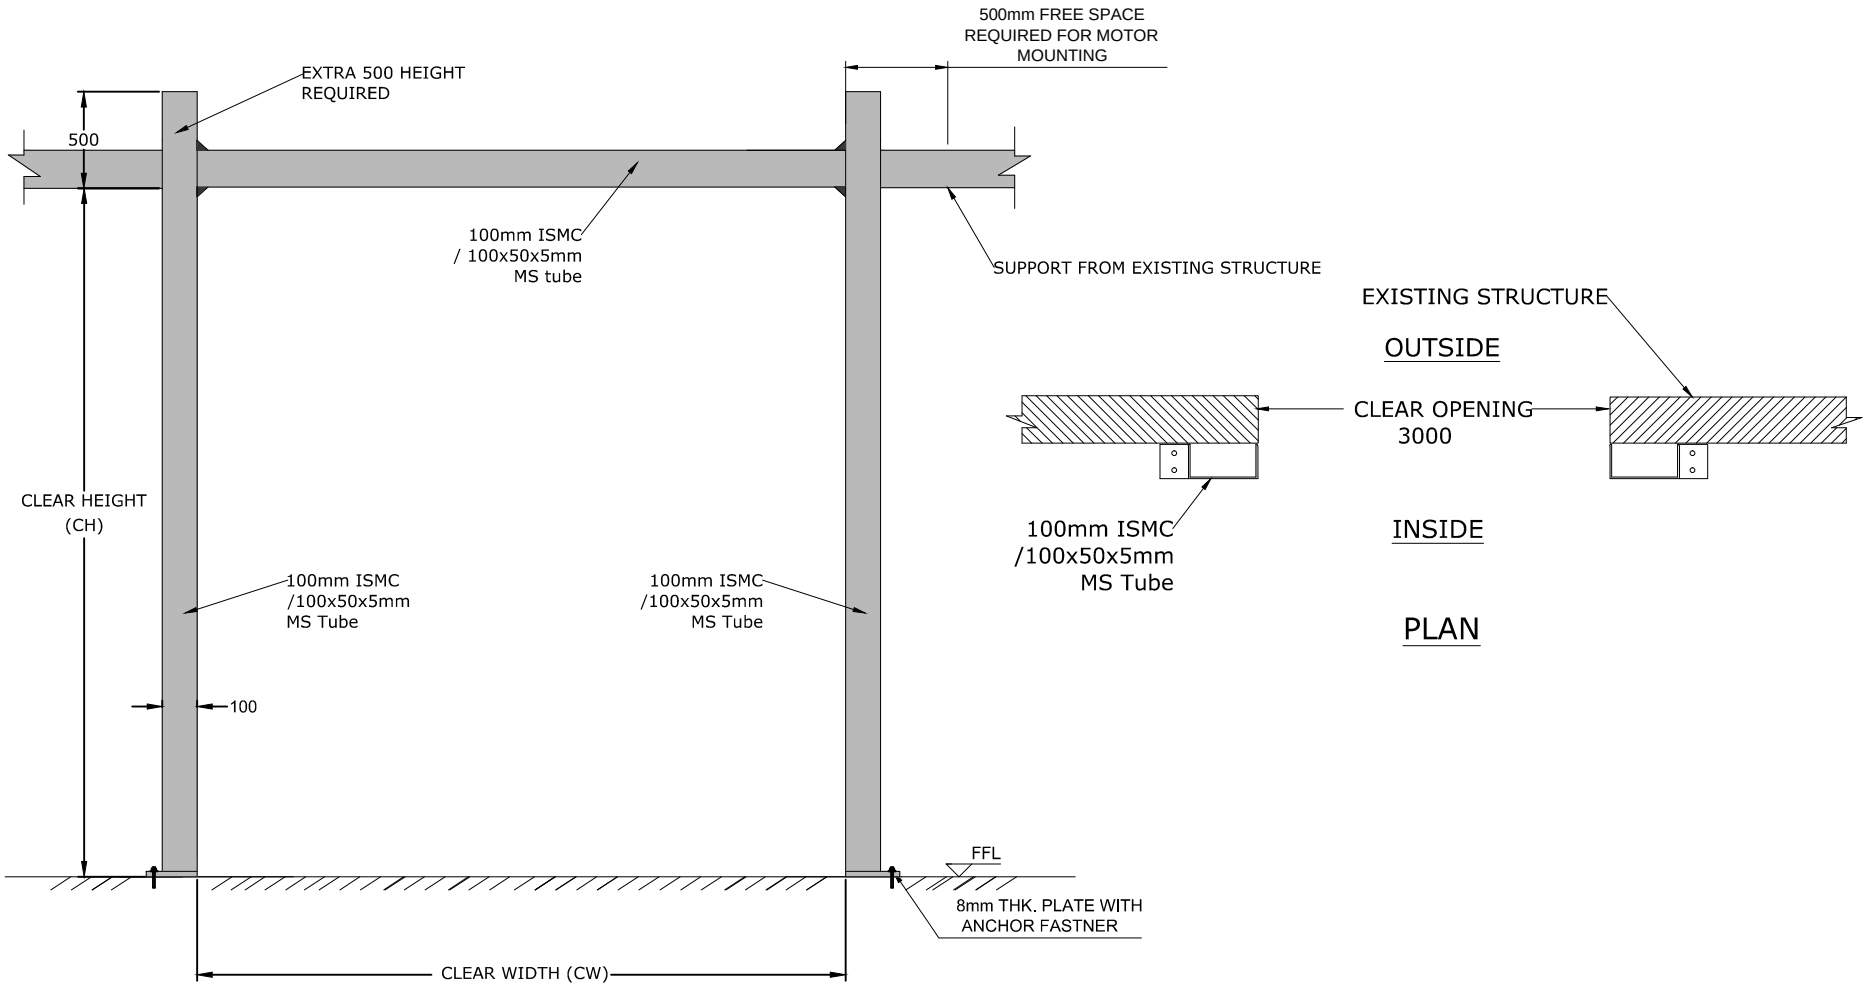


CLEAR WIDTH (CW)	CLEAR HEIGHT (CH)
3000	3500
3000	3000
2000	3000
2450	3500
2500	3500

TITLE

STRUCTURE FOR HIGH SPEED DOOR (RR 300+ ALU)

CLIENT APPROVAL

This drawing & design is the property of NIHVA TECHNOLOGIES. Not be sold or copy to any other concern.

ALL DIMENSION ARE IN mm

	SIGN	DATE
DRAWN	OMKAR	22/09/17
CHECK	OMKAR.	22/09/17
ENG		
APPRD.	SHEKHAR.	22/09/17
MFG		
Ref. No.		

NIHVA TECHNOLOGIES PVT. LTD.
NIHVA TECHNOLOGIES PVT. LTD. PUNE
Tel : 020 66304033
Email:- info@nihva.com
Website:- www.nihva.com

CLIENT - FERRERO INDIA PVT. LTD

PROJECT-

SITE - BARAMATI.

DWG. NO. - NIHVA/17-18/0210

SCALE: NTS | WT: | SHEET: 01

If any queries contact : projects@nihva.com