



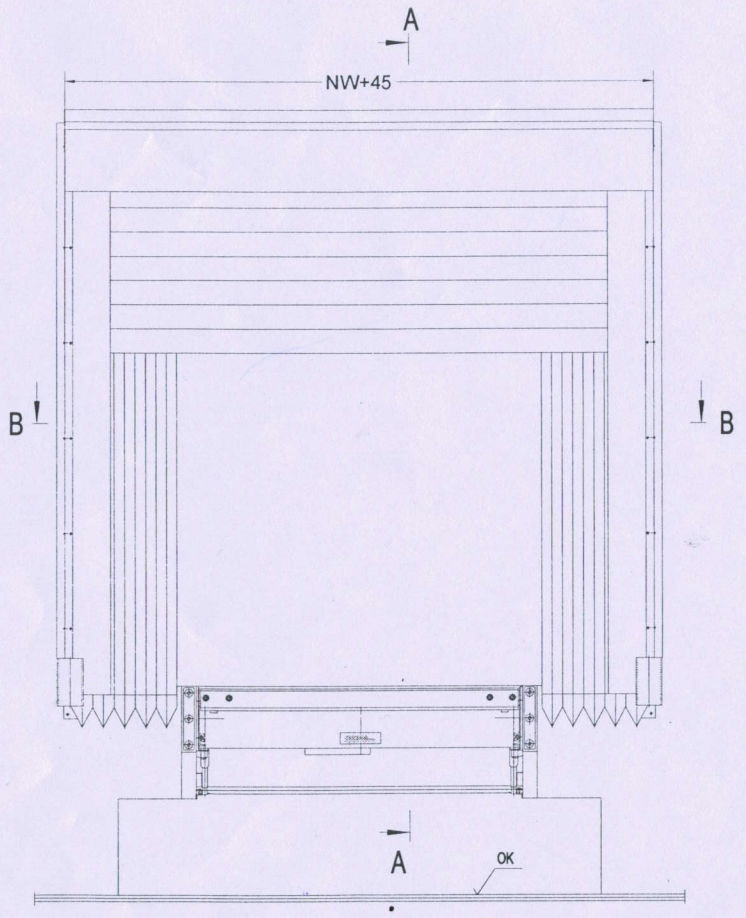


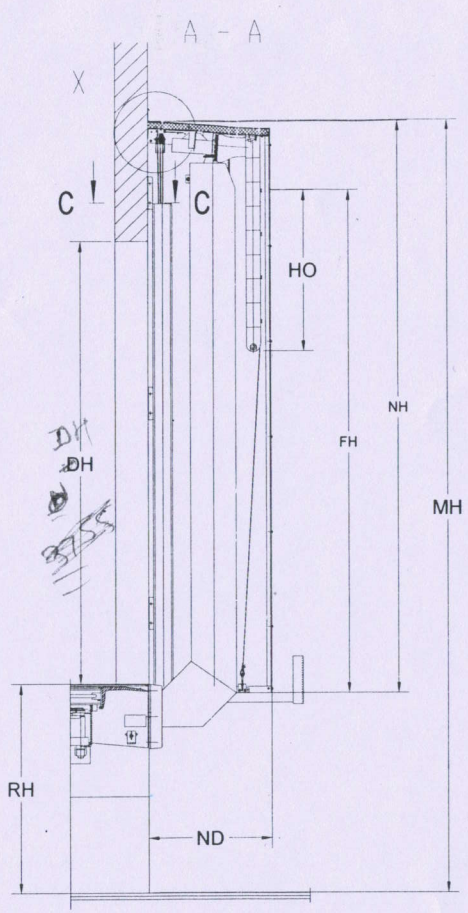

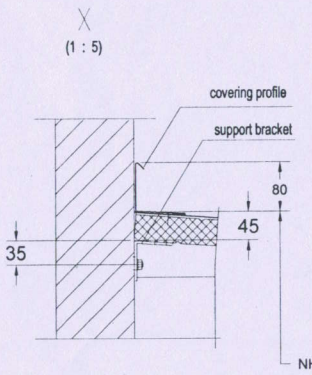

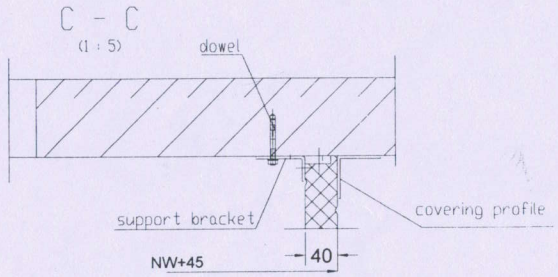

B - B

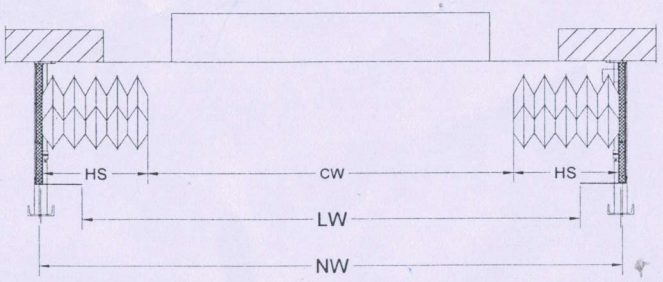

NOTE-
1.SELECTED DOCK SHELTER IS ONLY FOR 20/40 FT.CONTAINER.
2.ALL CIVIL WORK & M.S STRUCTURE IS IN CLINT SCOPE.

SR. NO.	LOCATION	SIZE	QTY.
3	OLD WAREHOUSE	3600 x 3600	02
2	TIK TAK WAREHOUSE	3600 x 3600	02
1	NEW WAREHOUSE	3600 x 3600	16

INFLATABLE DOCK SHELTER

Abb.	Dimension	Value(mm)
NW	Nominal width	3600
NH	Nominal height	3755
HS	Side bag extension	650
FH	Free height above level	3300
HO	Top bag extension	1000
ND	Nominal depth	770
MH	Installation height	VEHICLE HT + 500
LW	Clear width(max)	3000
CW	Clear width(min)	2300

Drawing approved based on physical verification

This drawing & designing is the property of NIHVA TECHNOLOGIES. Not to be sold or copied to any other concern.

TITLE
DOCK SHELTER

	SIGN	DATE
DRAWN	A.K	15.01.19
CHECK	P.A	15.01.19
REV.		
APPROVAL		

If any queries contact : projects@nihva.com

ALL DIMENSION ARE IN mm

NIHVA
NIHVA TECHNOLOGIES PVT. LTD.

NIHVA TECHNOLOGIES PVT. LTD. PUNE
Tel : 020 66304033
Email:- info@nihva.com
Website:- www.nihva.com

CLIENT - FERRERO
PROJECT -
SITE - BARAMATI
DWG. NO. : NIHVA/18-19/0239/R01 | REV :- R01
SCALE: NTS | WT: | SHEET: 01 OF 01

REV NO	DRAWN	DATE	REMARK
R01	A.K	24.01.19	LOCATION ADD