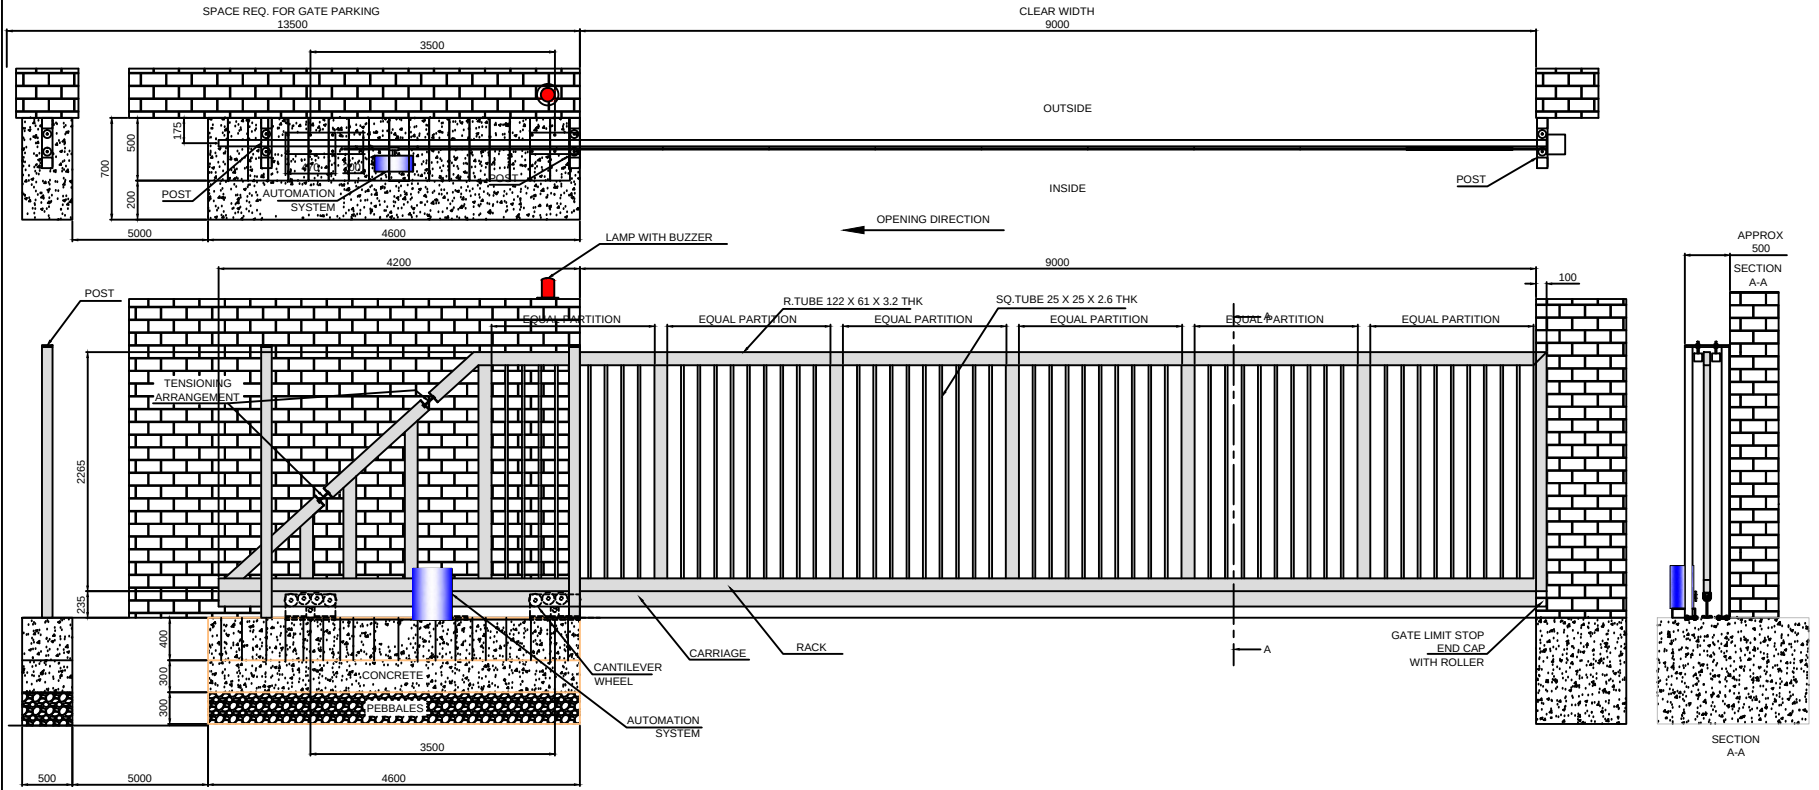


REV NO	DATE	DRAWN	REMARK
R03	03.03.2020	P.A	1. EQUAL PARTITION ADDED
R02	05.02.2020	P.A	1. FOUNDATION DETAILS ADD
R01	07.01.2020	P.A	1. SIZE & DESIGN CHANGE

TOLERANCE - ±10mm

NOTE-
1. ALL REQUIRED CIVIL WORK WILL BE IN CLIENTS SCOPE.
2. ONE COAT OF RED OXIDE & TWO COAT OF APPROVED RAL 9010 (PURE WHITE) SHADE WILL BE GIVEN TO THE GATE.
3. GATE LEAF WILL BE IN TWO/THREE PARTS FOR TRANSPORTATION & WILL BE WELD TOGETHER ON SITE.

QTY : 1 NO

This drawing & design is the property of NIHVA TECHNOLOGIES. Not to be sold or copied to any other concern.

TITLE
AUTOMATIC CANTILEVER GATE

	NAME	SIGN	DATE
DRAWN	P.A		18.12.2019
CHECK	G.J		18.12.2019
APPRD.			

NIHVA TECHNOLOGIES PVT. LTD.
NIHVA TECHNOLOGIES PVT. LTD. PUNE
Tel : 020 66304033
Email:- info@nihva.com
Website:- www.nihva.com

CLIENT - SCON
PROJECT - INNOVATEC
SITE LOCATION - SANAND

If any queries contact : design@nihva.com
DWG. NO. : NIHVA/19-20/0176/R03
REV- R03
ALL DIMENSION ARE IN mm
SCALE: NTS
WT:
SHEET: 01 OF 01