


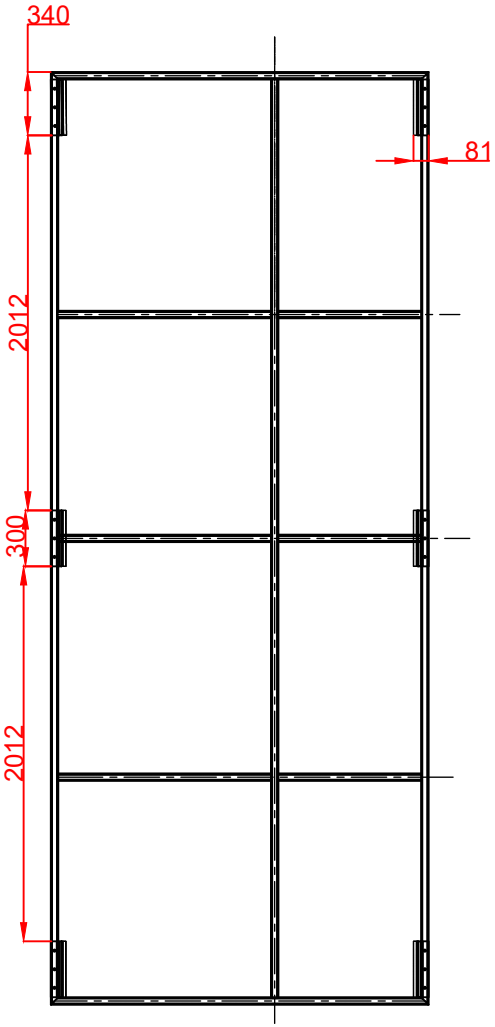


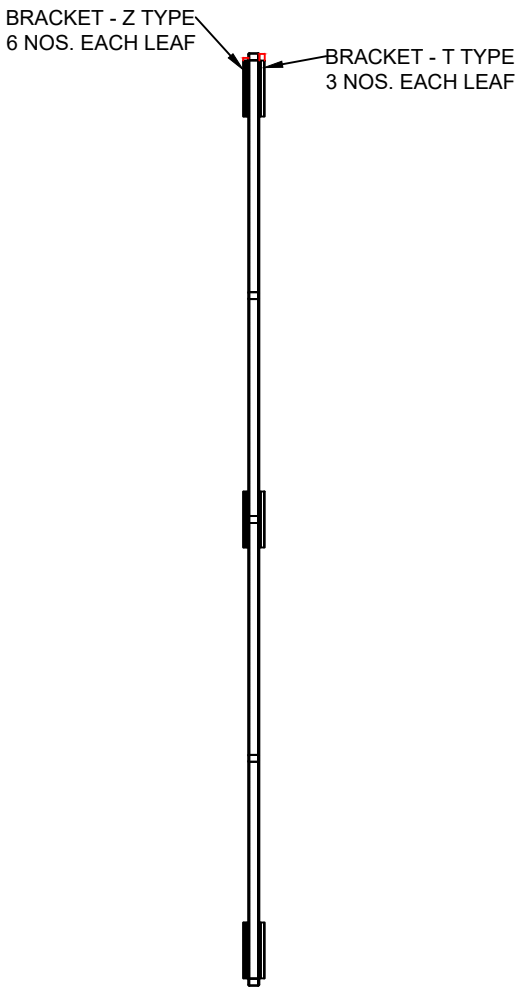

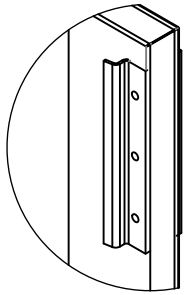

BRACKET - Z TYPE

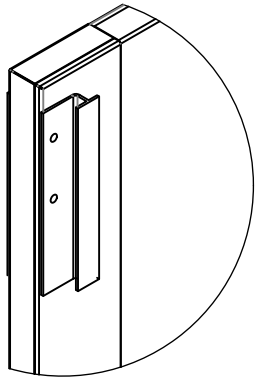

BRACKET - T TYPE

LEAF QTY. 4 Nos.

This drawing & design is the property of NIHVA TECHNOLOGIES. Not to be sold or copied to any other concern.

TITLE:- 4 LEAF RIGHT SIDE CRM DOOR 01				NIHVA TECHNOLOGIES PVT. LTD. PUNE Tel : 020 66304033 Email:- info@nihva.com Website:- www.nihva.com
	NAME	DATE	SIGN	
DRAWN	M.SUTAR	02/05/2022		CLIENT - LESTECH
CHECK	M.SUTAR	02/05/2022		LOCATION - POSCO MANGAON
APPRD.	V.TARAK	02/05/2022		PRODUCT - SLIDING DOOR
If any queries contact : design@nihva.com				DWG NO:-NIHVA/22-23/CLT/0014 REV- 0
ALL DIMENSION ARE IN mm				SCALE: NTS SCALE:-- 1:1 SHEET: 01 OF 01

Rev No.	Revision	Date	Revised By