


DRAWING

REV DESCRIPTION	DATE	REV NO
	18-05-2026	REV 00
1.		

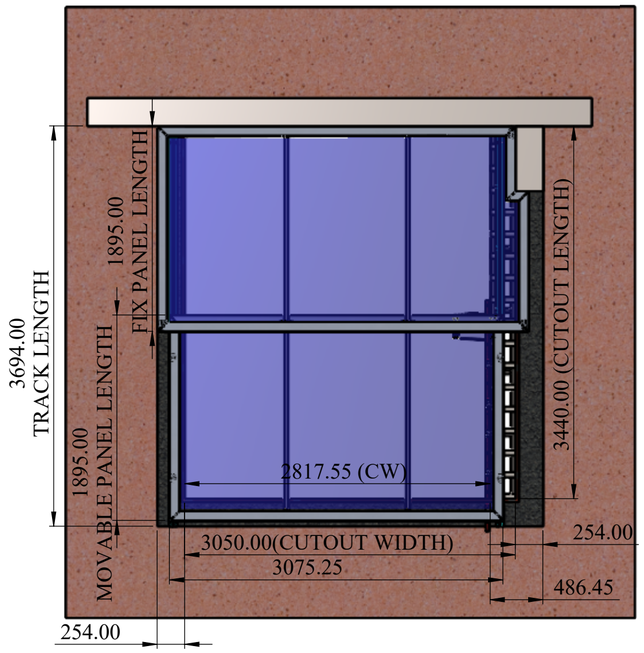

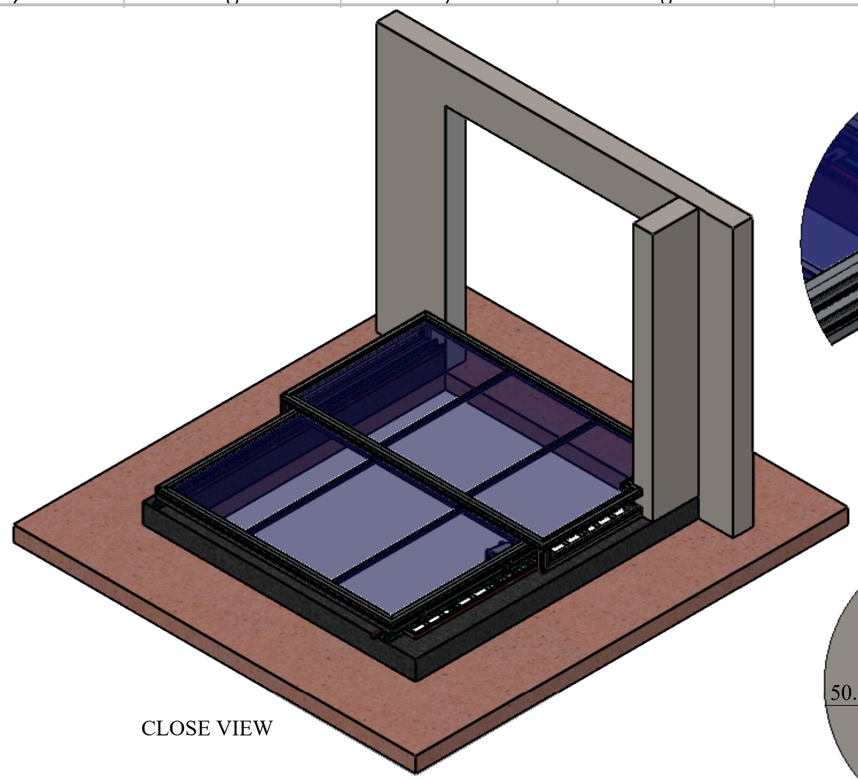


CLOSE VIEW

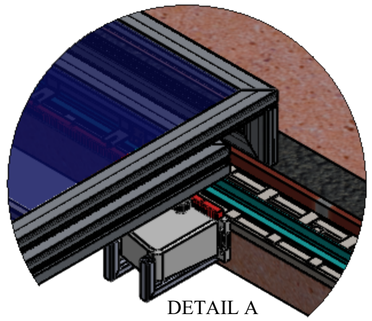


DETAIL A
SCALE 1 : 15


MOTOR MOUNTING

DETAIL B
SCALE 1 : 8

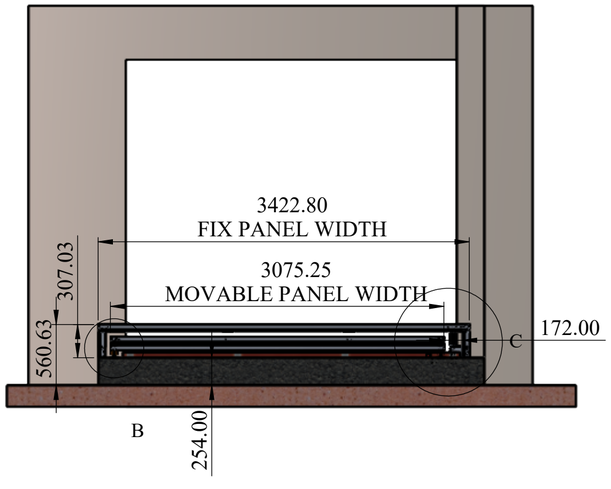

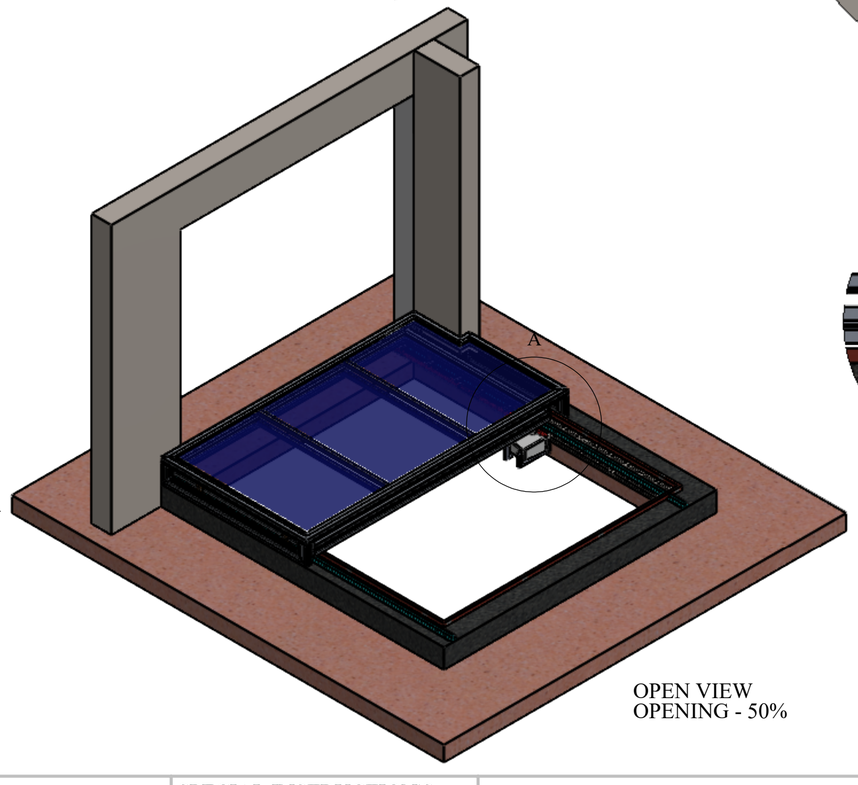

OPEN VIEW
OPENING - 50%

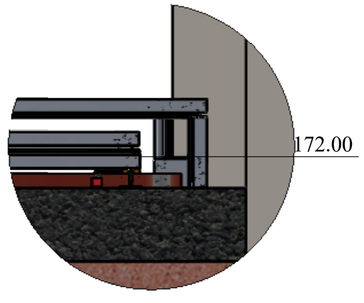

DETAIL C
SCALE 1 : 15

NOTE :

GA DRAWING
FOR MOTOR & TRACK MOUNTING FABRICATION REQUIRED
ALL CIVIL WORK & FABRICATION IN CLIENT SCOPE
PANEL COVERING / GLASS IN CLIENT SCOPE

SPECIAL INSTRUCTION'S :

TITLE - ROOF AUTOMATION

DWG NO - NTPL-000-PM-001-00-00-00

NIHVA Technologies Pvt. Ltd.


NIHVA TECHNOLOGIES PVT.LTD.PUNE
Website - www.nihva.com


	NAME	SIGNATURE	DATE
DRAWN	V.W.		18-05-2026
CHK'D	B.S.		19-05-2026
APPV'D	V.T.		19-05-2026


PRODUCT - RETRACTABLE ROOF
PROJECT NO - NTPL-000-PM
REVISION - 00
SITE LOCATION -
WEIGHT -
MATRIAL -
QTY - 1
If any queries contact - info@nihva.com/support
PROJECTION METHOD:
SCALE :
ALL DIMENSION ARE IN mm
A2
SHEET 1 OF 2


DRAWING

REV DESCRIPTION	DATE	REV NO
	18-05-2026	REV 00
1.		

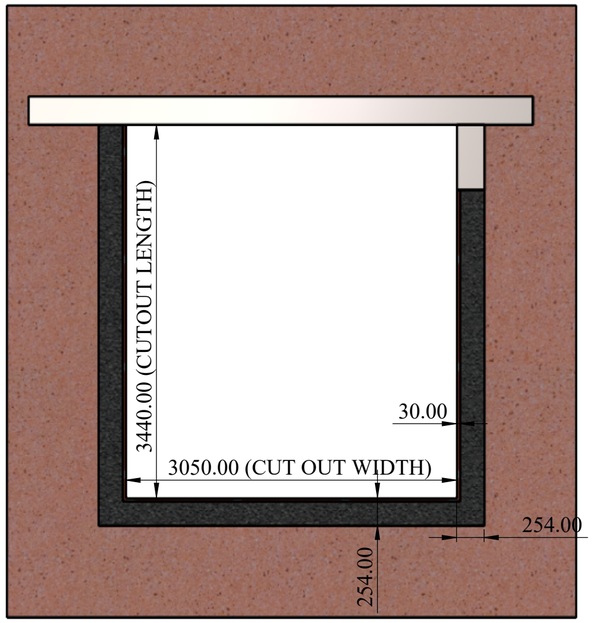

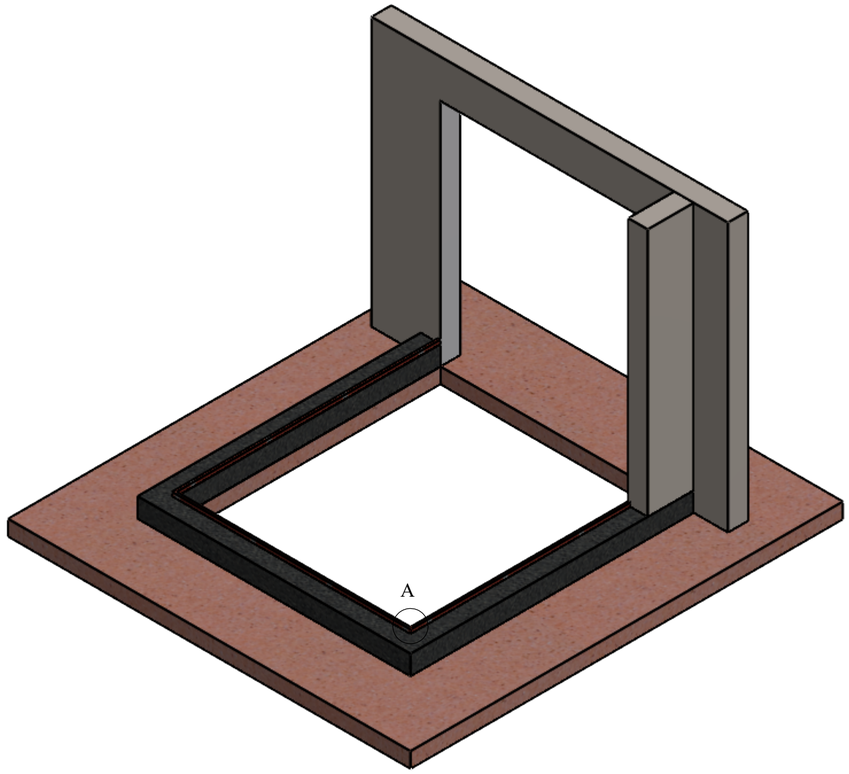

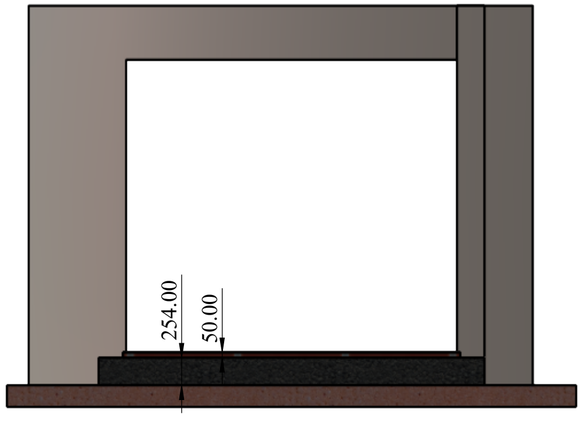

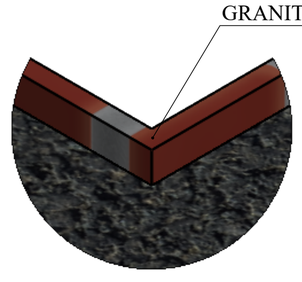

DETAIL A
SCALE 1 : 5

NOTE :

CIVIL DRAWING
FOR MOTOR & TRACK MOUNTING FABRICATION REQUIRED
ALL CIVIL WORK & FABRICATION IN CLIENT SCOPE

SPECIAL INSTRUCTION'S :

TITLE - ROOF AUTOMATION

DWG NO - NTPL-000-PM-001-00-00-00

NIHVA TECHNOLOGIES PVT.LTD.PUNE
Website - www.nihva.com

	NAME	SIGNATURE	DATE
DRAWN	V.W.		18-05-2026
CHK'D	B.S.		19-05-2026
APPV'D	V.T.		19-05-2026

PRODUCT - RETRACTABLE ROOF
PROJECT NO - NTPL-000-PM
REVISION - 00
SITE LOCATION -
WEIGHT -
MATRIAL -
QTY - 1
SCALE :
PROJECTION METHOD:
SHEET 2 OF 2

If any queries contact - info@nihva.com/support
ALL DIMENSION ARE IN mm
A2