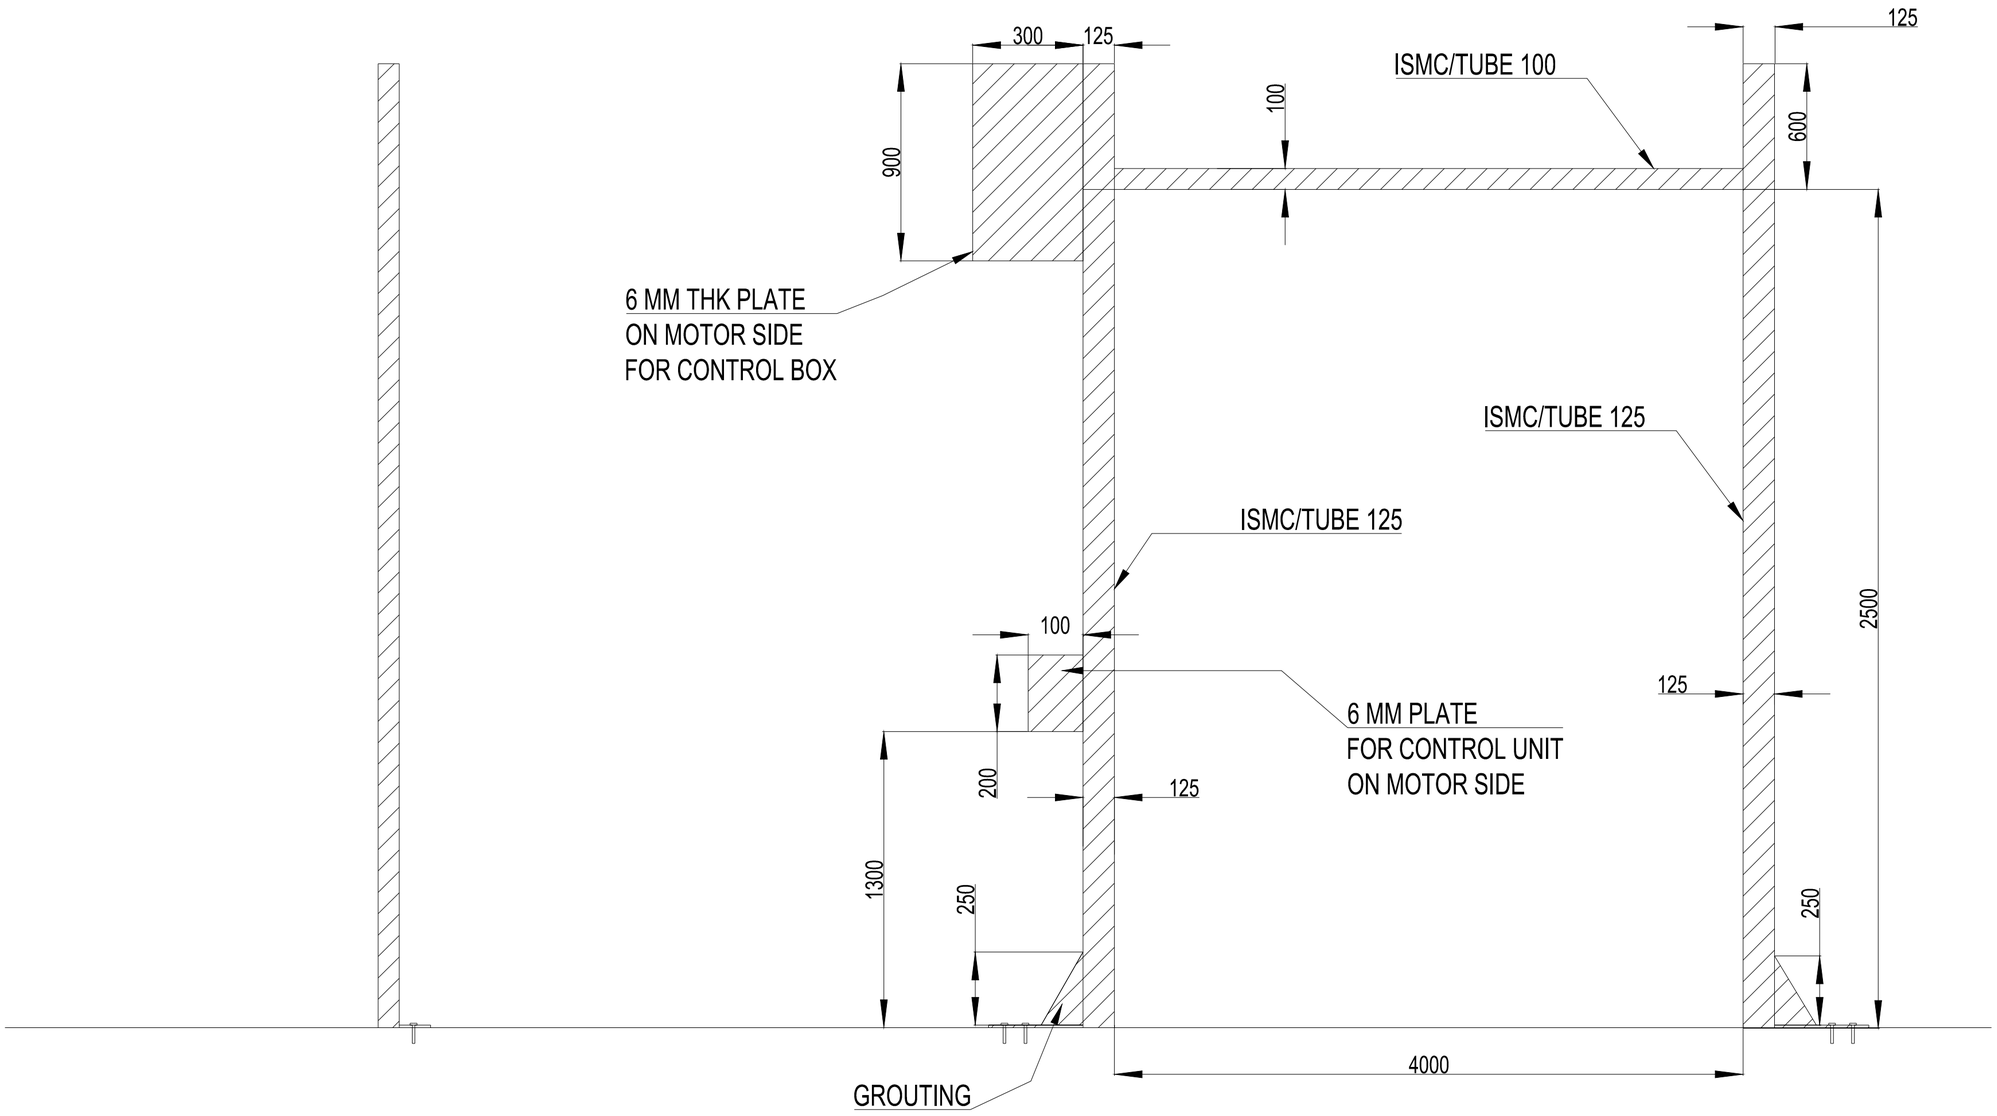


M.S. STRUCTURE S.V.

M.S. STRUCTURE F.V.

REV NO	DRAWN	DATE	REMARK
R01	S.M.S.	22.2.2021	MOTOR SIDE CHANGED TO LEFT

NOTES-
1. REQUIRED M.S. STRUCTURE , FITTING & ALL CIVIL WORK IS IN CLIENT SCOPE .
2. HIGH SPEED DOOR WILL BE INSTALLED AFTER READINESS OF STRUCTURE AS PER DRAWING .
3. M.S. STRUCTURE SHOULD BE RIGID & NEED TO BE FIXED/WELDED WITH EXISTING STRUCTURE AT SITE .
4. KINDLY WELD PLATES FOR CONTROL BOX & PENDANT TO THE MOTOR SIDE AS PER DRAWING.

CLEAR OPENING WIDTH	CLEAR OPENING HEIGHT	QTY	MOUNTING SURFACE
4000	2500	2 NOS	M.S. STRUCTURE

This drawing & design is the property of NIHVA TECHNOLOGIES. Not to be sold or copied to any other concern.

TITLE ASSA ABLOY RP 300
M.S. STRUCTURE

	NAME	SIGN	DATE
DRAWN	S.M.S.		17.2.2021
CHECK	S.M.S.		17.2.2021
APPRD.			

NIHVA TECHNOLOGIES PVT. LTD.
NIHVA TECHNOLOGIES PVT. LTD. PUNE
Tel : 020 66304033
Email:- info@nihva.com
Website:- www.nihva.com

CLIENT - ABB INDIA LIMITED

PROJECT -

SITE LOCATION - PEENYA , BENGLARU

If any queries contact : projectsupport@nihva.com

DWG. NO. : NIHVA/20-21/0162/R01 REV- R01

ALL DIMENSION ARE IN mm

SCALE: NTS WT: SHEET: 2 OF 2