

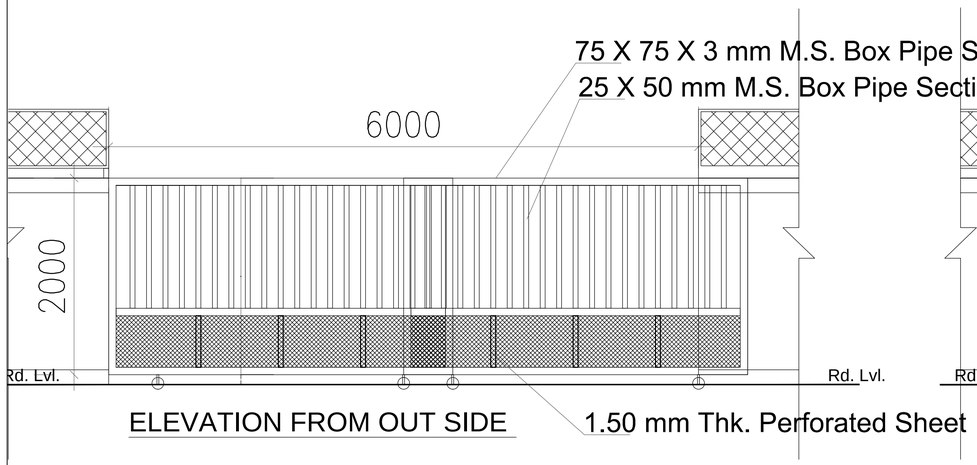


ELEVATION FROM OUT SIDE

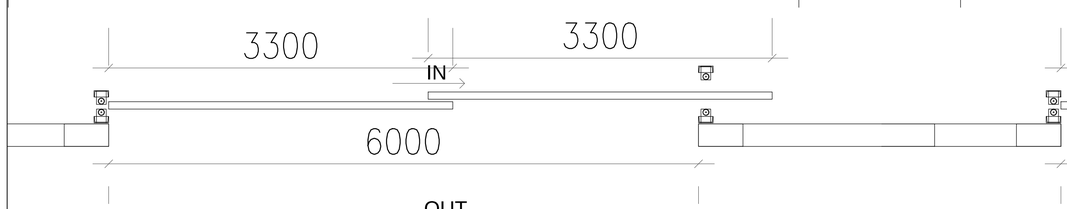


PLAN

6.00 M WIDE TWO LEAF MOTOR GATE
ENTRY GATE

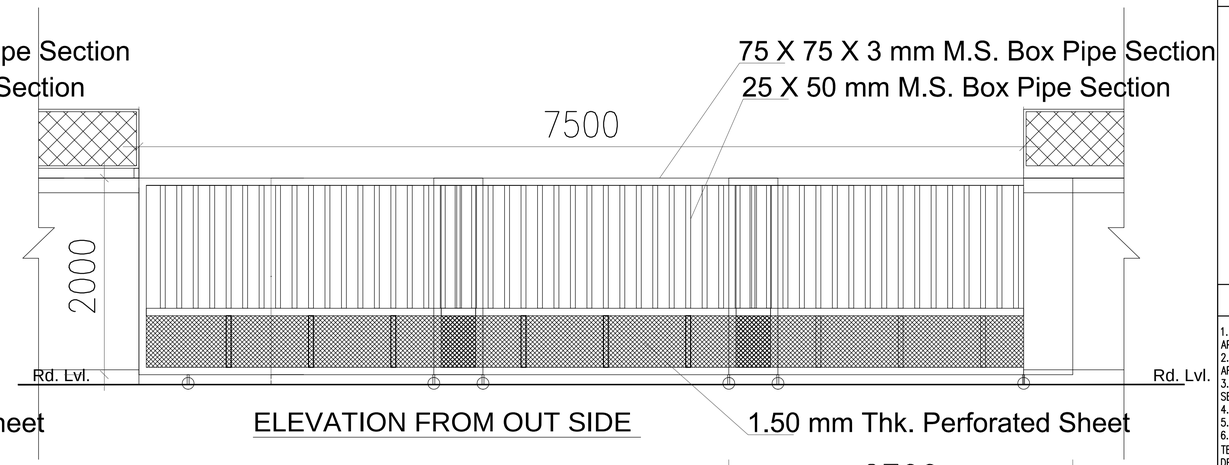


ELEVATION FROM OUT SIDE

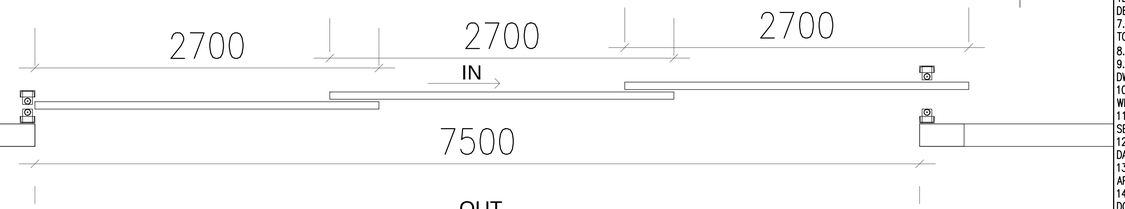


PLAN

7.5 M WIDE THREE LEAF MOTOR GATE
ENTRY GATE

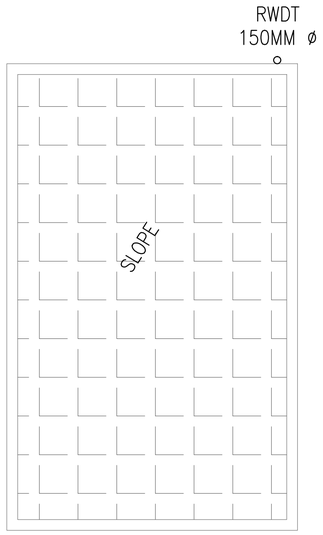


ROOF PLAN

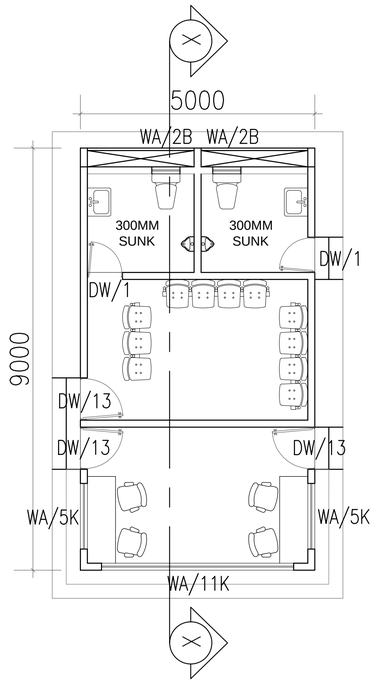


WATCHMEN CABIN PLAN


WATCHMEN CABIN

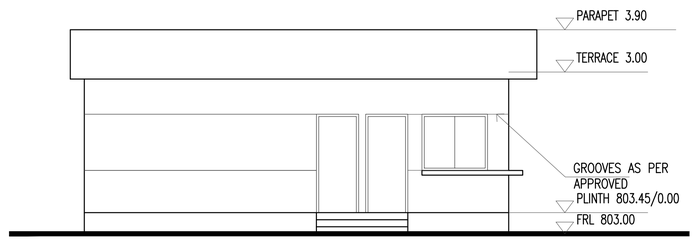


WEST SIDE ELEVATION

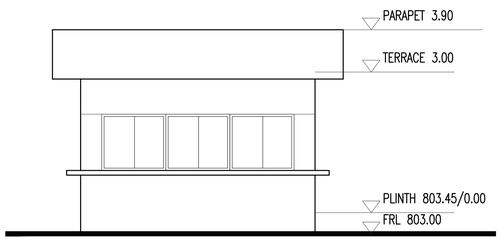

NORTH SIDE ELEVATION

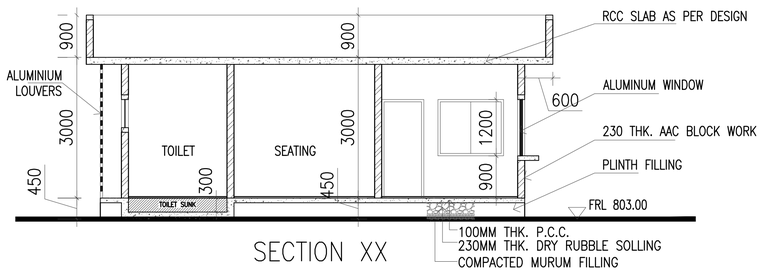

SECTION XX

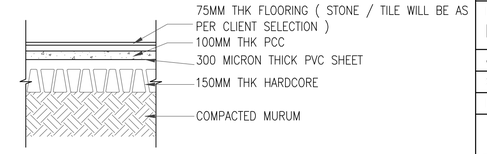

FLOORING SECTION

DWT478_ARCH_TD_ALLIED_BDL_06_R0

FOR TENDER PURPOSE

NOTES FOR CIVIL :

1. REFER DOOR ATTRIBUTES FOR DETAILING, TYPICAL DOOR MOCKUP TO BE APPROVED
2. CONTRACTOR TO GET THE SHOP DRAWINGS PREPARED AND APPROVED FROM ARCHIVISTA BEFORE PROCEEDING WITH ANY WORK.
3. ALL VERTICAL AND HORIZONTAL JOINTS BETWEEN STEEL AND MASONRY TO BE SEALED WITH SEALANTS.
4. ALL DIMENSIONS ARE IN MILLIMETERS.
5. NO DIMENSION TO BE SCALED OFF THE DRAWINGS.
6. THIS DRAWING SHALL BE READ IN CONJUNCTION WITH ALL OTHER RELATED TECHNICAL/ STRUCTURAL/ SERVICES OR APPROVED MUNICIPAL DRAWINGS AND DETAILS.
7. ANY DISCREPANCY IN THIS DRAWING & BOQ SHALL BE IMMEDIATELY BROUGHT TO NOTICE OF THE ARCHITECTS BEFORE QUOTINTING FOR SAID WORK .
8. ALL DIMENSIONS SHALL BE CHECKED/ VERIFIED ON SITE.
9. INTERNAL PARTITIONS AT TOILET TO BE FACTORY MADE HPL BOARD, SHOP DWG TO BE PROVIDED FOR APPROVAL.
10. ALL CUT-OUTS REQUIRED FOR HVAC INSTALLATION TO BE CO-ORINATED WITH PEB AND PUFF PANEL INSTALLATION TEAM.
11. ALL CUT-OUTS IN PANELS, WALLS FOR MEP INSTALLATION TO BE GULLY SEALED, COVERED AMD TO BE MADE FIRE-PROOF.
12. THE SHOP DRAWINGS OF PANELS AT EACH ROOM TO SHOW ELECTRICAL DATA RACEWAY OR CONDUIT POSITIONS AND SWITCH BOARDS.
13. ALL EXTERNAL RAILINGS TO BE IN STAINLESS STEEL, MOCKUP TO BE APPROVED.
14. ALL AIR-SHOWER UNITS TO BE SUPPLIED BY THE CLIENT, HOWEVER GC TO DO THE INSTALLATION, SEALING ETC.
15. ANY ITEMS NOT MENSIONED BOQ BUT SHOWN IN THE DRAWING SHALL BE PART OF ORDER AND NEED TO BE EXECUTED WITH OUT ANY EXTRA CHARGES.

REVISIONS :

NO	DATE	REMARKS

ARCHITECT SIGN

CLIENT SIGN

CLIENT:
PROPOSED FACTORY FOR DIVGI - TTS
PLOT NO. I-07(I-5&I-6). CHORDIYA INDUSTRIAL PARK
SHIRWAL PUNE

TITLE:
SECURITY CABIN AND ENTRY GATES

DRG.NO.
DWT478_ARCH_TD_ALLIED_BDL_06_R0

JOB.NO. : DWT478	DRAWN BY : AKASH
SCALE : NTS	CHECKED BY : PANKAJ
DATE : 05.03.2022	APPROVED BY : SHRIRAM J.

ARCHIVISTA
ENGINEERING PROJECTS PVT.LTD.