OHT SLAB TOP LEVEL
+ 91.00 M

CROWN PORTAL TOP
+89.90M


O.H.T SLAB BOTTOM LEVEL
+88.10 M

TERRACE LEVEL
+85.10 M


22ND FLOOR LEVEL
+82.10 M

21ST FLOOR
+79.10 M


2900
3000
3000
3000

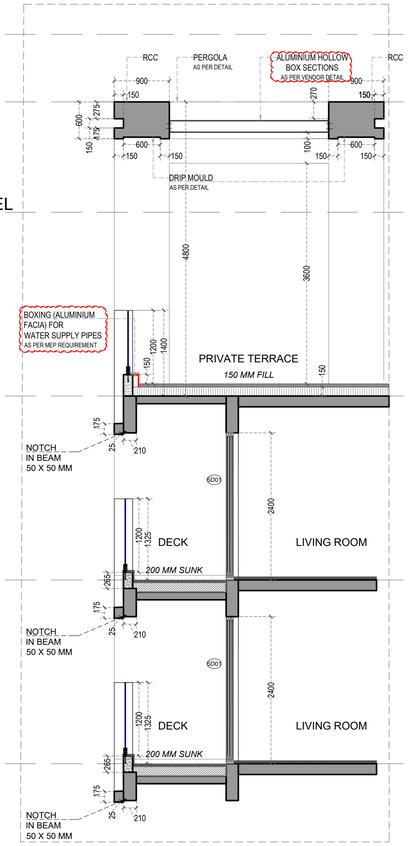


SECTION -1

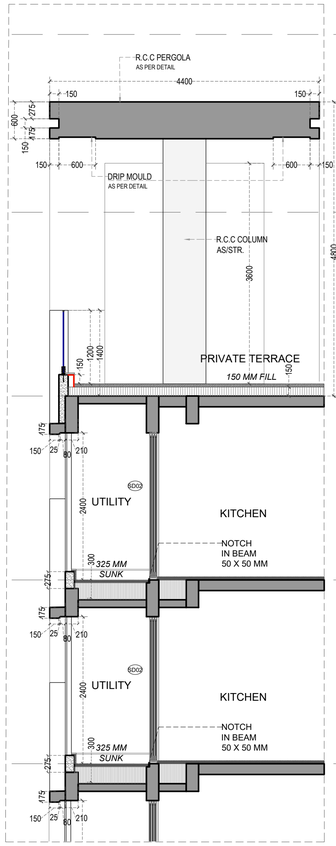


SECTION -2

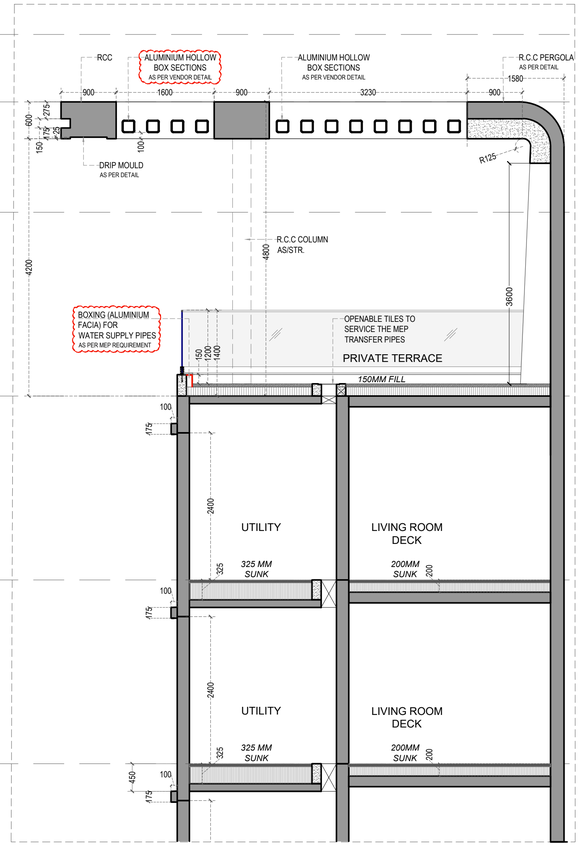


SECTION -2A

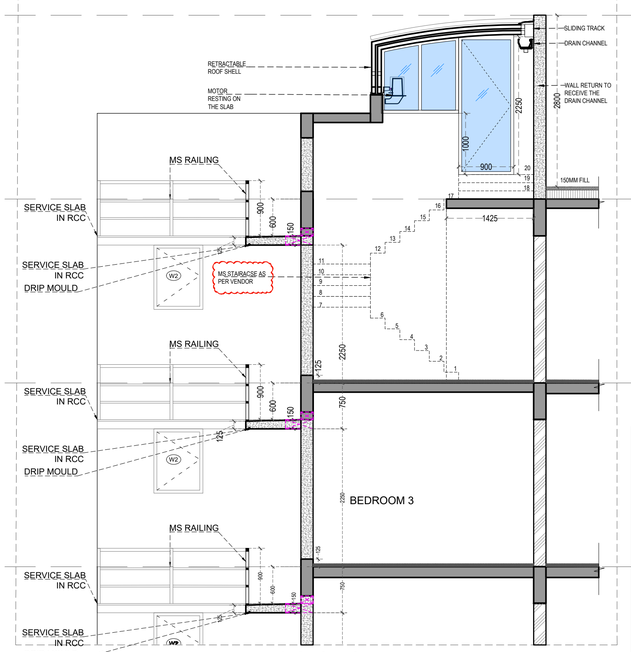

SECTION -3D

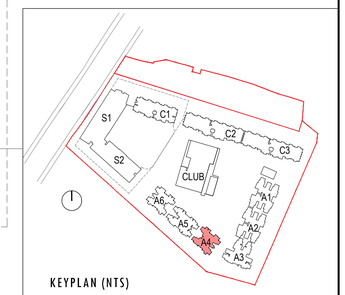

KEYPLAN (NTS)

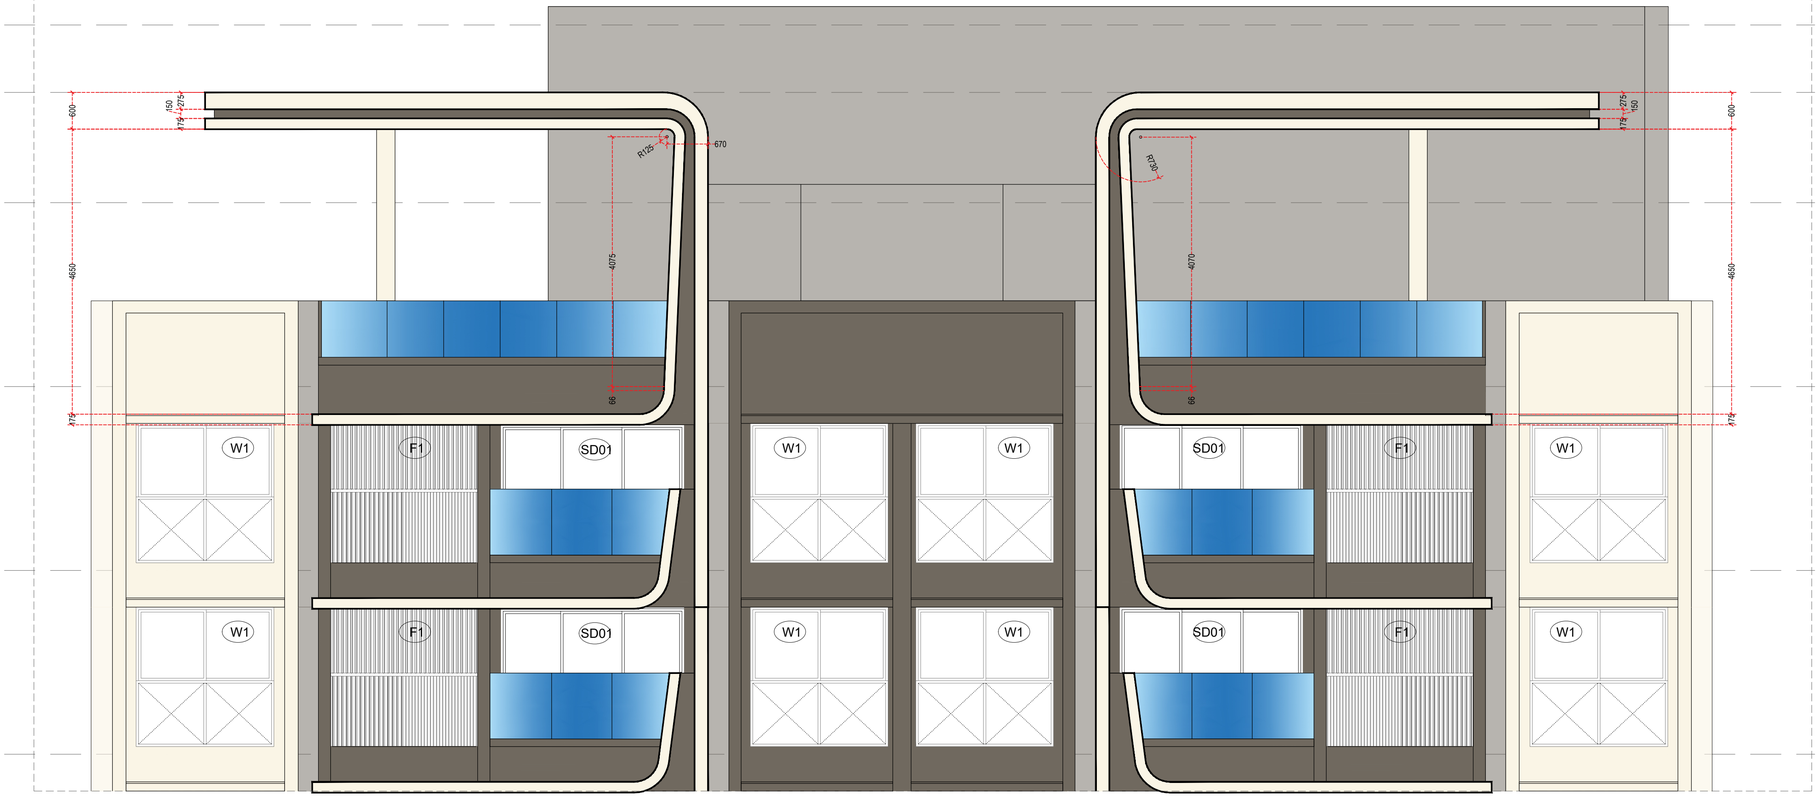

PART ELEVATION A

GENERAL NOTES

1 : All dimensions are in millimeters and levels in meters unless specified otherwise.
2 : Do not scale the drawing; follow written dimensions.
3 : All dimensions are unfinished dimensions unless specified otherwise.
4 : Any discrepancies should be brought to the notice of the Architect prior to execution of job / procuring materials at site.
5 : This drawing is the property of Kapadia Associates and should not be reproduced, copied, handed over to a third party or used for any purpose other than for which it has been issued.
6 : This drawing is to be read in conjunction with all relevant structural & services drawings.

NOTE:

1. PLEASE READ IN CONJUNCTION WITH KITCHEN DETAIL,TOILET DETAIL, FIN DETAIL & RAILING DETAIL, STAIRCASE DETAILS.
2. 10MM ADDITIONAL COVER HAS BEEN INCLUDED IN THE SHEAR WALL THICKNESS, WHEREVER REQUIRED FOR GROOVE.
3. HIGHLIGHTED AREAS ARE UNDER DISCUSSION

REVISION INDEX

REV. NO.	DATE	REMARKS
R00	29-04-2026	VFC ISSUED

CLIENT

LODHA GROUP

PROJECT TITLE

LODHA RISERVO - A4

VIKHROLI,MUMBAI

DRAWING TITLE & NO.

AR-KA-A4-401.1_TERRACE WALL SECTIONS

DRAWING STAGE

WORKING DRAWING

SCALE	REV. NO.	REV. DATE
1:50	R00	29-04-2026

STAMP & SIGNATURE

Digitally signed by: SUPRIYA UKIDAVE
Date: 2026.04.29 19:52:32 +06'30'

KAPADIA ASSOCIATES
architecture • urban design
112-114, Peninsula Centre,Dr. S.S. Rao Road,Parel East, Mumbai 400012
Tel : 91-22-6660 2838 / 39 E-mail : kapl@kapl.in Website : www.kapl.in