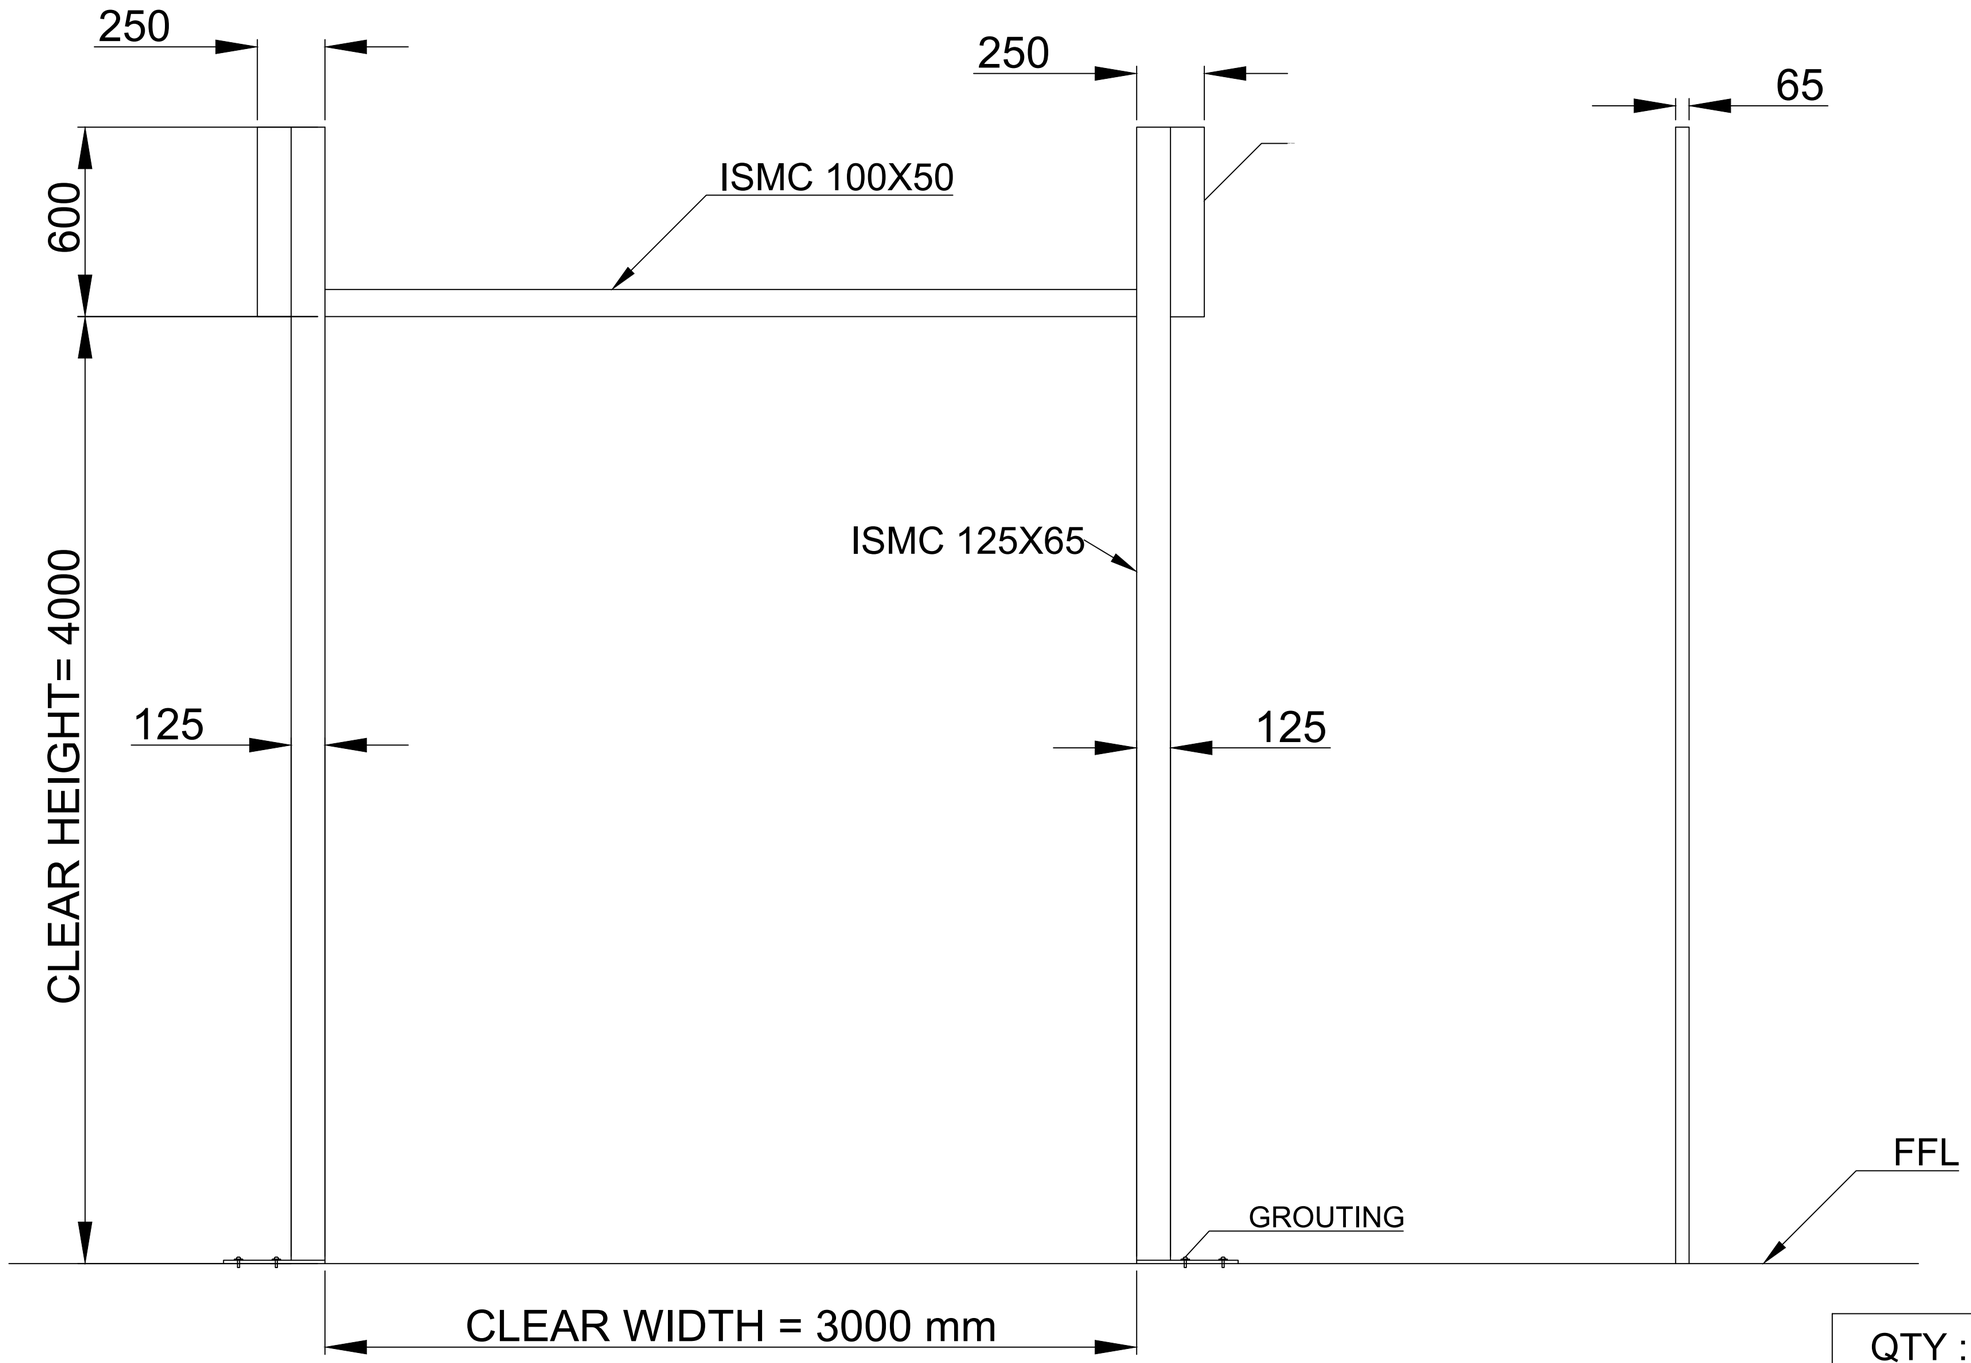


QTY : 1 NO

NOTE -
(1) ALL REQUIRED TECHNICAL MS STRUCTURE & FITTING IN CLIENT SCOPE .
(2) ALL CIVIL WORK IN CLIENT SCOPE .

This drawing & design is the property of NIHVA TECHNOLOGIES. Not to be sold or copied to any other concern.

TITLE	ALUMINUM HIGH SPEED ROLLING SHUTTER STRUCTURE DWG			NIHVA TECHNOLOGIES PVT. LTD. PUNE Tel : 020 66304033 Email:- info@nihva.com Website:- www.nihva.com
	NAME	SIGN	DATE	
DRAWN	MAHESH S.		24.08.2022	CLIENT - AMULYA TRADERS
CHECK	MAHESH S.		24.08.2022	PROJECT - JOHN DEERE
APPRD.	AMIT K.		24.08.2022	SITE LOCATION - PUNE
If any queries contact : projectsupport@nihva.com				DWG. NO. : NIHVA/22-23/MFG/0070 — REV- 0
ALL DIMENSION ARE IN mm				SCALE: NTS — WT: — SHEET: 01 OF 01