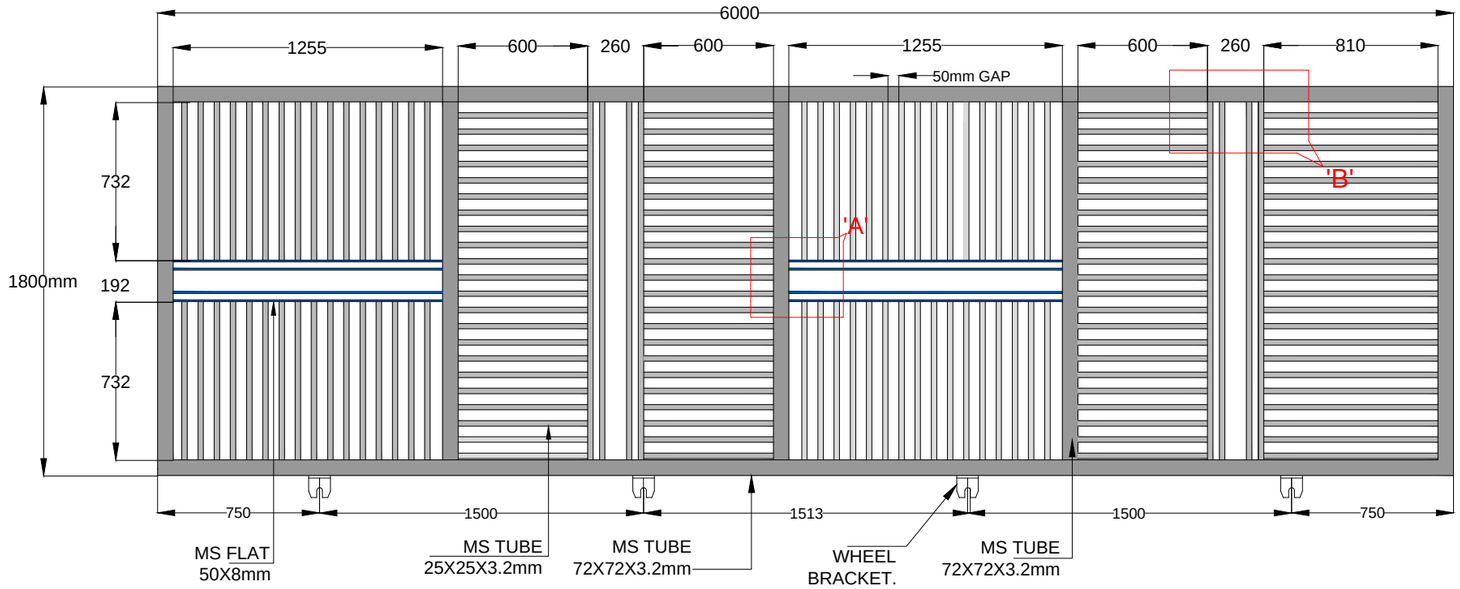

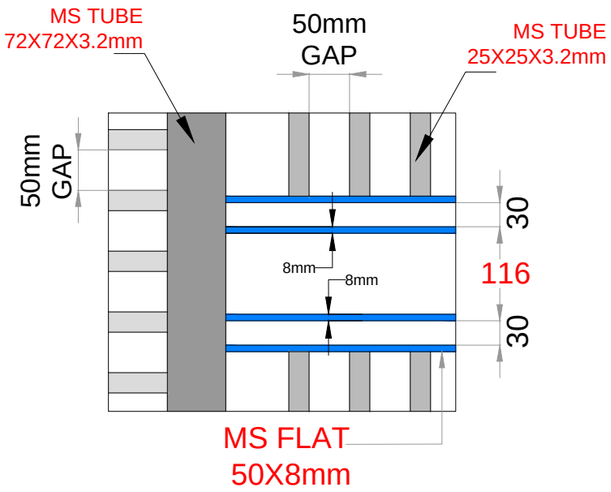

DETAIL VIEW OF 'A'.

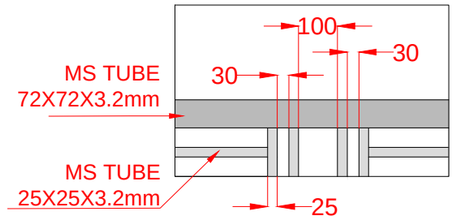

DETAIL VIEW 'B'

SR NO	CLEAR WIDTH	CLEAR HEIGHT	QTY.
1	6000mm	1800mm	01 NOS

NOTE:-WHEEL BRACKET PROFILE ONLY LASER CUTTING.

This drawing & design is the property of NIHVA TECHNOLOGIES. Not to be sold or copied to any other concern.

TITLE
SLIDING GATE LEAF 02

NIHVA TECHNOLOGIES PVT. LTD.

NIHVA TECHNOLOGIES
PVT. LTD. PUNE
Tel : 020 66304033
Email:- info@nihva.com
Website:- www.nihva.com

	NAME	SIGN	DATE
DRAWN	SURAJ		31-03-2018
CHECK	OMKAR		31-03-2018
APPRD.	SHEKHAR		31-03-2018

CLIENT -
PROJECT -
SITE LOCATION -
If any queries contact : design@nihva.com
DWG. NO. : NIHVA/17-18/ VDR/0269.
REV- 0
ALL DIMENSION ARE IN mm
SCALE: NTS
WT:
SHEET: 01 OF 01