

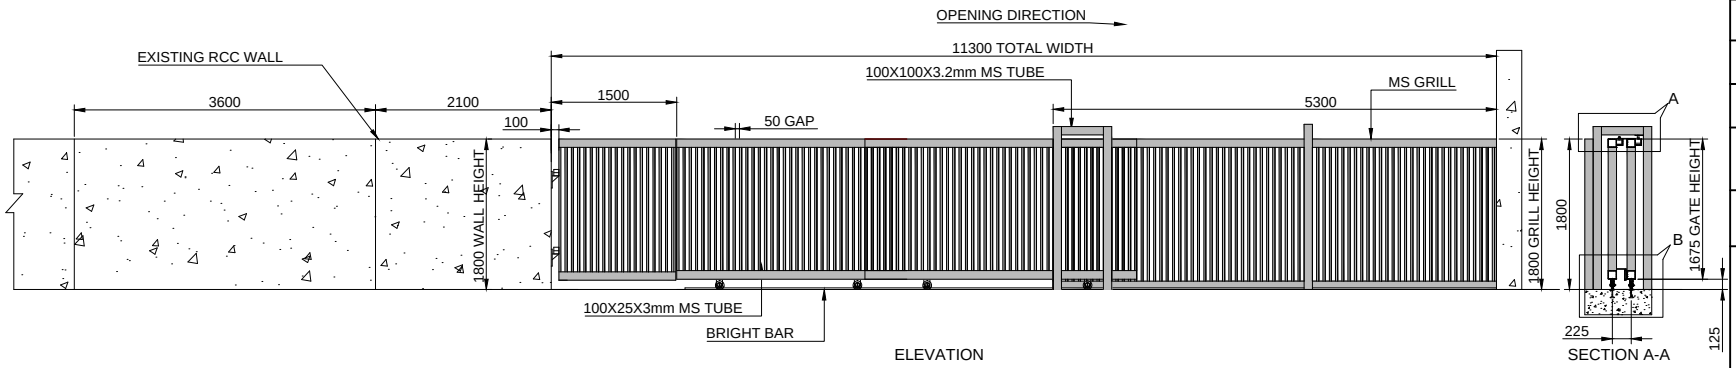


ELEVATION


SECTION A-A

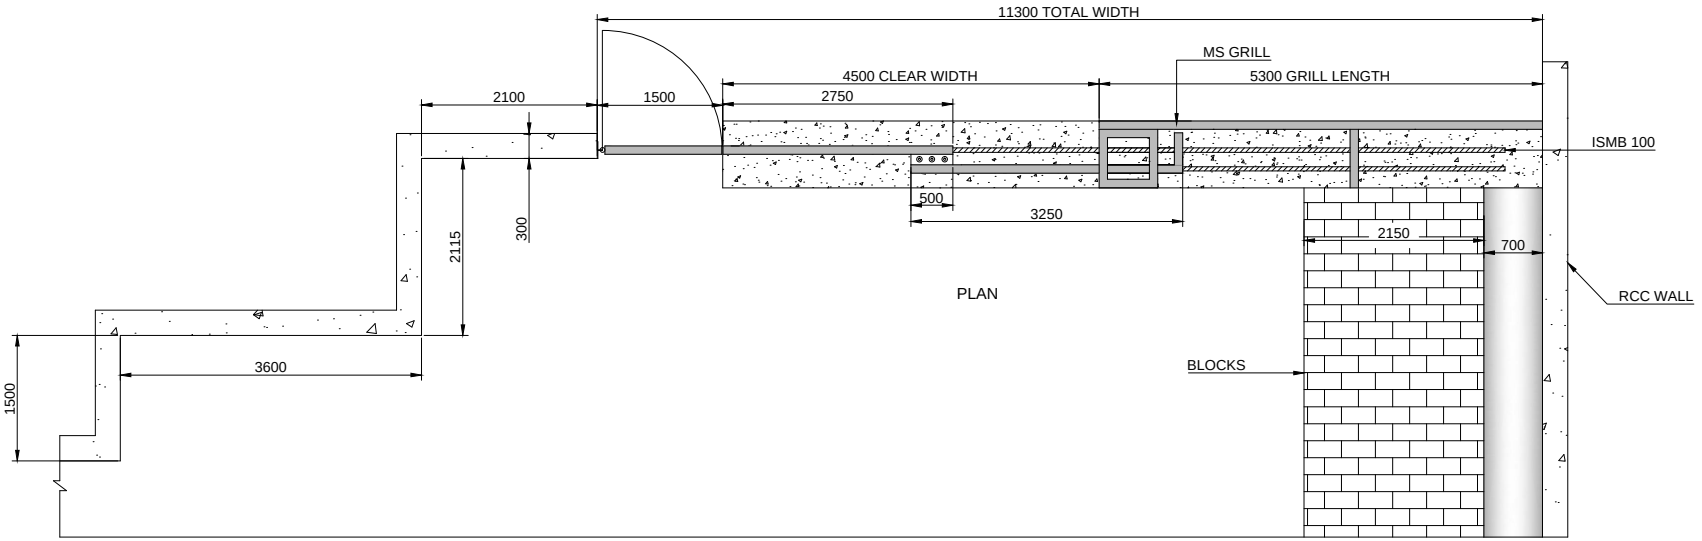

PLAN

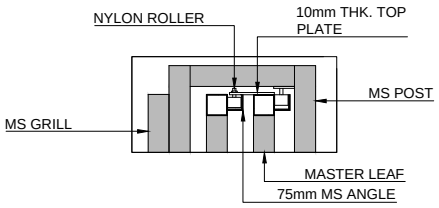

DETAILED VIEW OF A

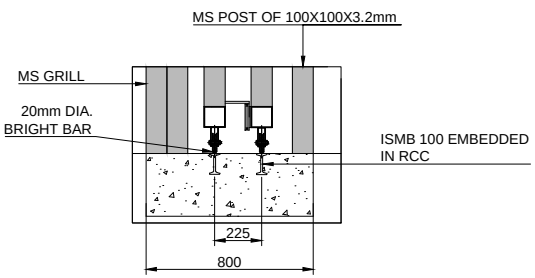

DETAILED VIEW OF B

OPTION 3

DIMENSION :		
CLEAR WIDTH	CLEAR HEIGHT	QUANTITY
5500 mm	1800 mm	01 NOS.
1500 mm	1800 mm	01 NOS.

MATERIAL :

THICKNESS :

NIHVA TECHNOLOGIES PVT. LTD.

NIHVA TECHNOLOGY PVT. LTD. PUNE
Email:- info@nihva.com
Website:- www.nihva.com

TITLE:

TWO LEAF TELESCOPIC GATE (MANUAL) & WICKET GATE

CLIENT'S APPROVAL :

CLIENT - LUPIN LIMITED

PROJECT -

SITE LOCATION - SUS ROAD,PUNE

DWG. NO. : NIHVA/16-17/113/3

SCALE: NTS	WT:	SHEET:1 OF 1
DRAWN BY: OMKAR		DATE: 10-12-2016
CHECK : SAGAR P.		DATE: 10-12-2016

If any queries contact : projects@nihva.com

NOTE: ALL DIMENSION ARE IN mm

THIS DRAWING & DESIGNING IS THE PROPERTY OF NIHVA TECHNOLOGIES. NOT BE SOLD OR COPY TO ANY OTHER CONCERN.