



FOUNDATION AND BEAM FOR SLIDING TRACK

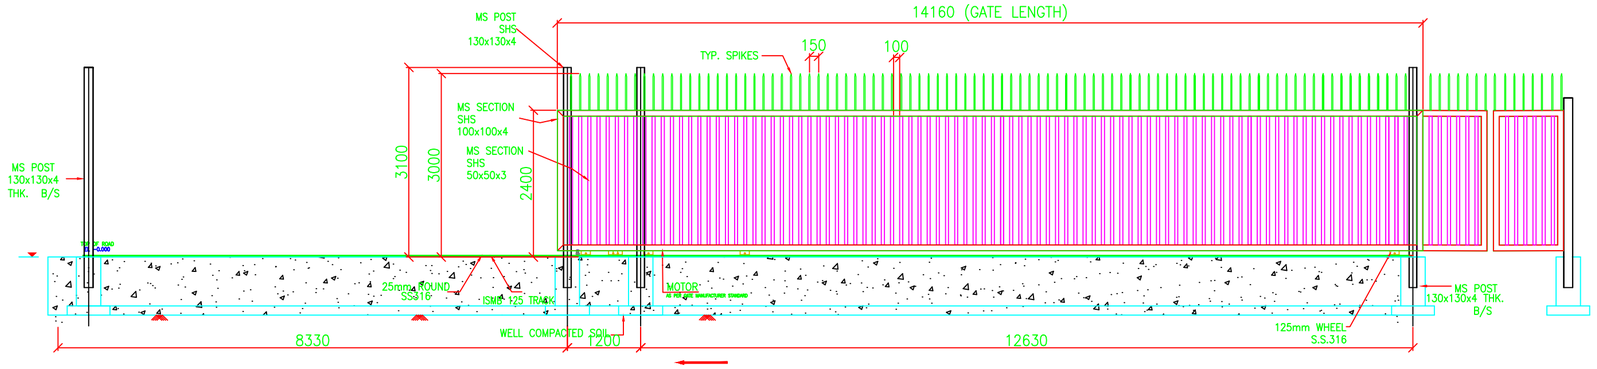


SECTION A-A


Note: All Structural Steel Members confirming Grade A – E250 as per IS:2062.

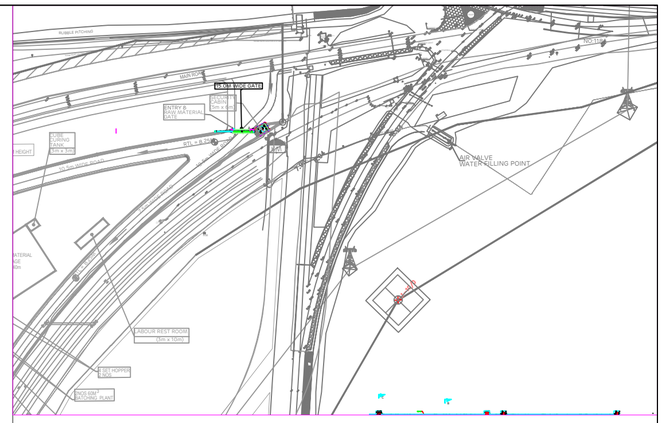


KEY PLAN

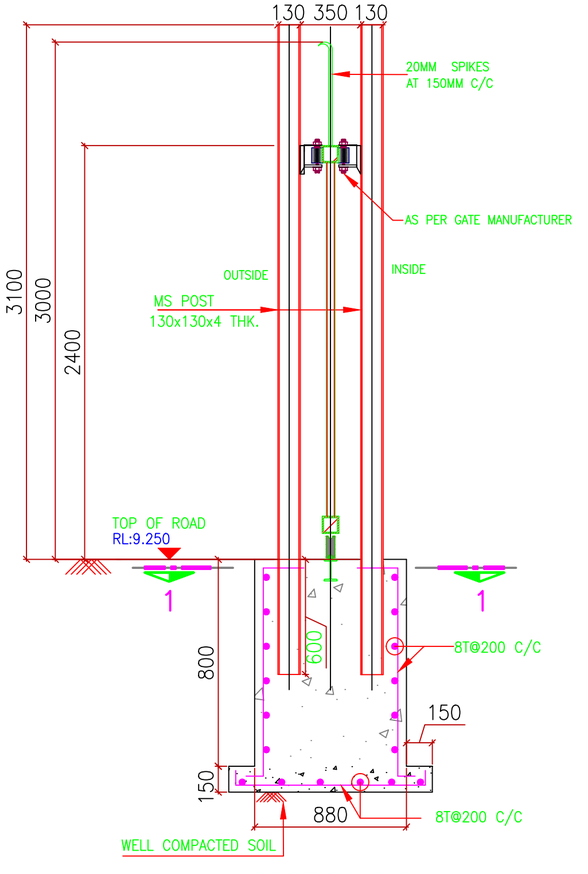


SECTION C-C

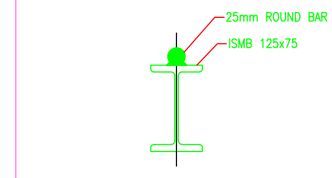


BEAM FOR SLIDING TRACK
(SCALE 1:5)

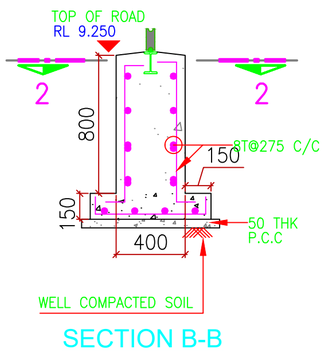

SECTION B-B

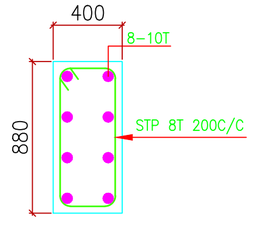

SECTION 1-1
(TYP. PEDESTAL DETAILS)

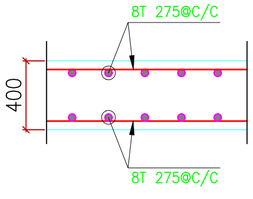

SECTION 2-2
(TYP. PEDESTAL DETAILS)

REV.NO.	DESCRIPTION	DRAWN	DESIGN	CHKD.	M	E	C	C&I	L/O	APPD	DATE
0	RELEASED FOR CONSTRUCTION	DSG	MCC/DF	SM						SSG	18-09-24

	NAME	SIGN	DATE
DRAWN	DSG		18-09-24
DESIGNED			
CHECKED			
DEPT.HEAD			
PROJ.MGR.	-------		

TITLE: DETAIL OF 15.0m WIDE SLIDING GATE FOR PRECAST YARD

RELEASED FOR		
	PRELIMINARY	
	TENDER	
	ENGINEERING	
	CONSTRUCTION	✓

SCALE : AS SHOWN | SHEET: 1 OF 1 | SIZE : A0

DWG.NO. 59AA-E-CIV-SLG-DC-G-I-0002

REV. 0

SIZE-A0