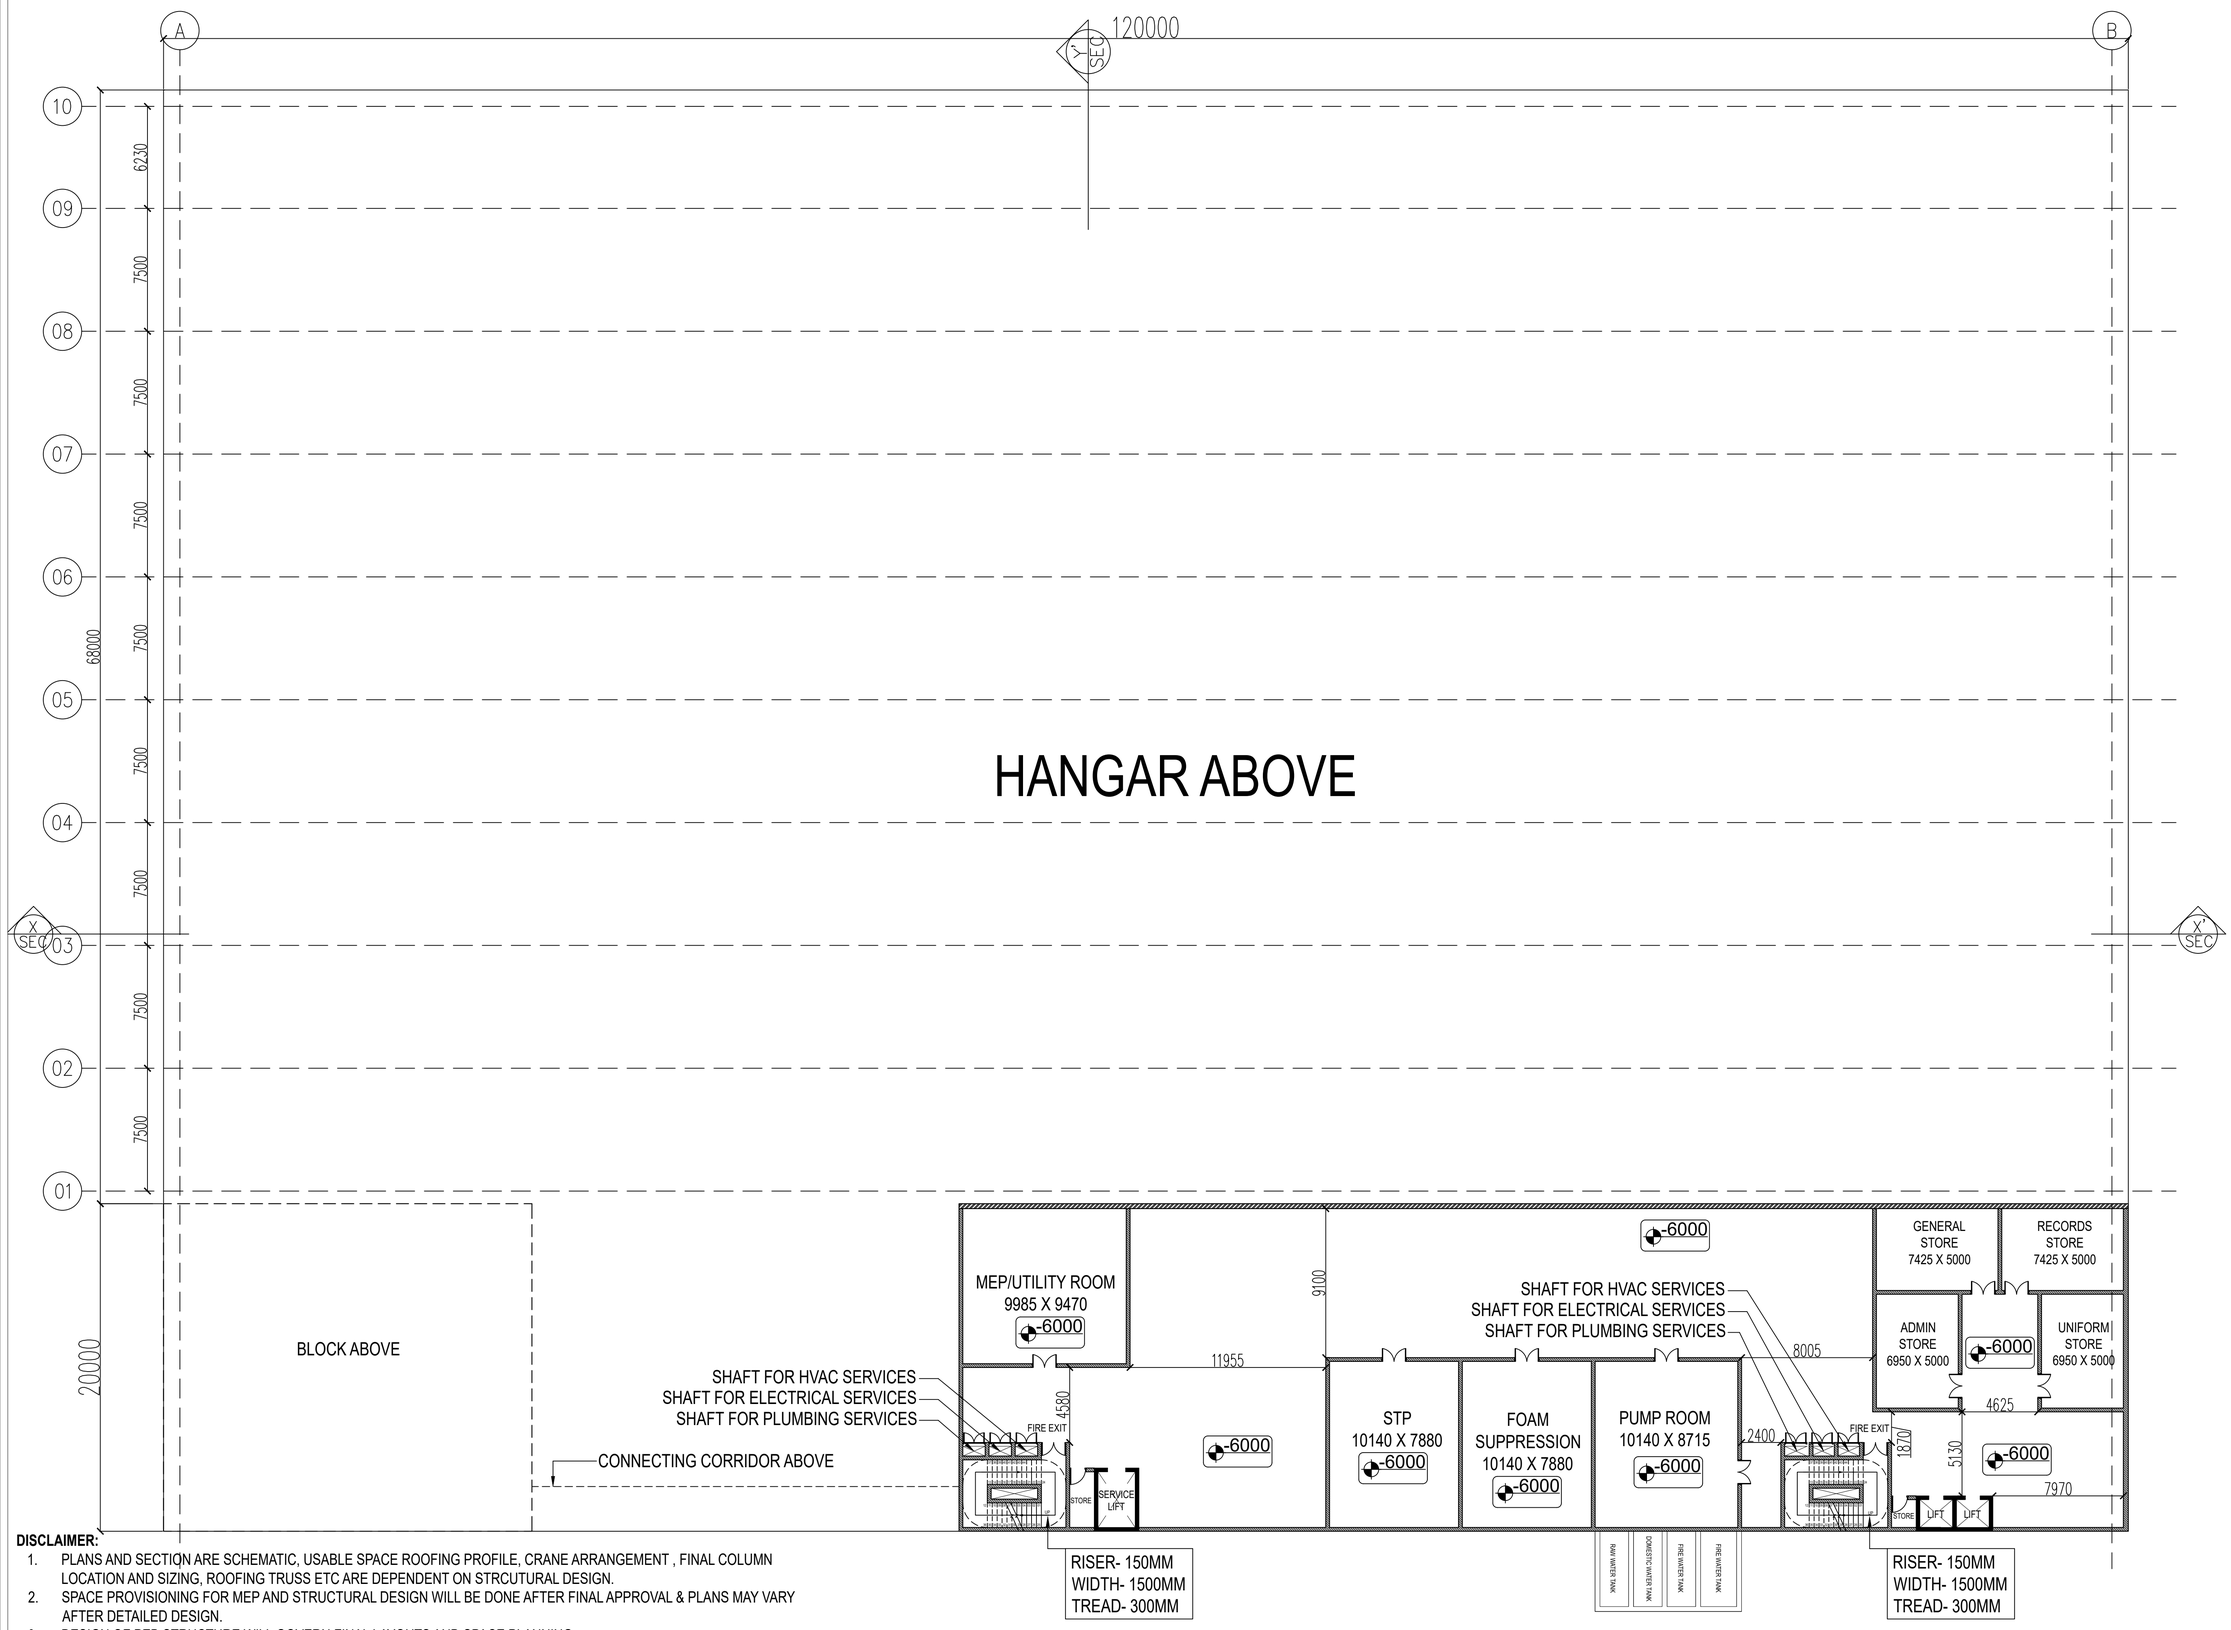


DISCLAIMER:

1. PLANS AND SECTIQN ARE SCHEMATIC, USABLE SPACE ROOFING PROFILE, CRANE ARRANGEMENT , FINAL COLUMN LOCATION AND SIZING, ROOFING TRUSS ETC ARE DEPENDENT ON STRCUTURAL DESIGN.
2. SPACE PROVISIONING FOR MEP AND STRUCTURAL DESIGN WILL BE DONE AFTER FINAL APPROVAL & PLANS MAY VARY AFTER DETAILED DESIGN.
3. DESIGN OF PEB STRUCTURE WILL GOVERN FINAL LAYOUTS AND SPACE PLANNING
4. OCCUPIED FUNCTIONS SUBJECT TO STATUTORY APPROVALS.
5. FINAL SPAN OF HANGAR WILL BE DEPENDENT ON FINAL ROOFING PROFILE AND STRUCTURAL DESIGN.

NOTES:

1. ALL DIMENSIONS ARE IN MILLIMETER
2. ANY REUSE OF EXISTING MATERIAL TO BE CO-ORDINATED DURING FINAL DESIGN.
3. ANY MEP DESIGN TO BE CO-ORDINATED DURING FINAL DESIGN.
4. THIS DRAWING IS NOT TO BE SCALED.
5. ANY DISCREPENCIES TO BE BROUGHT TO THE NOTICE OF THE ARCHITECTS.

FOR APPROVAL

PROJECT:
SARDAR VALLABHBHAI PATEL INTERNATIONAL AIRPORT T1 & T2 ENHANCEMENT

CLIENT:
adani
ADANI AHMEDABAD INTERNATIONAL AIRPORT LTD.

CONSULTANT : ARCHITECTURE & DESIGN

inCUBIS BUILTENVIRONMENTSINDUSTRIALDESIGN
inCUBIS CONSULTANTS (India) Private Limited
804-806, Emaar Palm Square, Sector-66,Golf Course Extension, Gurugram - 122102, India.
Telephones +91-124 451 8750 email - incubis@incubis.net www.incubis.net

REVISIONS

REF.	DATE	DESCRIPTION

PROJECT: **SARDAR VALLABHBHAI PATEL INTERNATIONAL AIRPORT T1 & T2 ENHANCEMENT**

STATUS: FOR APPROVAL

DRAWING TITLE: MRO BASEMENT LAYOUT


JOB No. NH8 SCALE: --

	NAME	SIGN	DATE	SIZE: @ A3
DSGN				NORTH
DRWN	NA		26.07.2024	
CHKD	VD			
APPD	AKG			

DRAWING No. 2023/INC/AIA.A/MRO/001 REV: R0

RELEASED FOR

☐ INFORMATION ☒ APPROVAL ☐ TENDER ☐ CONSTRUCTION ☐ AS BUILT

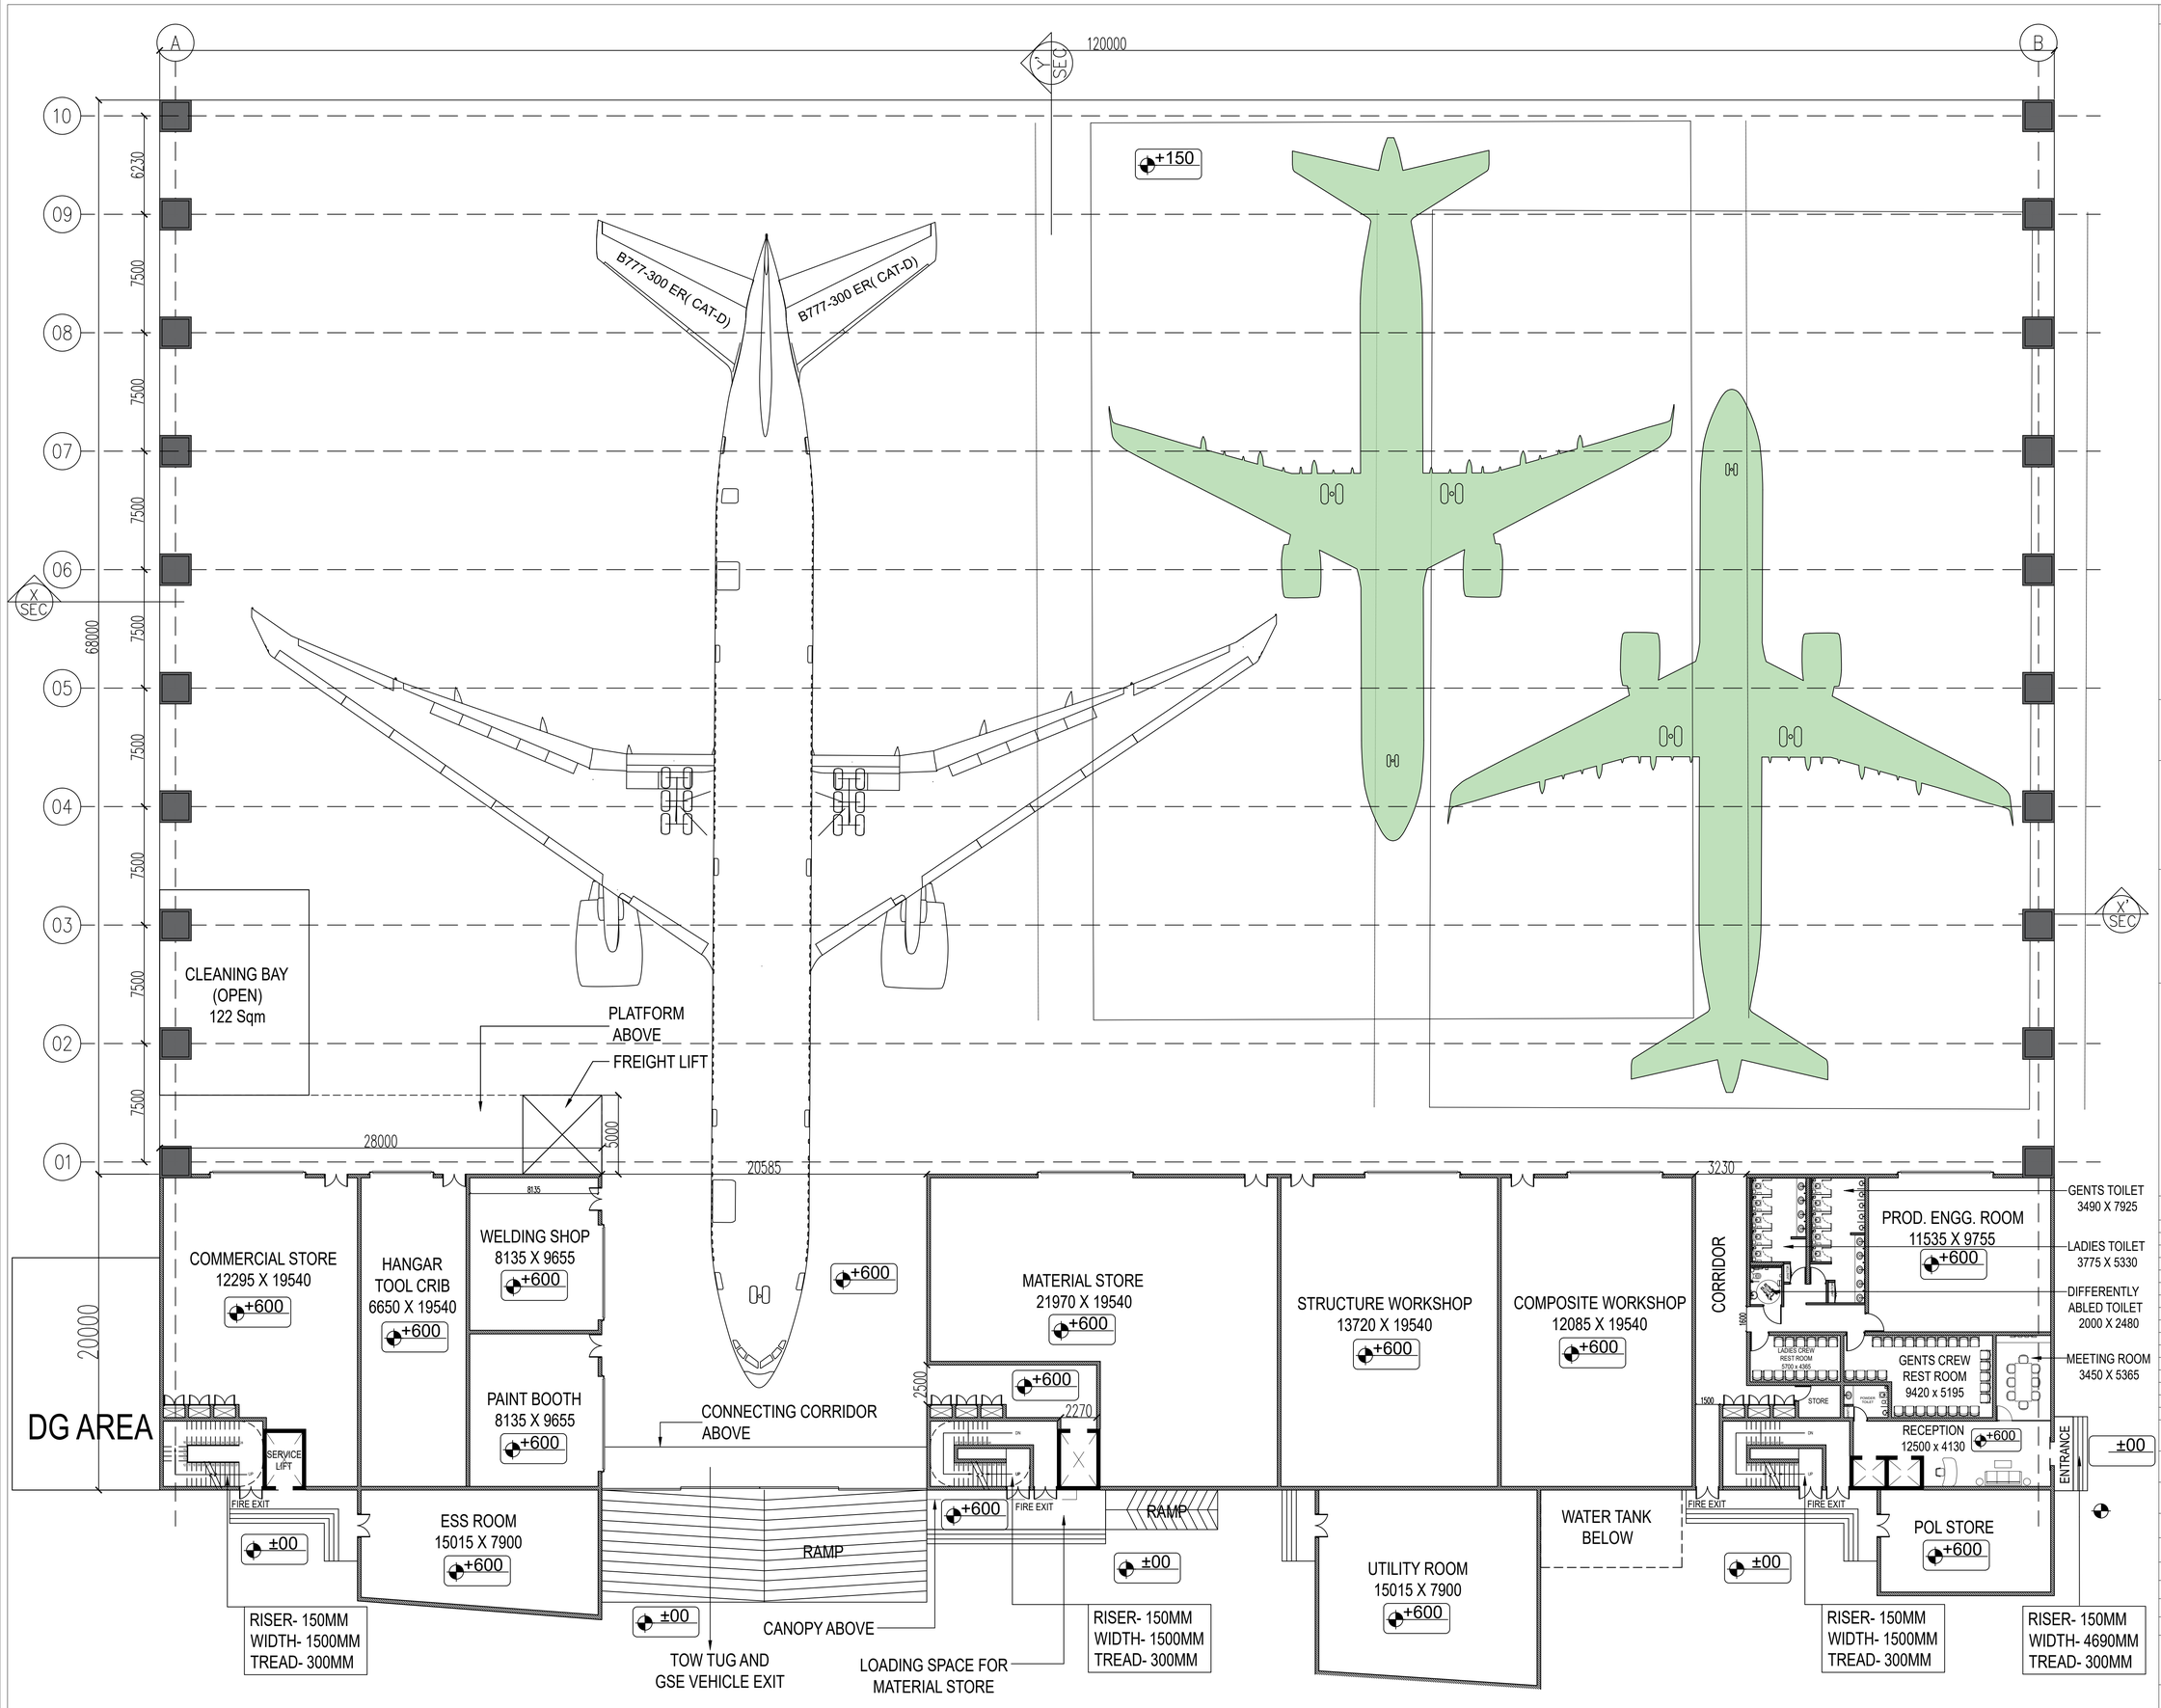

NOTES:

DISCLAIMER:

1. PLANS AND SECTION ARE SCHEMATIC, USABLE SPACE ROOFING PROFILE, CRANE ARRANGEMENT , FINAL COLUMN LOCATION AND SIZING, ROOFING TRUSS ETC ARE DEPENDENT ON STRCUTURAL DESIGN.
2. SPACE PROVISIONING FOR MEP AND STRUCTURAL DESIGN WILL BE DONE AFTER FINAL APPROVAL & PLANS MAY VARY AFTER DETAILED DESIGN.
3. DESIGN OF PEB STRUCTURE WILL GOVERN FINAL LAYOUTS AND SPACE PLANNING
4. OCCUPIED FUNCTIONS SUBJECT TO STATUTORY APPROVALS.
5. FINAL SPAN OF HANGAR WILL BE DEPENDENT ON FINAL ROOFING PROFILE AND STRUCTURAL DESIGN.

FOR APPROVAL

PROJECT:
SARDAR VALLABHBHAI PATEL INTERNATIONAL AIRPORT T1 & T2 ENHANCEMENT

CLIENT:
ADANI AHMEDABAD INTERNATIONAL AIRPORT LTD.

CONSULTANT : ARCHITECTURE & DESIGN

mCUBIS CONSULTANTS (India) Private Limited
804-806, Emaar Palm Square, Sector-66,Golf Course Extension, Gurugram - 122102, India.
Telephones +91-124 451 8750 email - incubis@incubis.net www.incubis.net

REVISIONS

REF.	DATE	DESCRIPTION

PROJECT: **SARDAR VALLABHBHAI PATEL INTERNATIONAL AIRPORT T1 & T2 ENHANCEMENT**

STATUS: FOR APPROVAL

DRAWING TITLE: MRO GROUND FLOOR LAYOUT

JOB No. NH8 SCALE: --

SIZE: @ A3


	NAME	SIGN	DATE
DSGN			
DRWN	NA		
CHKD	VD		
APPD	AKG		

NORTH

DRAWING No. 2023/INC/AIA.A/MRO/002 REV: R0

RELEASED FOR

☐ INFORMATION ☒ APPROVAL ☐ TENDER ☐ CONSTRUCTION ☐ AS BUILT

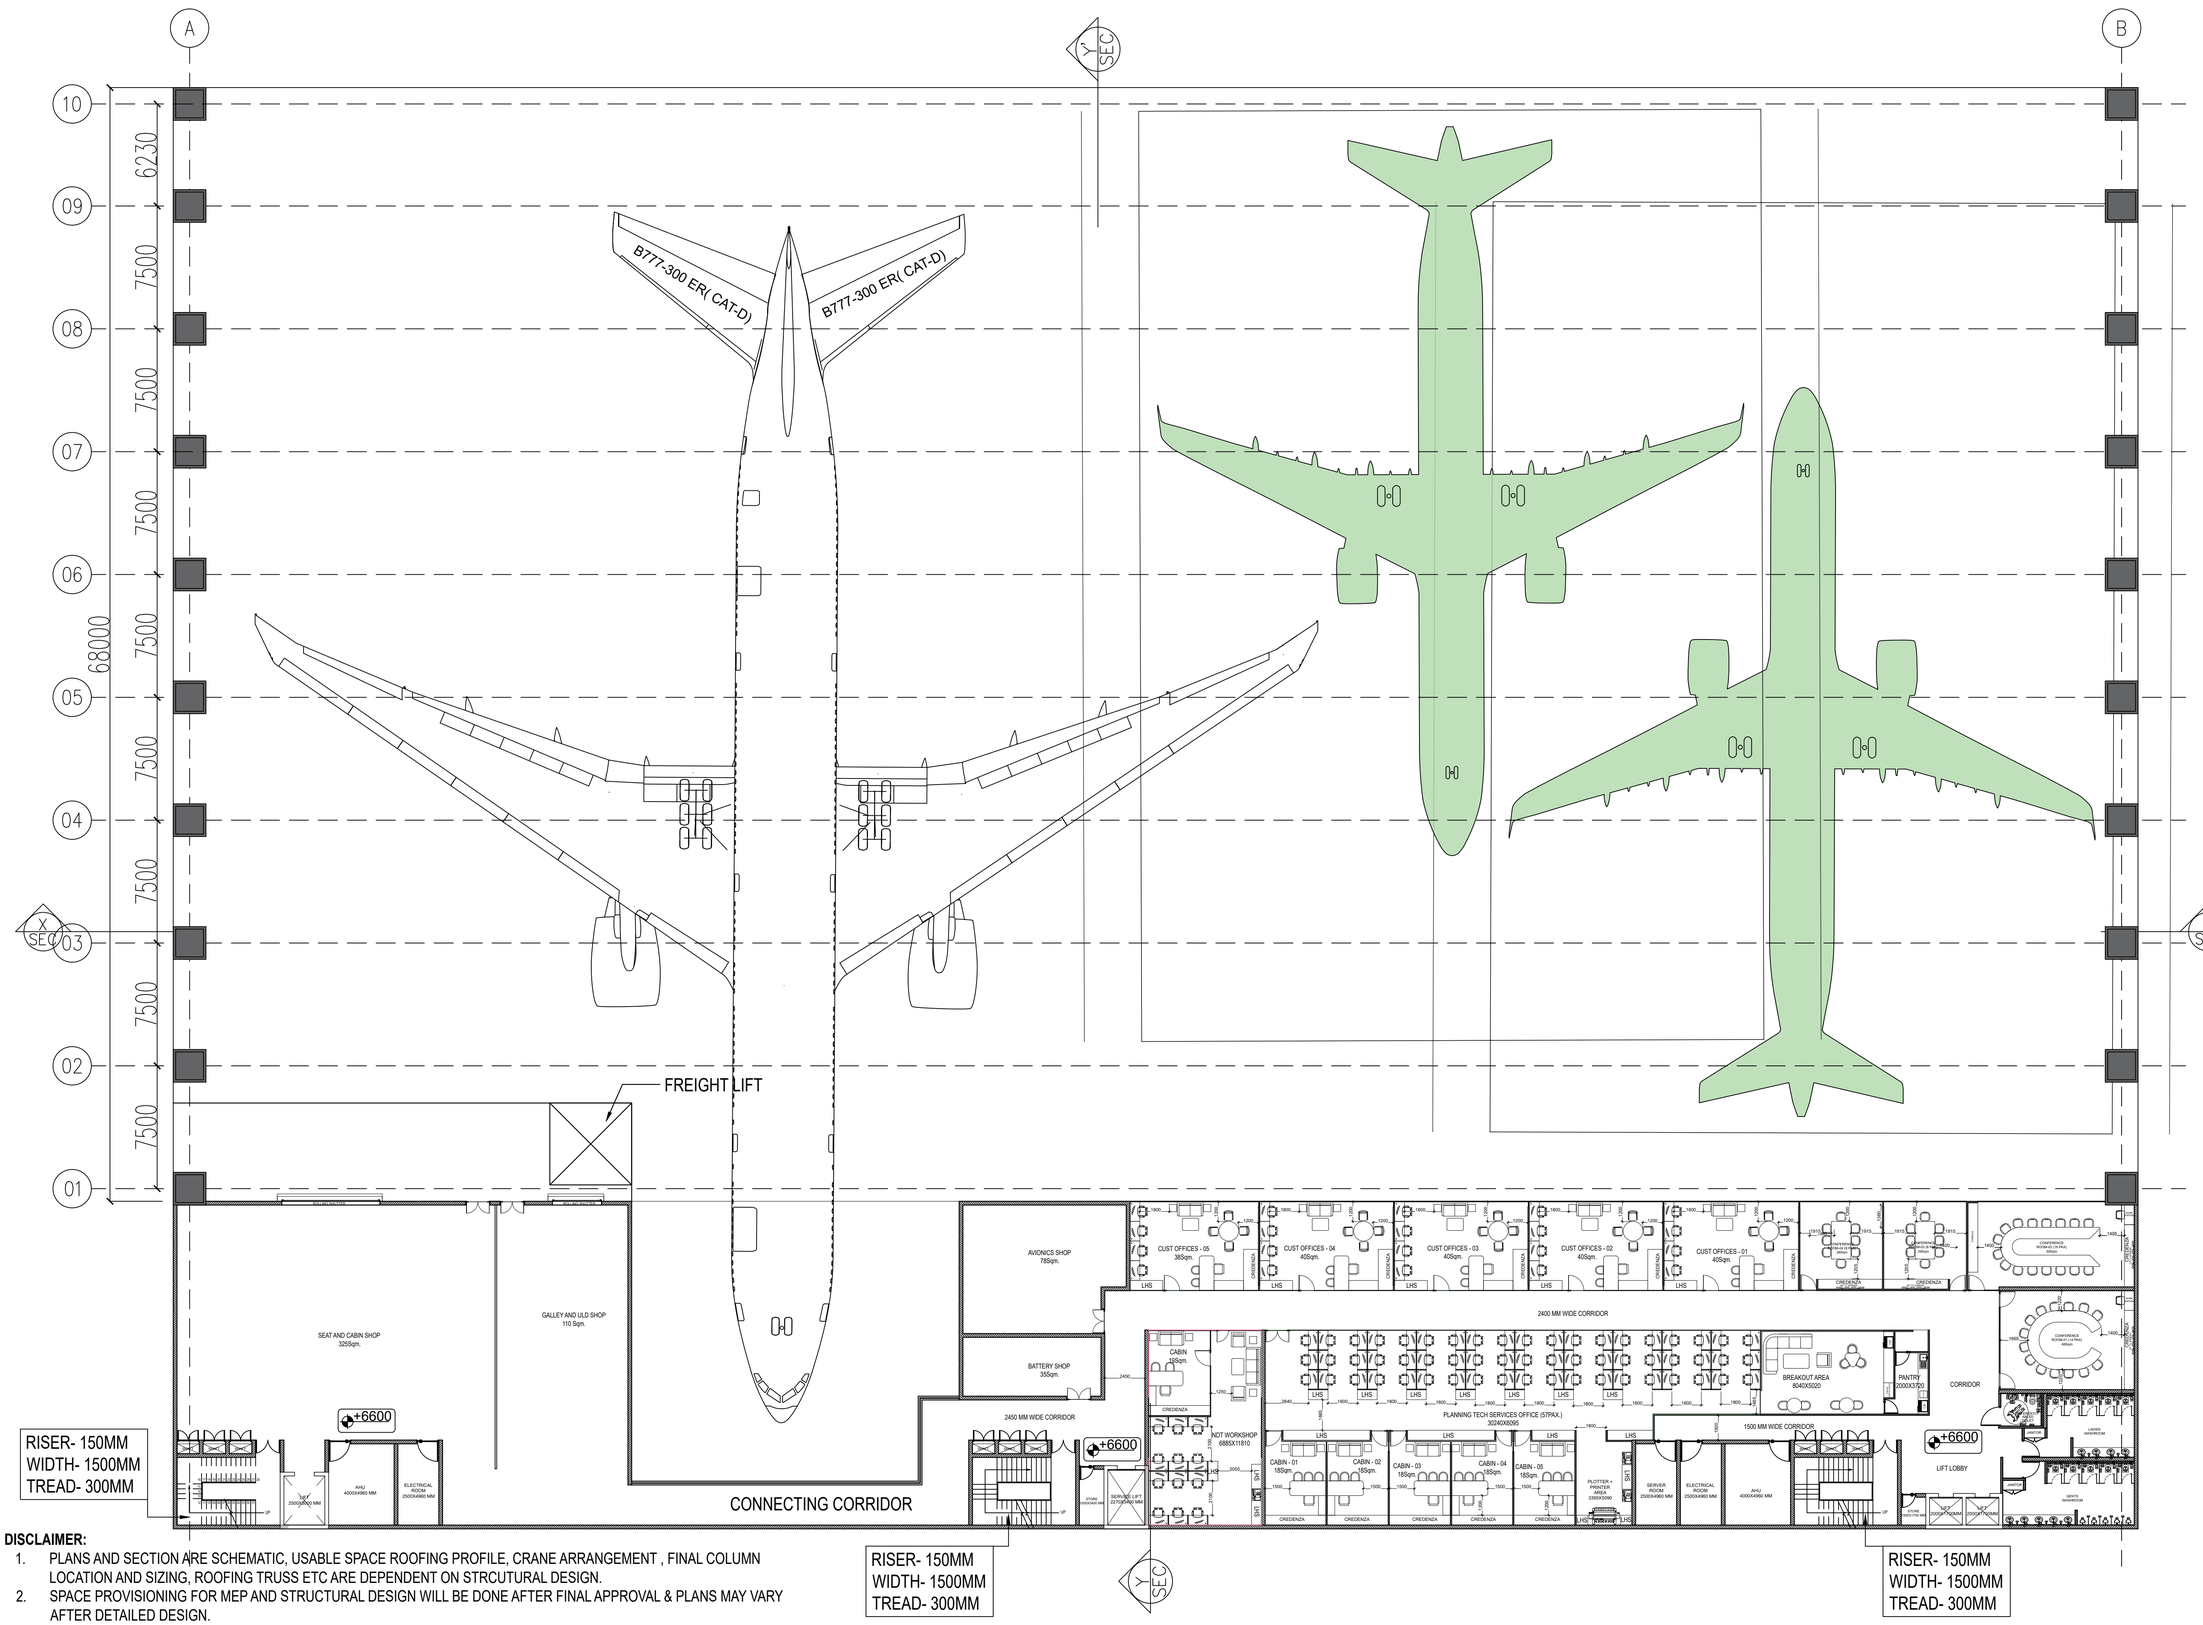

DISCLAIMER:

1. PLANS AND SECTION ARE SCHEMATIC, USABLE SPACE ROOFING PROFILE, CRANE ARRANGEMENT , FINAL COLUMN LOCATION AND SIZING, ROOFING TRUSS ETC ARE DEPENDENT ON STRCUTURAL DESIGN.
2. SPACE PROVISIONING FOR MEP AND STRUCTURAL DESIGN WILL BE DONE AFTER FINAL APPROVAL & PLANS MAY VARY AFTER DETAILED DESIGN.
3. DESIGN OF PEB STRUCTURE WILL GOVERN FINAL LAYOUTS AND SPACE PLANNING
4. OCCUPIED FUNCTIONS SUBJECT TO STATUTORY APPROVALS.
5. FINAL SPAN OF HANGAR WILL BE DEPENDENT ON FINAL ROOFING PROFILE AND STRUCTURAL DESIGN.

NOTES:

1. ALL DIMENSIONS ARE IN MILLIMETER
2. ANY REUSE OF EXISTING MATERIAL TO BE CO-ORDINATED DURING FINAL DESIGN.
3. ANY MEP DESIGN TO BE CO-ORDINATED DURING FINAL DESIGN.
4. THIS DRAWING IS NOT TO BE SCALED.
5. ANY DISCREPENCIES TO BE BROUGHT TO THE NOTICE OF THE ARCHITECTS.

FOR APPROVAL

PROJECT:
SARDAR VALLABHBHAI PATEL INTERNATIONAL AIRPORT T1 & T2 ENHANCEMENT

CLIENT:
adani
ADANI AHMEDABAD INTERNATIONAL AIRPORT LTD.

CONSULTANT : ARCHITECTURE & DESIGN

inCUBIS BUILTENVIRONMENTSINDUSTRIALDESIGN
inCUBIS CONSULTANTS (India) Private Limited
804-806, Emaar Palm Square, Sector-66,Golf Course Extension, Gurugram - 122102, India.
Telephones +91-124 451 8750 email - incubis@incubis.net www.incubis.net

REVISIONS

REF.	DATE	DESCRIPTION

PROJECT: **SARDAR VALLABHBHAI PATEL INTERNATIONAL AIRPORT T1 & T2 ENHANCEMENT**

STATUS: FOR APPROVAL

DRAWING TITLE: MRO FIRST FLOOR LAYOUT

JOB No. NH8 SCALE: --

	NAME	SIGN	DATE
DSGN			
DRWN	NA		
CHKD	VD		
APPD	AKG		


SIZE: @ A3

NORTH

DRAWING No. 2023/INC/AIA.A/MRO/003 REV: R0

RELEASED FOR

☐ INFORMATION ☒ APPROVAL ☐ TENDER ☐ CONSTRUCTION ☐ AS BUILT

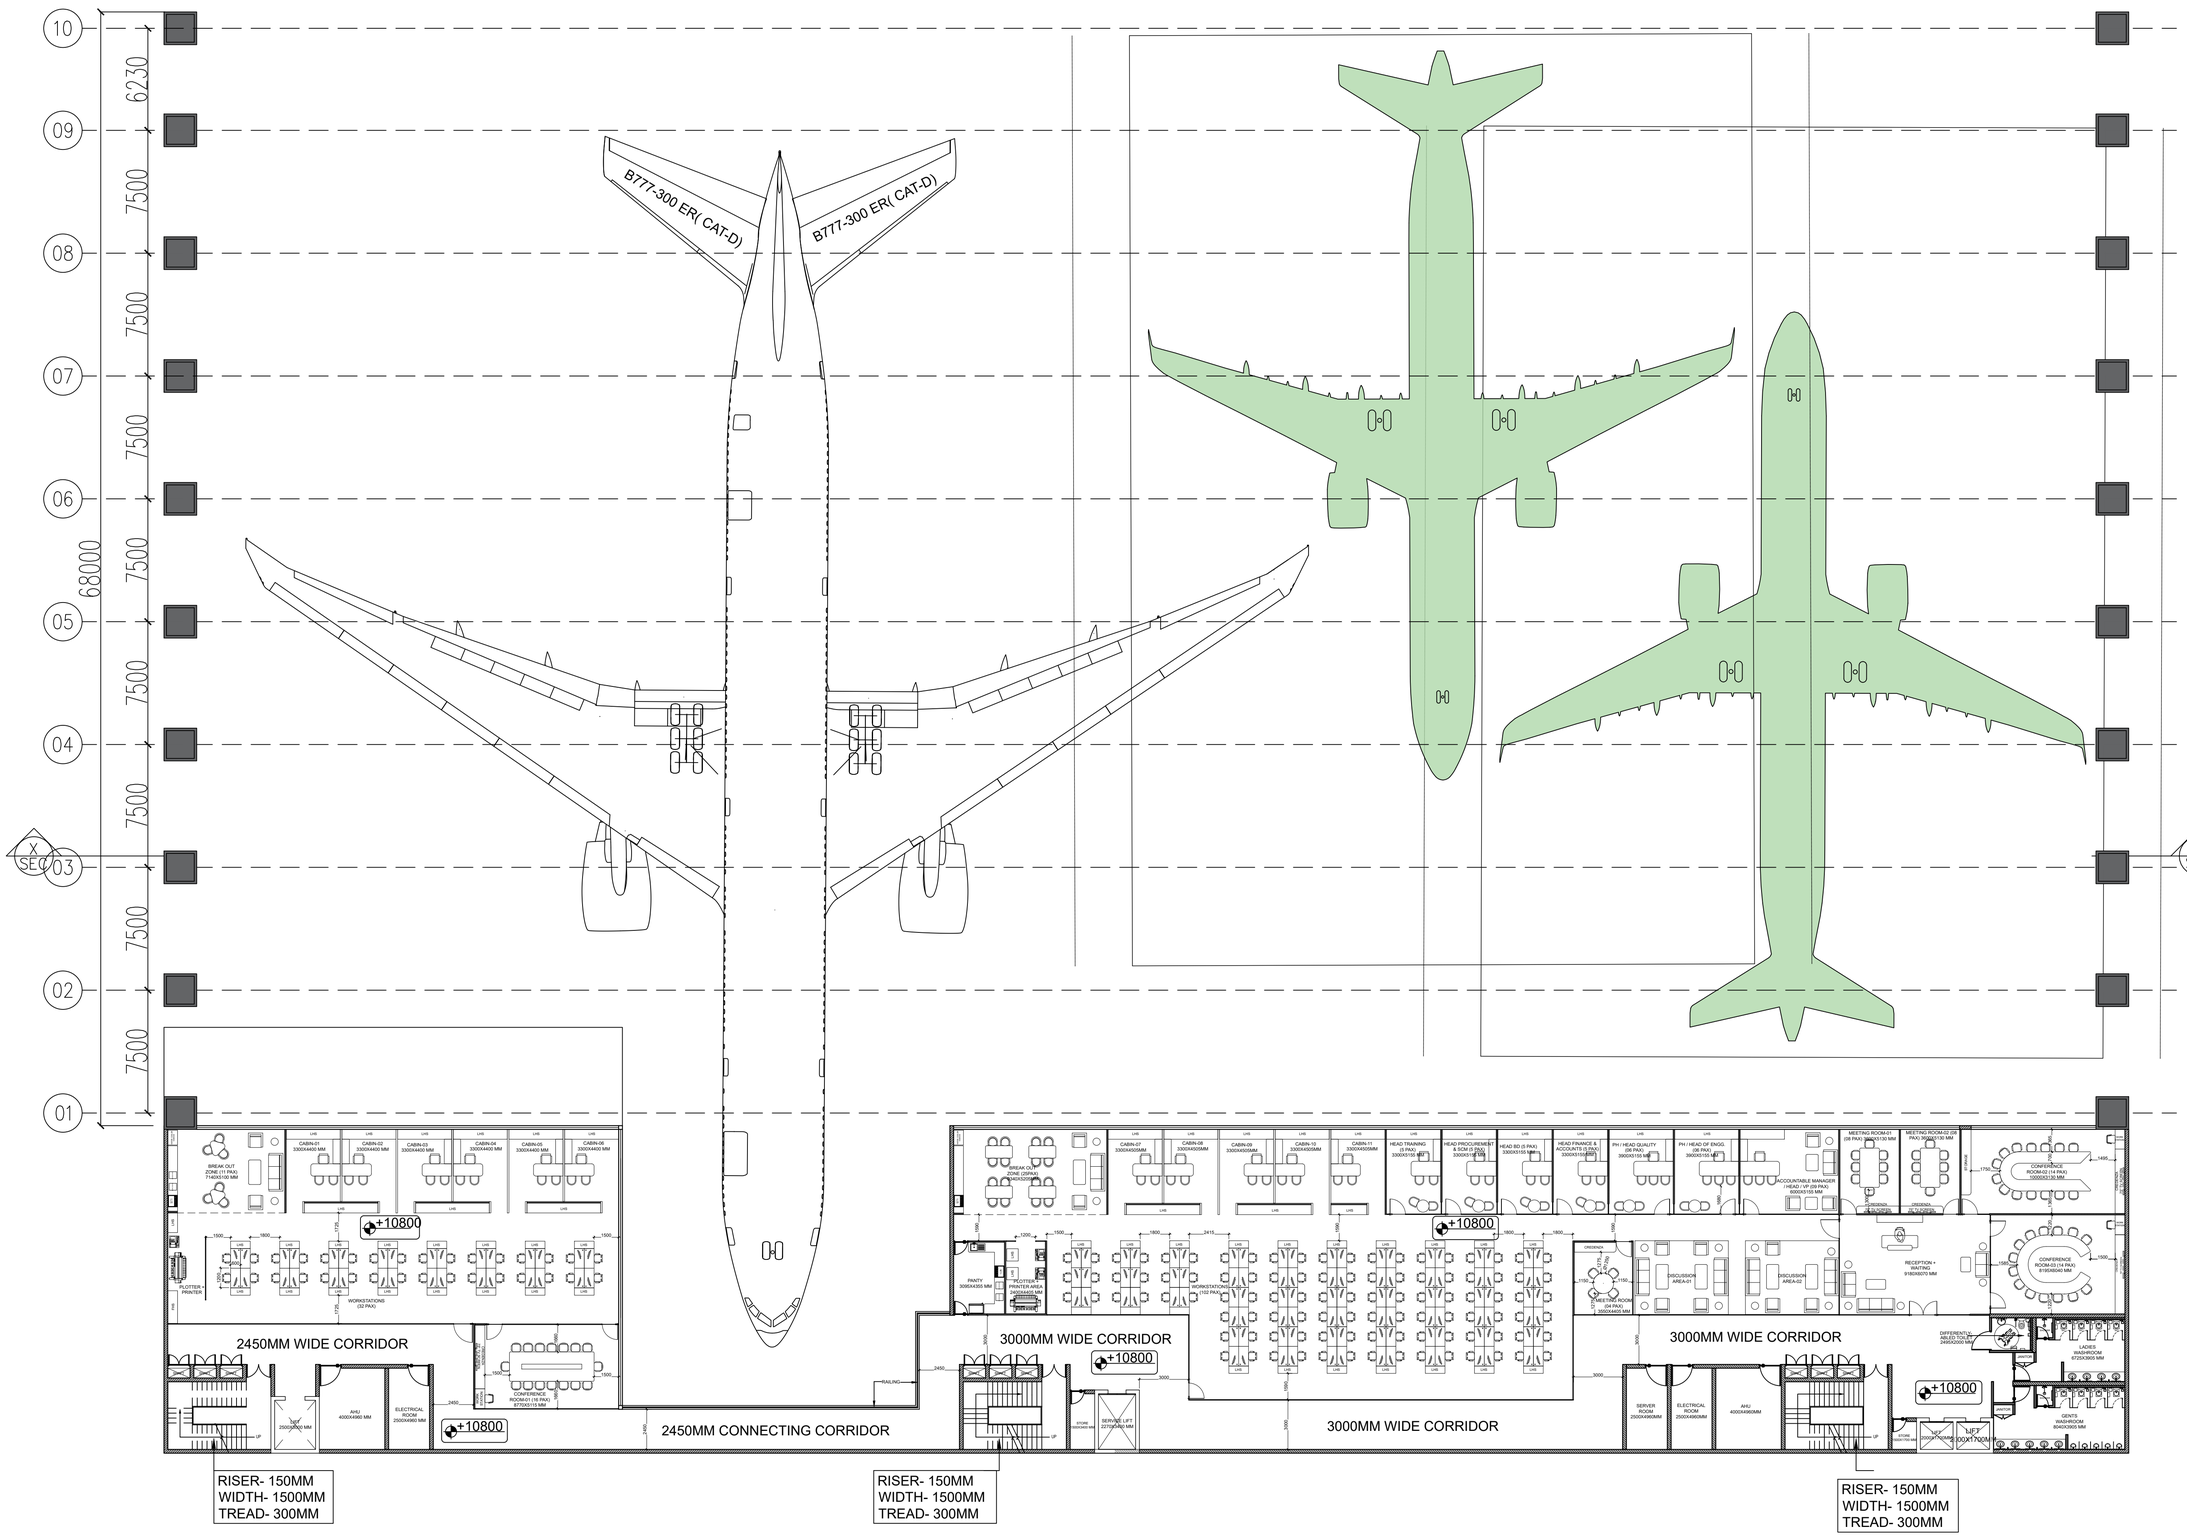

DISCLAIMER:

1. PLANS AND SECTION ARE SCHEMATIC, USABLE SPACE ROOFING PROFILE, CRANE ARRANGEMENT , FINAL COLUMN LOCATION AND SIZING, ROOFING TRUSS ETC ARE DEPENDENT ON STRCUTURAL DESIGN.
2. SPACE PROVISIONING FOR MEP AND STRUCTURAL DESIGN WILL BE DONE AFTER FINAL APPROVAL & PLANS MAY VARY AFTER DETAILED DESIGN.
3. DESIGN OF PEB STRUCTURE WILL GOVERN FINAL LAYOUTS AND SPACE PLANNING
4. OCCUPIED FUNCTIONS SUBJECT TO STATUTORY APPROVALS.
5. FINAL SPAN OF HANGAR WILL BE DEPENDENT ON FINAL ROOFING PROFILE AND STRUCTURAL DESIGN.

NOTES:

1. ALL DIMENSIONS ARE IN MILLIMETER
2. ANY REUSE OF EXISTING MATERIAL TO BE CO-ORDINATED DURING FINAL DESIGN.
3. ANY MEP DESIGN TO BE CO-ORDINATED DURING FINAL DESIGN.
4. THIS DRAWING IS NOT TO BE SCALED.
5. ANY DISCREPENCIES TO BE BROUGHT TO THE NOTICE OF THE ARCHITECTS.

FOR APPROVAL

PROJECT:
SARDAR VALLABHBHAI PATEL INTERNATIONAL AIRPORT
T1 & T2 ENHANCEMENT

CLIENT:
adani
ADANI AHMEDABAD INTERNATIONAL AIRPORT LTD.

CONSULTANT : ARCHITECTURE & DESIGN

incubis BUILT ENVIRONMENT SOLUTIONS INDUSTRIAL DESIGN
incubis CONSULTANTS (India) Private Limited
804-806, Emaar Palm Square, Sector-66,Golf Course Extension, Gurugram - 122102, India.
Telephones +91-124 451 8750 email - incubis@incubis.net www.incubis.net

REVISIONS

REF.	DATE	DESCRIPTION

PROJECT: SARDAR VALLABHBHAI PATEL INTERNATIONAL AIRPORT T1 & T2 ENHANCEMENT

STATUS: FOR APPROVAL

DRAWING TITLE: MRO SECOND FLOOR LAYOUT


JOB No. NH8 SCALE: --

	NAME	SIGN	DATE	SIZE: @ A3
DSGN				NORTH
DRWN	NA			
CHKD	VD			
APPD	AKG			

DRAWING No. 2023/INC/AIA.A/MRO/004 REV: R9

RELEASED FOR

☐ INFORMATION ☒ APPROVAL ☐ TENDER ☐ CONSTRUCTION ☐ AS BUILT

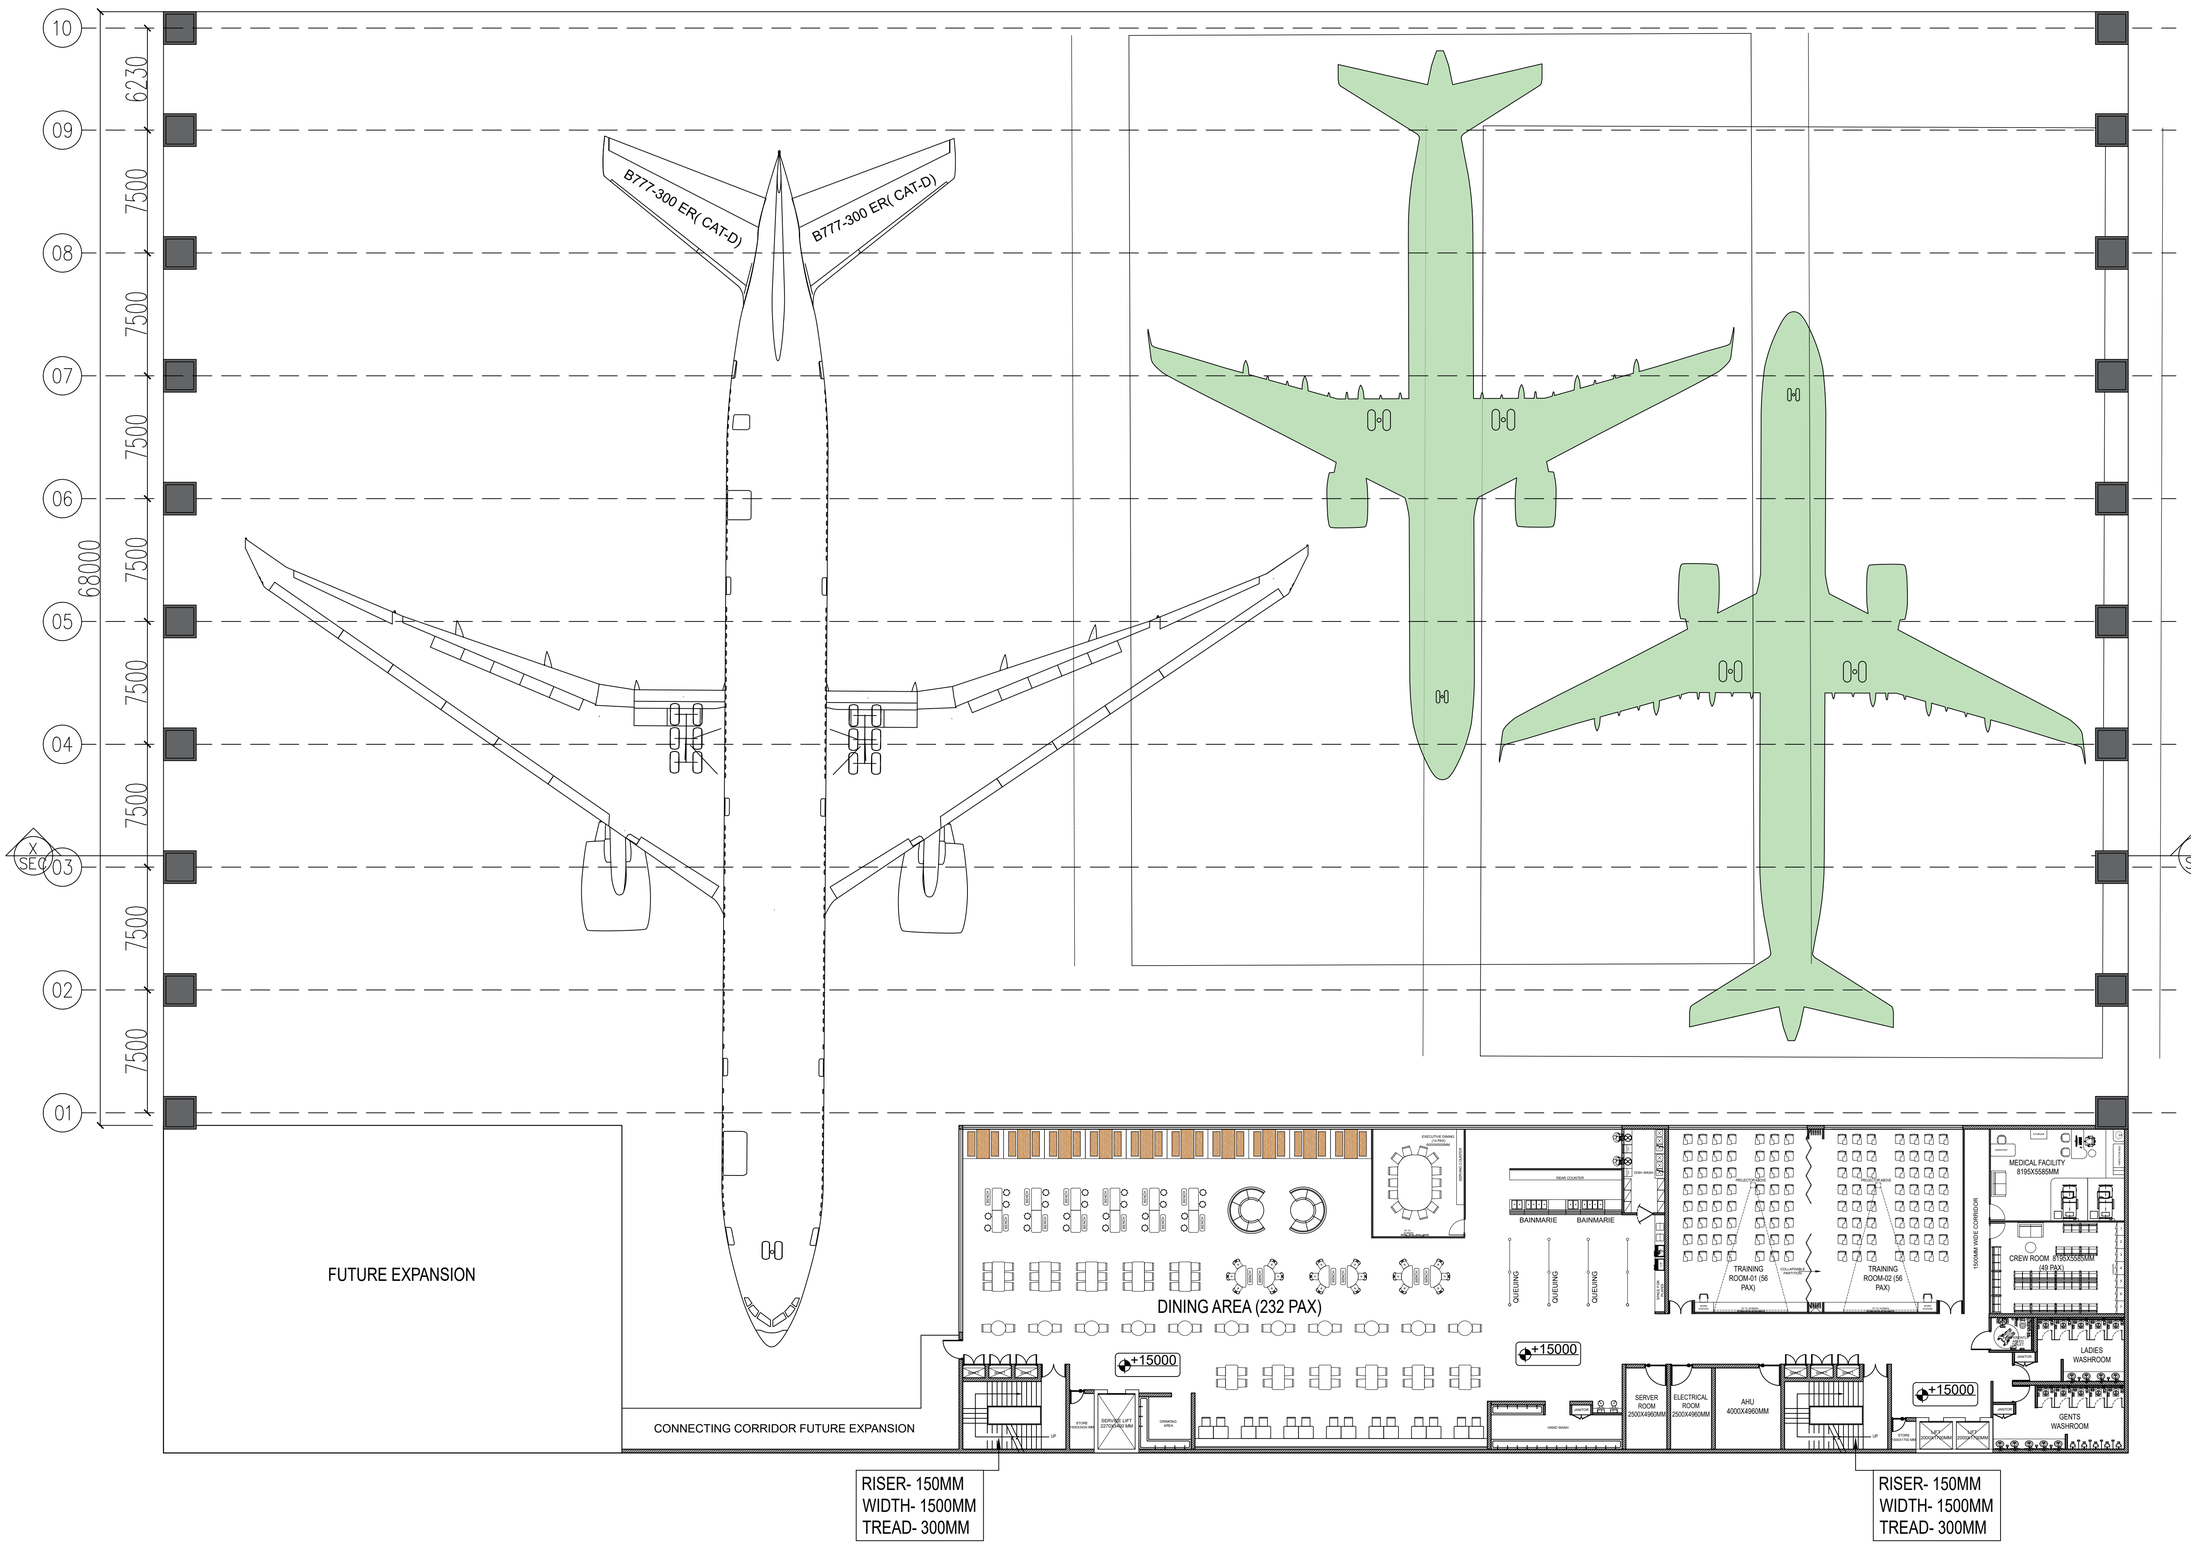

NOTES:

1. ALL DIMENSIONS ARE IN MILLIMETER
2. ANY REUSE OF EXISTING MATERIAL TO BE CO-ORDINATED DURING FINAL DESIGN.
3. ANY MEP DESIGN TO BE CO-ORDINATED DURING FINAL DESIGN.
4. THIS DRAWING IS NOT TO BE SCALED.
5. ANY DISCREPENCIES TO BE BROUGHT TO THE NOTICE OF THE ARCHITECTS.

FOR APPROVAL

PROJECT:
SARDAR VALLABHBHAI PATEL INTERNATIONAL AIRPORT
T1 & T2 ENHANCEMENT

CLIENT:
adani
ADANI AHMEDABAD INTERNATIONAL AIRPORT LTD.

CONSULTANT : ARCHITECTURE & DESIGN

mCUBIS BUILT ENVIRONMENT'S INDUSTRIAL DESIGN
mCUBIS CONSULTANTS (India) Private Limited
804-806, Emaar Palm Square, Sector-66,Golf Course Extension, Gurugram - 122102, India.
Telephones +91-124 451 8750 email - incubis@incubis.net www.incubis.net

REVISIONS

REF.	DATE	DESCRIPTION

PROJECT: SARDAR VALLABHBHAI PATEL INTERNATIONAL AIRPORT T1 & T2 ENHANCEMENT

STATUS: FOR APPROVAL

DRAWING TITLE: MRO THIRD FLOOR LAYOUT

JOB No. NH8 SCALE: --

	NAME	SIGN	DATE
SIZE: @ A3			
DSGN			
DRWN	NA		
CHKD	VD		
APPD	AKG		

NORTH


DRAWING No. 2023/INC/AIA.A/MRO/005 REV: R0

RELEASED FOR


☐ INFORMATION ☒ APPROVAL ☐ TENDER ☐ CONSTRUCTION ☐ AS BUILT

DISCLAIMER:

1. PLANS AND SECTION ARE SCHEMATIC, USABLE SPACE ROOFING PROFILE, CRANE ARRANGEMENT , FINAL COLUMN LOCATION AND SIZING, ROOFING TRUSS ETC ARE DEPENDENT ON STRCUTURAL DESIGN.
2. SPACE PROVISIONING FOR MEP AND STRUCTURAL DESIGN WILL BE DONE AFTER FINAL APPROVAL & PLANS MAY VARY AFTER DETAILED DESIGN.
3. DESIGN OF PEB STRUCTURE WILL GOVERN FINAL LAYOUTS AND SPACE PLANNING
4. OCCUPIED FUNCTIONS SUBJECT TO STATUTORY APPROVALS.
5. FINAL SPAN OF HANGAR WILL BE DEPENDENT ON FINAL ROOFING PROFILE AND STRUCTURAL DESIGN.

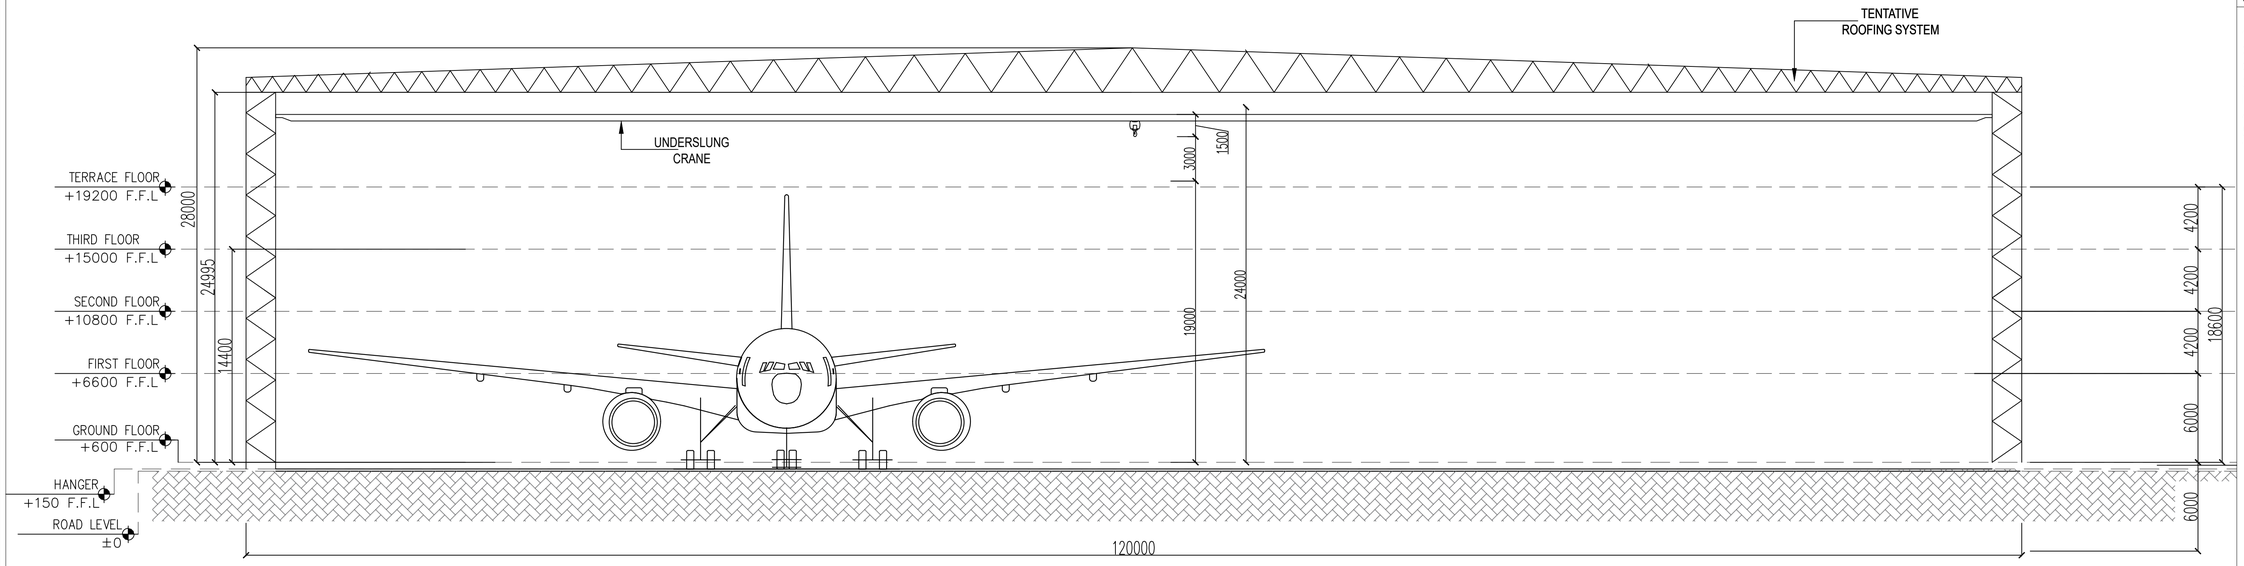

SCHEMATIC SECTION
X-X'

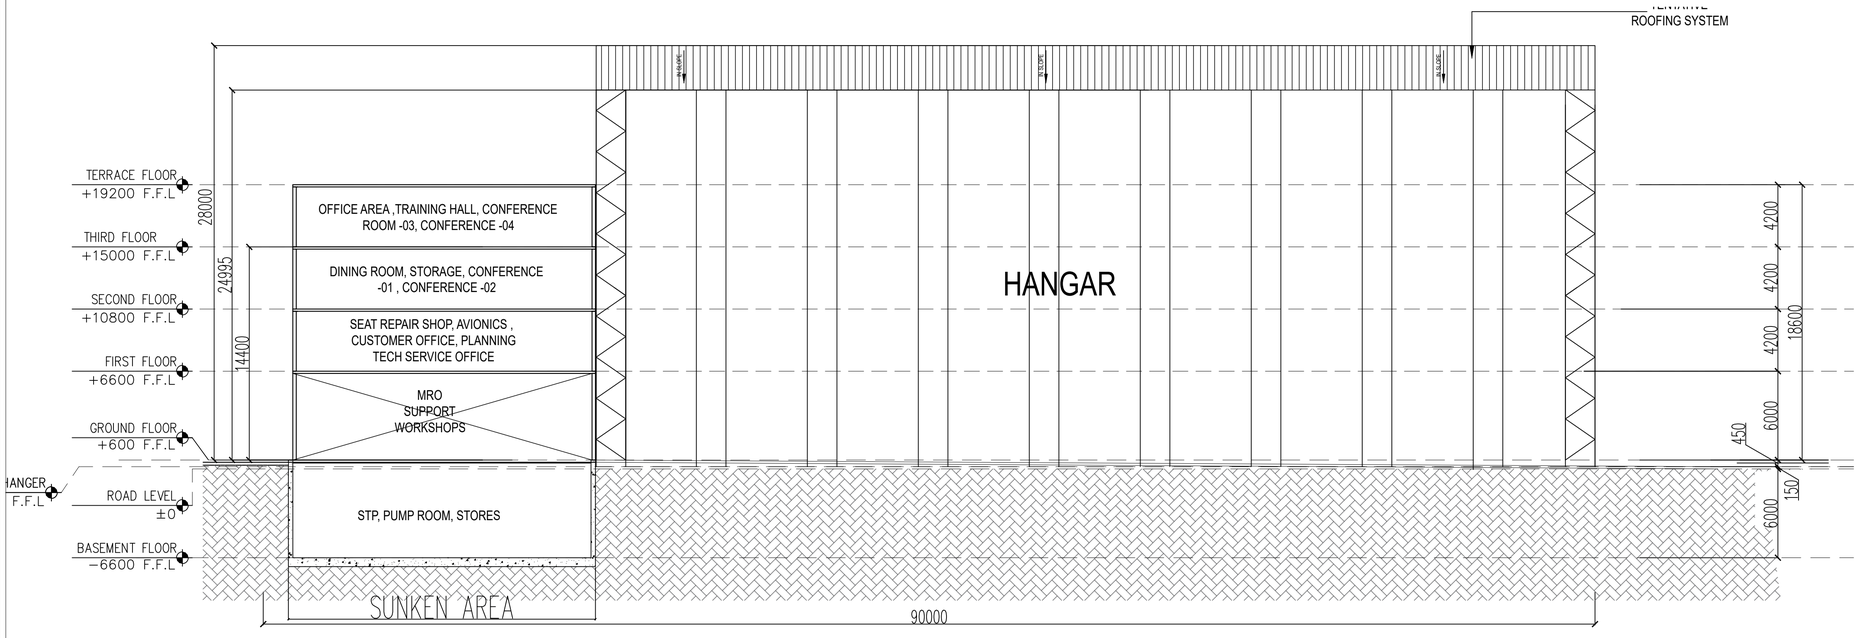

SCHEMATIC SECTION

DISCLAIMER:

1. PLANS AND SECTION ARE SCHEMATIC, USABLE SPACE ROOFING PROFILE, CRANE ARRANGEMENT , FINAL COLUMN LOCATION AND SIZING, ROOFING TRUSS ETC ARE DEPENDENT ON STRCUTURAL DESIGN.
2. SPACE PROVISIONING FOR MEP AND STRUCTURAL DESIGN WILL BE DONE AFTER FINAL APPROVAL & PLANS MAY VARY AFTER DETAILED DESIGN.
3. DESIGN OF PEB STRUCTURE WILL GOVERN FINAL LAYOUTS AND SPACE PLANNING
4. OCCUPIED FUNCTIONS SUBJECT TO STATUTORY APPROVALS.
5. FINAL SPAN OF HANGAR WILL BE DEPENDENT ON FINAL ROOFING PROFILE AND STRUCTURAL DESIGN.

NOTES:

1. ALL DIMENSIONS ARE IN MILLIMETER
2. ANY REUSE OF EXISTING MATERIAL TO BE CO-ORDINATED DURING FINAL DESIGN.
3. ANY MEP DESIGN TO BE CO-ORDINATED DURING FINAL DESIGN.
4. THIS DRAWING IS NOT TO BE SCALED.
5. ANY DISCREPENCIES TO BE BROUGHT TO THE NOTICE OF THE ARCHITECTS.

FOR APPROVAL

PROJECT:
SARDAR VALLABHBHAI PATEL INTERNATIONAL AIRPORT
T1 & T2 ENHANCEMENT

CLIENT:
adani
ADANI AHMEDABAD INTERNATIONAL AIRPORT LTD.

CONSULTANT : ARCHITECTURE & DESIGN

incubis
BUILT ENVIRONMENT | INDUSTRIAL DESIGN
incubis CONSULTANTS (India) Private Limited
804-806, Emaar Palm Square, Sector-66,Golf Course Extension, Gurugram - 122102, India.
Telephones +91-124 451 8750 email - incubis@incubis.net www.incubis.net

REVISIONS

REF.	DATE	DESCRIPTION

PROJECT: **SARDAR VALLABHBHAI PATEL INTERNATIONAL AIRPORT T1 & T2 ENHANCEMENT**

STATUS: FOR APPROVAL

DRAWING TITLE: MRO-HANGAR BUILDING SECTIONS

JOB No. NH8 | SCALE: --

	NAME	SIGN	DATE
DSGN			
DRWN	NA		
CHKD	VD		
APPD	AKG		

SIZE: @ A3

NORTH

DRAWING No. 2023/INC/AIA.A/MRO/006 | REV: R0

RELEASED FOR

☐ INFORMATION ☒ APPROVAL ☐ TENDER ☐ CONSTRUCTION ☐ AS BUILT