




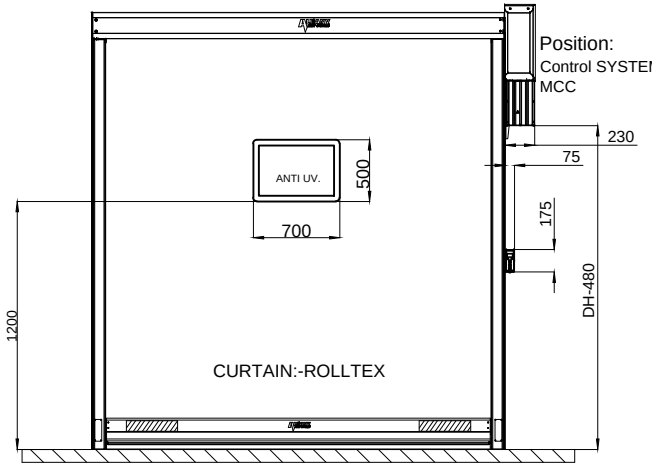


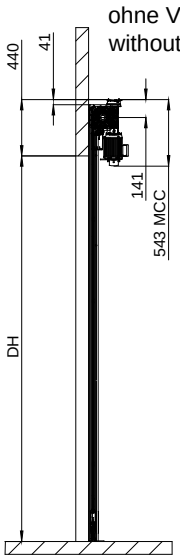

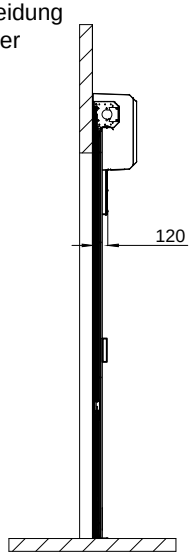

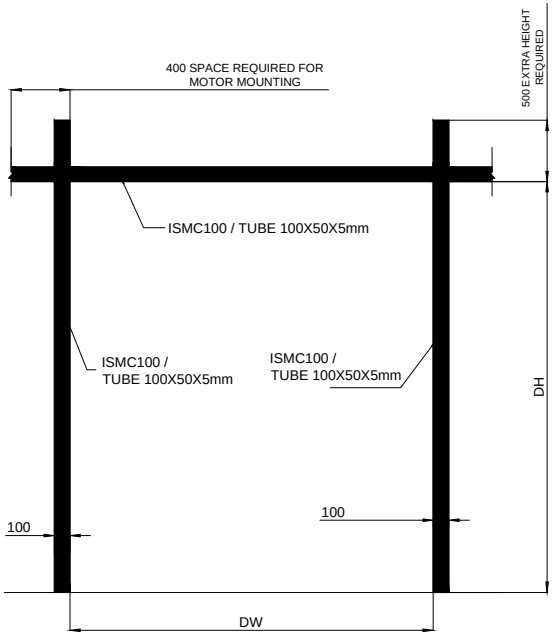

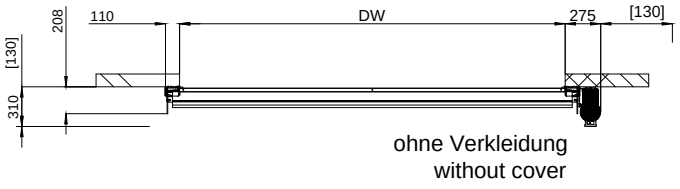

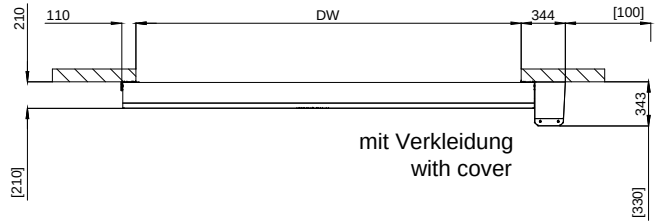

RAL : 5002 BLUE

Tolerance ±3 mm (for all dimensions)

Dimensions in [ ] ==> clearance for installation

CLEAR WIDTH(DW)	CLEAR HEIGHT(DH)	QTY
4000mm	2500mm	01 NOS

NOTE : ALL CIVIL & STRUCTURAL WORK WILL BE IN CLIENT SCOPE.

This drawing & design is the property of NIHVA TECHNOLOGIES. Not to be sold or copied to any other concern.

TITLE: HIGH SPEED DOOR RP300 & STRUCTURE

	NAME	SIGN	DATE
DRAWN	P.V.A		06.09.19
CHECK	V.M.T		06.09.19
APPV'ED			

If any queries contact : design@nihva.com

ALL DIMENSION ARE IN mm

NIHVA TECHNOLOGIES PVT. LTD.
NIHVA TECHNOLOGIES PVT. LTD. PUNE
Tel : 020 66304033
Email:- info@nihva.com
Website:- www.nihva.com

CLIENT :-

PROJECT :-

LOCATION :- PUNE.

DWG. NO. :- NIHVA/19-20/VDR/152 REV.:-R01

SCALE: NTS | WT: | SHEET: 01 OF 01