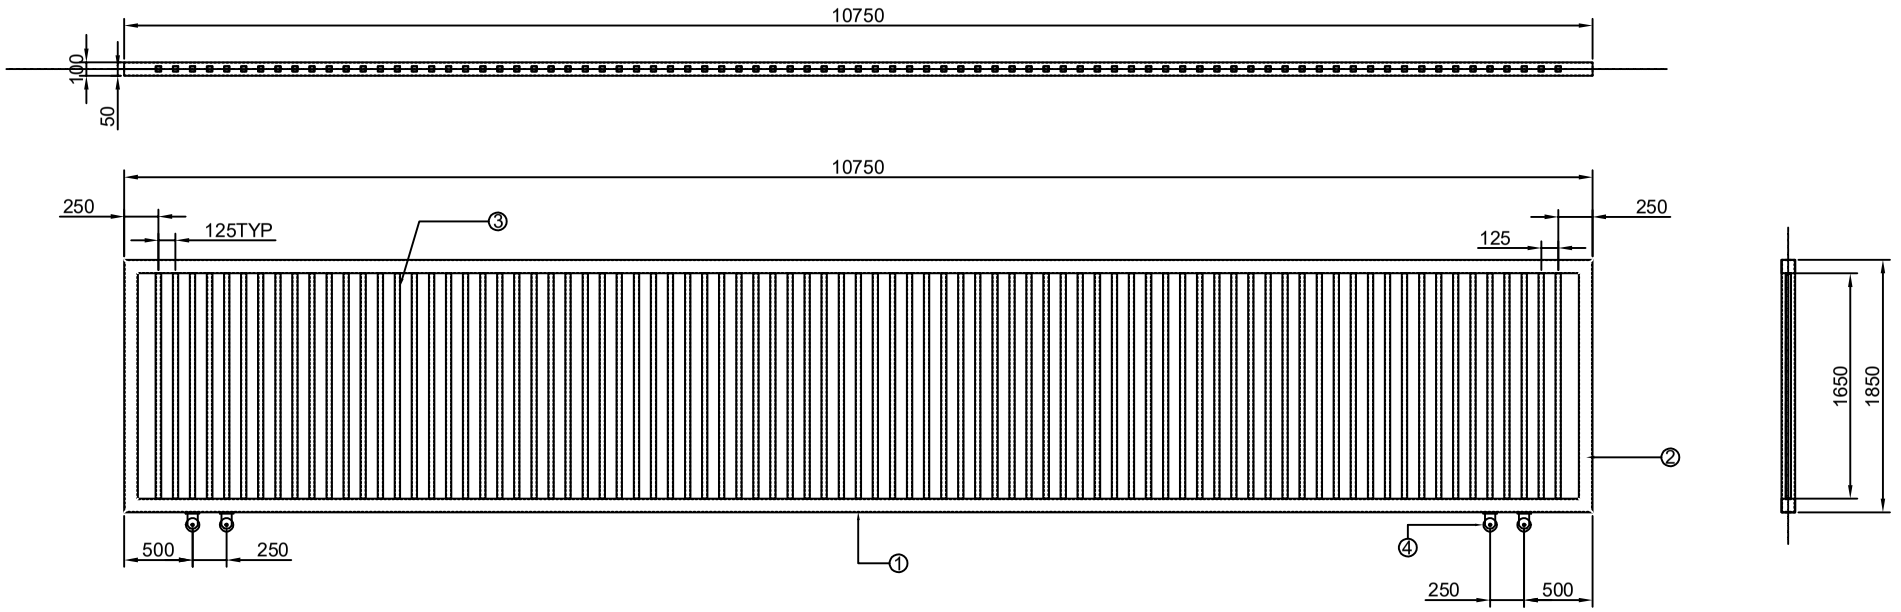


BOM			
SL NO.	DESCRIPTION	SPECIFICATION	QTY
1	MS SQ. TUBE	100X100X3.6X10750L	2NOS
2	MS SQ.TUBE	100X100X3.6X1850L	2NOS
3	MS SQ.TUBE	40X40X2.6X1650L	83NOS
4	WHEEL	4" STD WHEEL	4NOS
5	BRACKET	STD BKT	4NOS

This drawing & design is the property of NIHVA TECHNOLOGIES. Not to be sold or copied to any other concern.

TITLE:- MS Motorised Single Leaf Sliding Gate

NIHVA TECHNOLOGIES PVT. LTD.
NIHVA TECHNOLOGIES PVT. LTD. PUNE
Tel : 020 66304033
Email:- info@nihva.com
Website:- www.nihva.com

	NAME	DATE	SIGN
DRAWN	SUJATA.B	16/10/2021	
CHECK	G.PATIL	16/10/2021	
APPRD.	A.KURHADE	16/10/2021	

If any queries contact : design@nihva.com

ALL DIMENSION ARE IN mm

CLIENT - SCON PROJECTS

LOCATION -

PRODUCT - QTY:-01NO

DWG NO:-NIHVA\21-22\VDR\0251 REV- 0

SCALE: NTS SCALE:-- 1:1 SHEET: 01 OF 01

Rev No.	Revision	Date	Revised By