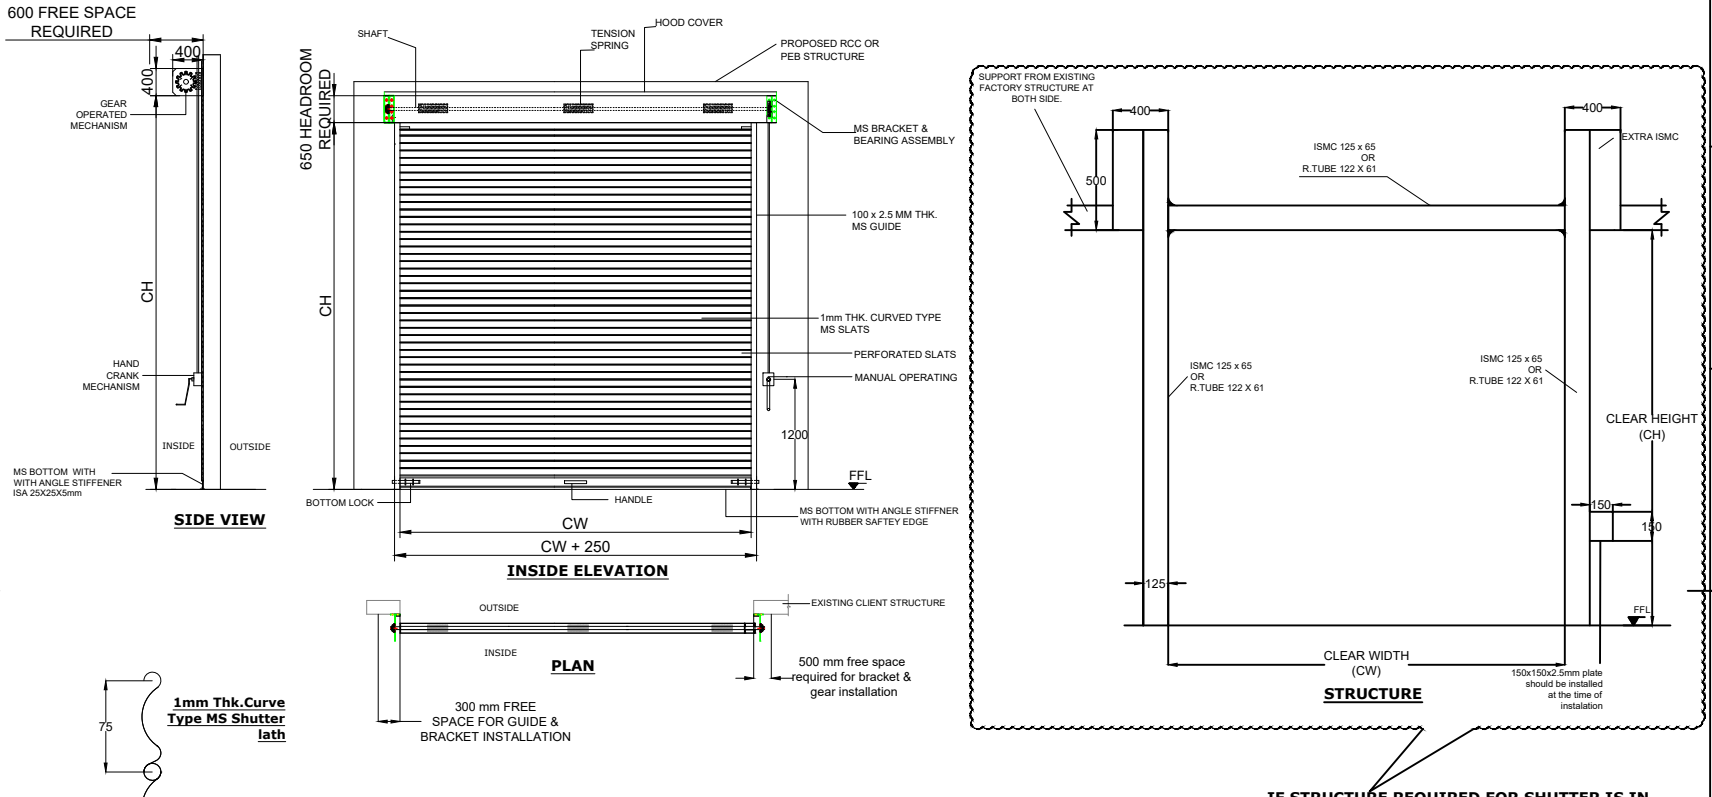


TOLERANCE - ±10mm

This drawing & design is the property of NIHVA TECHNOLOGIES. Not to be sold or copied to any other concern.

TITLE				
GEAR OPERATED ROLLING SHUTTER				
	NAME	SIGN	DATE	
DRAWN	B.S.		23.06.2025	
CHECK	V.T.		23.06.2025	
APPRD.	V.T.		23.06.2025	
If any queries contact : design@nihva.com				
ALL DIMENSION ARE IN mm				

NIHVA TECHNOLOGIES PVT. LTD.
NIHVA TECHNOLOGIES PVT. LTD. PUNE
Tel : 020 66304033
Website:- www.nihva.com
Email:- info@nihva.com

CLIENT - TATA COMMINS			
PROJECT -			
SITE LOCATION -			
DWG. NO. : NIHVA/21-22/VDR/020			REV- R00
SCALE: NTS	WT:		SHEET: 01 OF 01

SR NO	(CW) CLEAR WIDTH	(CH) CLEAR HEIGHT	QUANTITY
1	5000	4500	01 NO

NOTE-
1. ALL CIVIL WORK WILL BE CLIENT'S SCOPE.
2.IF STRUCTURE REQUIRED FOR SHUTTER IS IN CLIENT'S SCOPE.