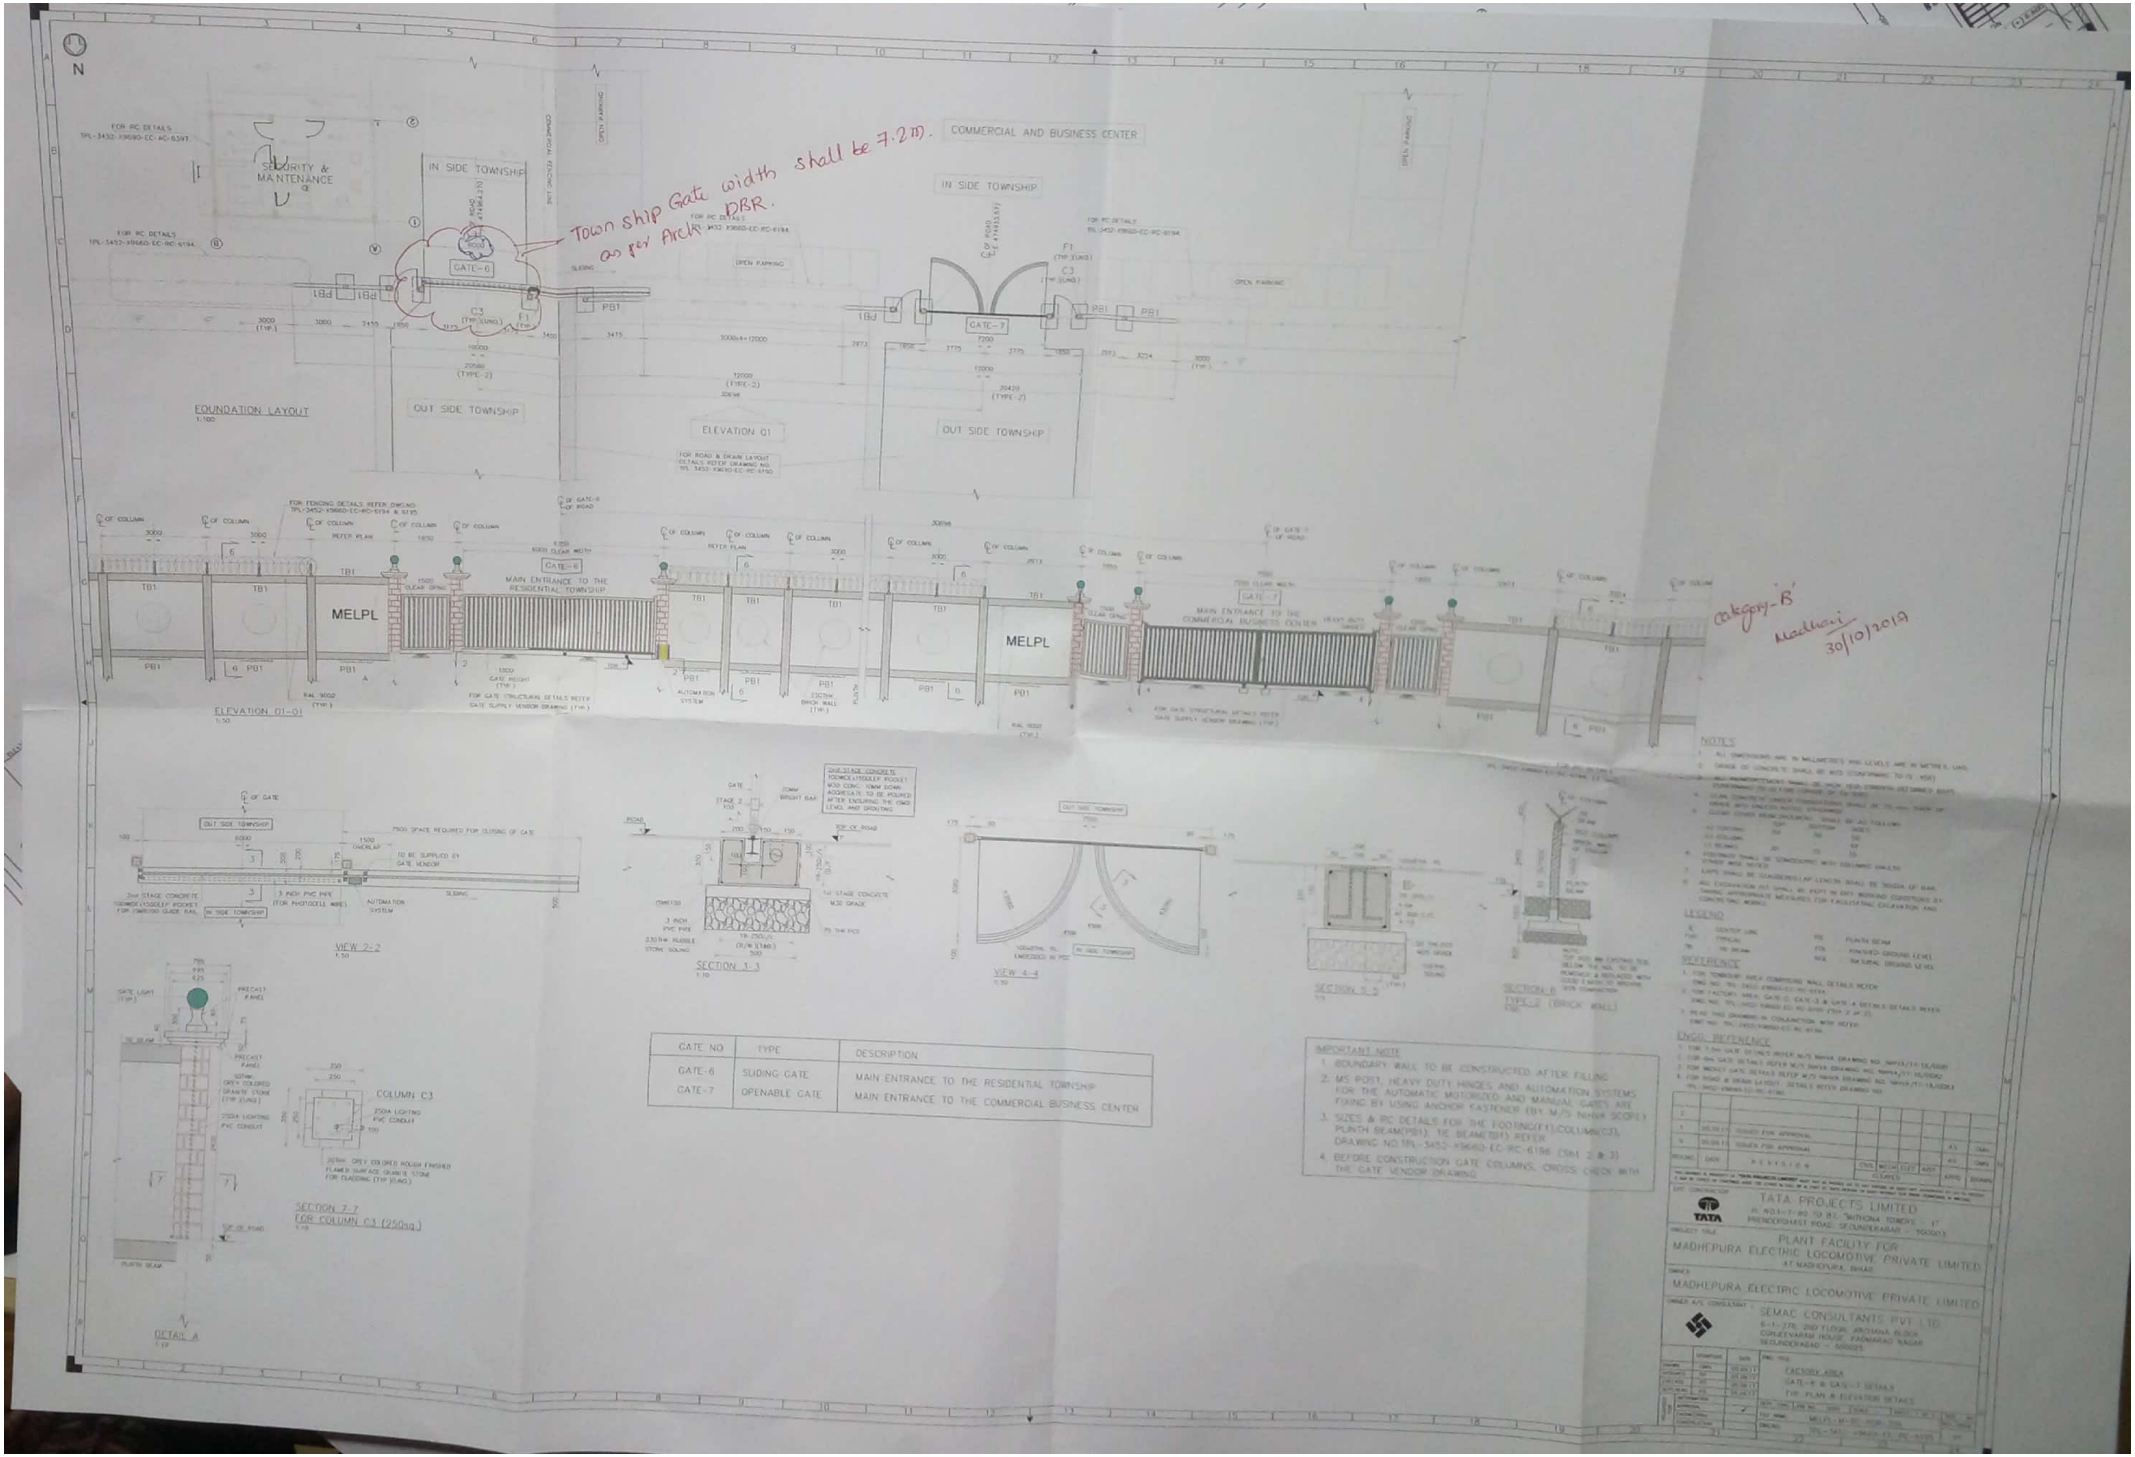



| GATE NO | TYPE | DESCRIPTION |
|---|---|---|
| GATE-6 | SLIDING GATE | MAIN ENTRANCE TO THE RESIDENTIAL TOWNSHIP |
| GATE-7 | OPENABLE GATE | MAIN ENTRANCE TO THE COMMERCIAL BUSINESS CENTER |

IMPORTANT NOTE
1. BOUNDARY WALL TO BE CONSTRUCTED AFTER FILLING.
2. MS POST, HEAVY DUTY HINGES AND AUTOMATION SYSTEMS FOR THE AUTOMATIC MOTORIZED AND MANUAL GATES ARE FIXING BY USING ANCHOR FASTENER (BY M/S NIHAR SCOPE)
3. SIZES & RC DETAILS FOR THE FOOTING(FT1),COLUMN(C3), PLINTH BEAM(PB1), TIE BEAM(TB1) REFER DRAWING NO.TPL-3452-X9660-EC-RC-6196 (SH-1 & 3)
4. BEFORE CONSTRUCTION GATE COLUMNS, CROSS CHECK WITH THE GATE VENDOR DRAWING.

NOTES
LEGEND
REFERENCE
ENGG. REFERENCE

TATA PROJECTS LIMITED
PLANT FACILITY FOR MADHEPURA ELECTRIC LOCOMOTIVE PRIVATE LIMITED AT MADHEPURA, BIHAR
MADHEPURA ELECTRIC LOCOMOTIVE PRIVATE LIMITED
SEMAC CONSULTANTS PVT. LTD.
FACTORY AREA
GATE-6 & GATE-7 DETAILS
TYP. PLAN & ELEVATION DETAILS

Scanned by CamScanner

# SEMAC CONSULTANTS PRIVATE LIMITED

General Consultant

**Ref : TPL-340052-MELPL-ENGG-005** **TRANSMITTAL**

| To | From |
|---|---|
| TATA PROJECTS LIMITED. Secunderabad -500003, India | **Semac CONSULTANTS PVT. LTD.**<br>6-1-276, 2nd Floor, Conjeevaram House,<br>Padmarao Nagar, Hyderabad - 500 025.<br>Phone: 040-27508968; Fax 040-27507733<br>Email: semachyd@rediffmail.com |

**Kind Attn:- Sourav Ghosh**

| **Project :** PROPOSED PLANT & RESIDENTIAL FACILITY FOR MADHEPURA ELECTRIC LOCOMOTIVE PRIVATE LIMITED AT MADHEPURA, BIHAR. | **Date : 30.OCT.17** |
|---|---|
| **Job Description:- H-15-16/004** | |

[ ] Soft Copies [√] Hard Copies

| S.No. | Drawing nos | Rev. No. | Category | Title |
|---|---|---|---|---|
| 1 | | R0 | B | compliance report for fire drill assembly |
| 2 | TPL-3452-X9690-EC-RC-6195<br>Sheet 1 of 2 | R1 | B | Gate - 6 & Gate - 7 details<br>Typ. Plan & elevation details |

| | | |
|---|---|---|
| | Notice of No objection | Cat C |
| √ | Notice of No objection with comments | Cat B |
| | Rejected for resubmission | Cat A |

**Project Coordinator/Designer**

Scanned by CamScanner