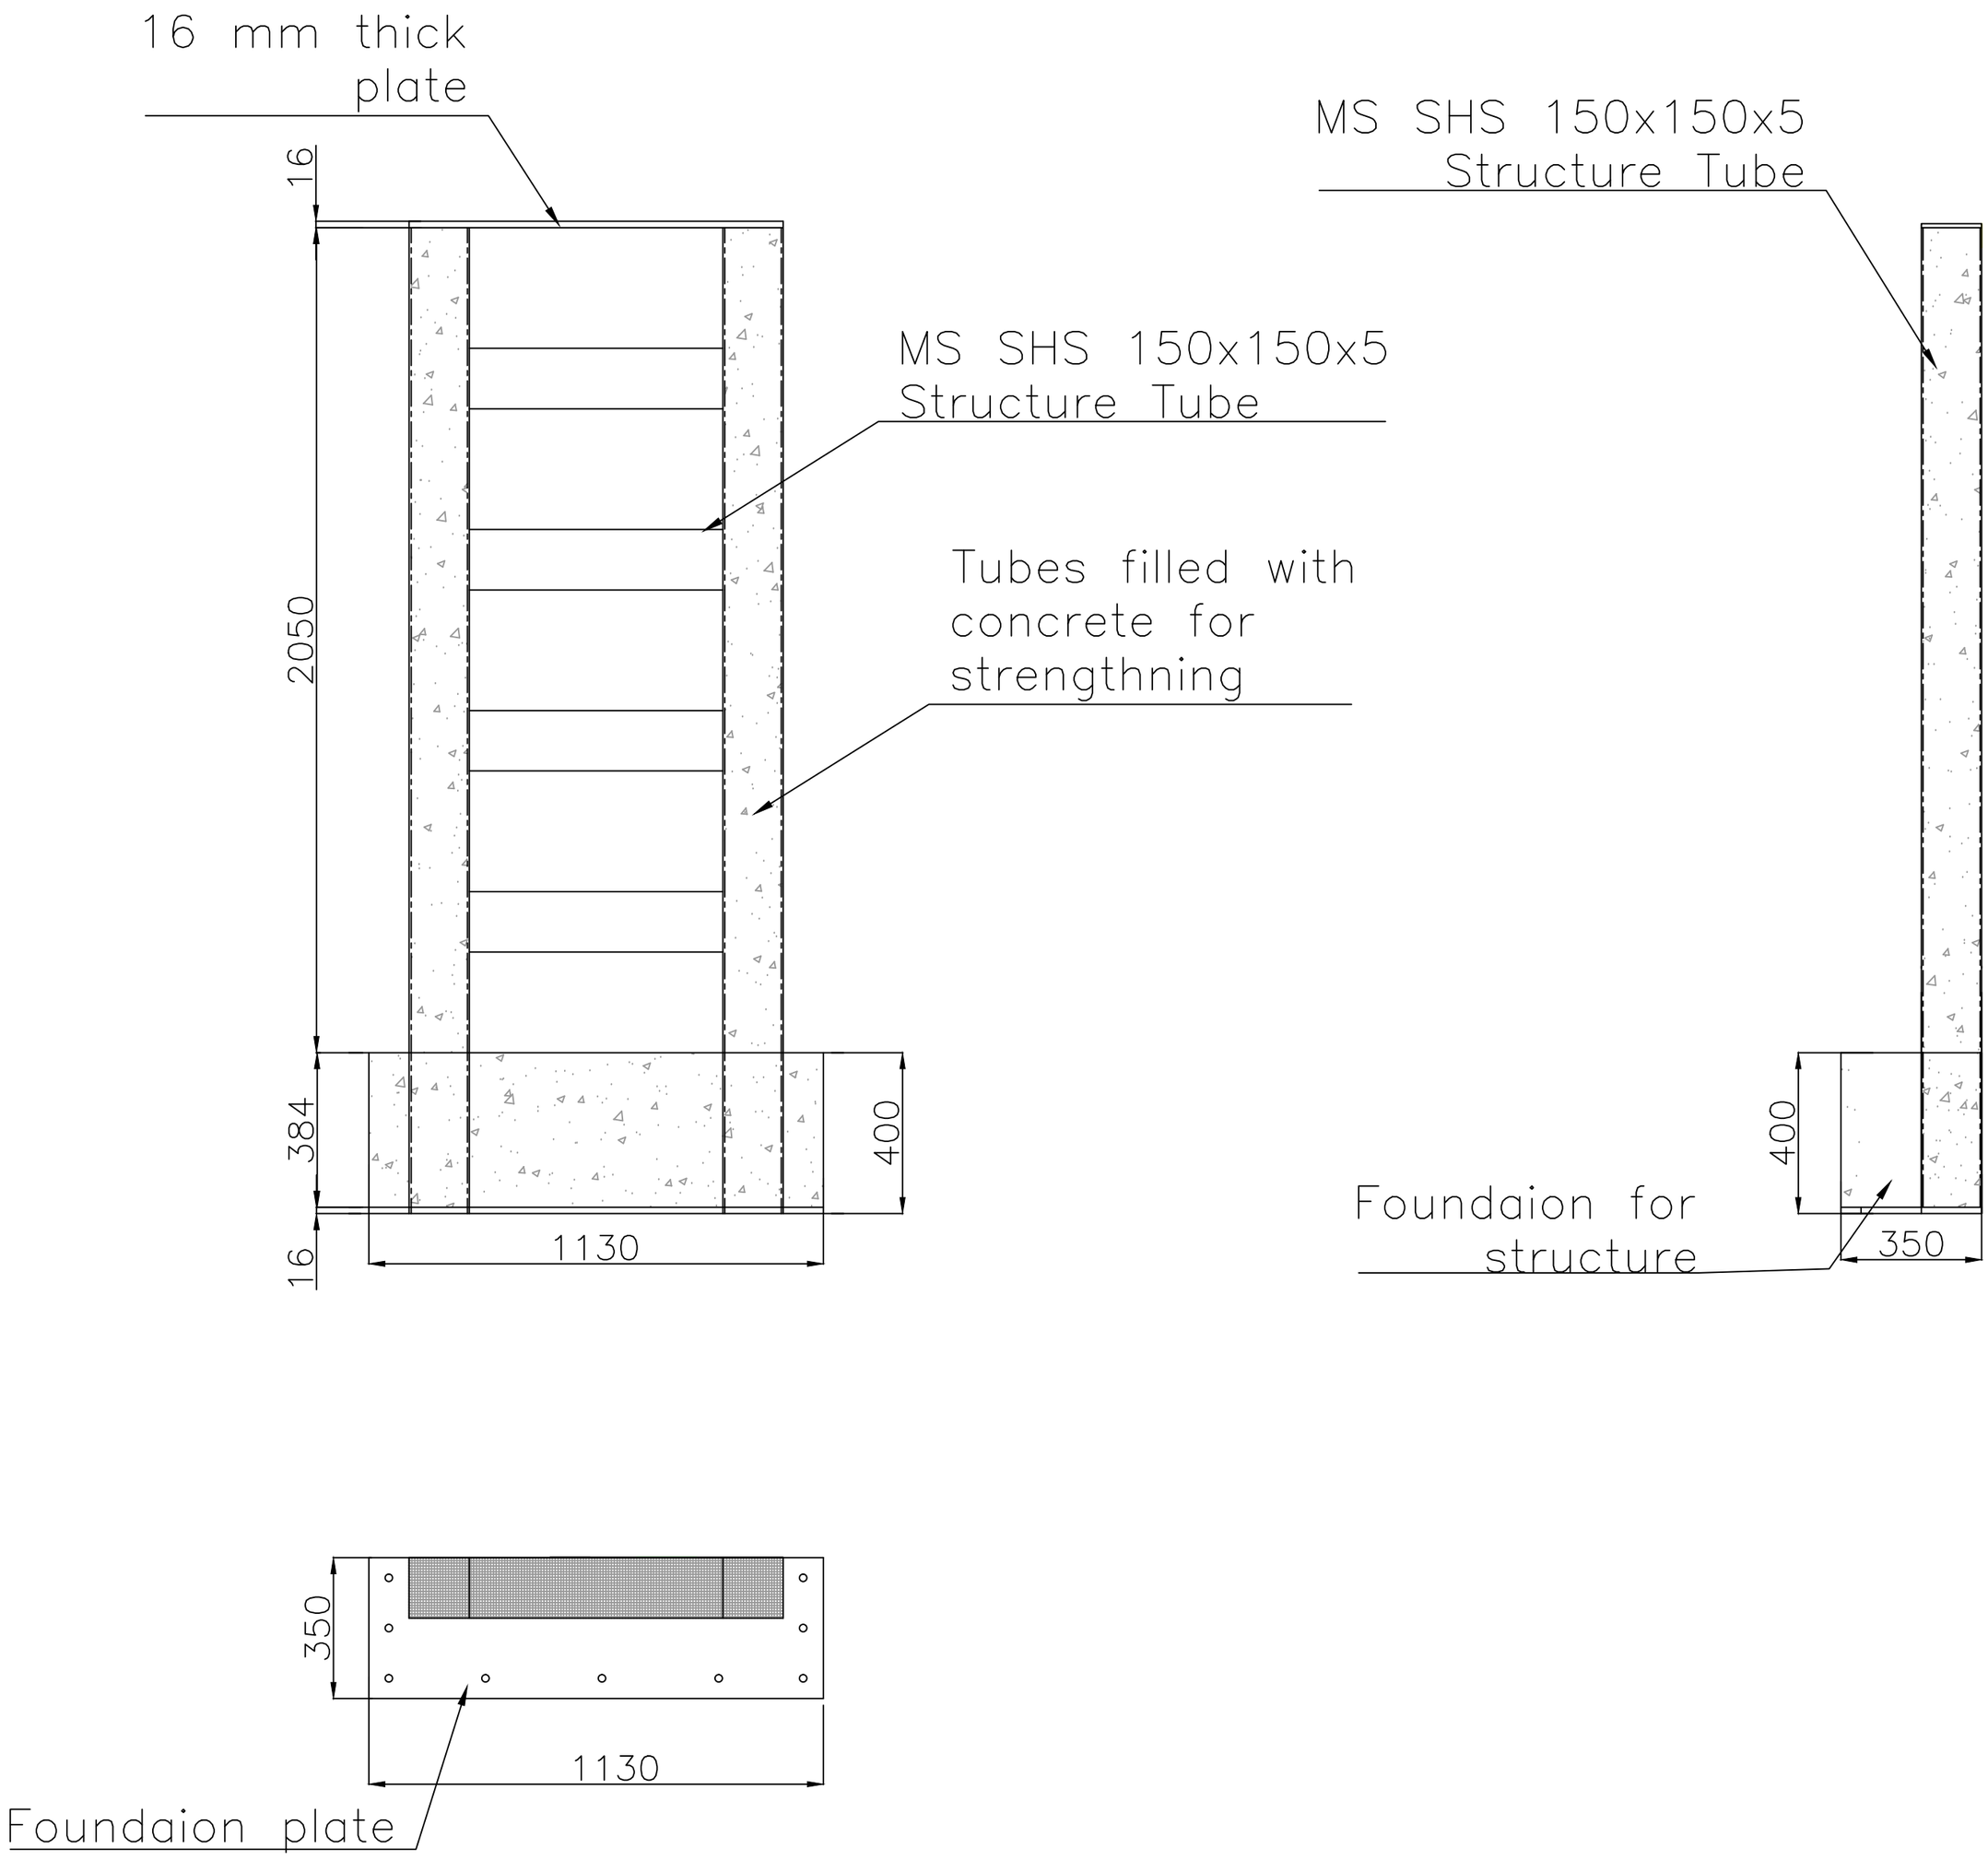


Rev 01- 02/02/2022

1. Plate shifted to front side and size reduced.

Note:

1. All dimension are in mm.
2. All civil work is in client scope.
3. If required, cladding is in client scope.

This drawing & design is the property of NIHVA TECHNOLOGIES. Not to be sold or copied to any other concern.

TITLE: Structure for swing gate				NIHVA TECHNOLOGIES PVT. LTD. PUNE Tel : 020 66304033 Email:- info@nihva.com Website:- www.nihva.com	
	NAME	SIGN	DATE	CLIENT -HAIMAVATHY PROPERTIES PVT. LTD.	
DRAWN	G.P.		22.01.22		
CHECK	A.K.		22.01.22	LOCATION - MUMBAI	
APPRD.	V.T.		22.01.22	PRODUCT - STRUCTURE	
If any queries contact : design@nihva.com				NIHVA\21-22\CLT\321	REV- 01
ALL DIMENSION ARE IN mm				SCALE: NTS	SHEET: 01 OF 01