



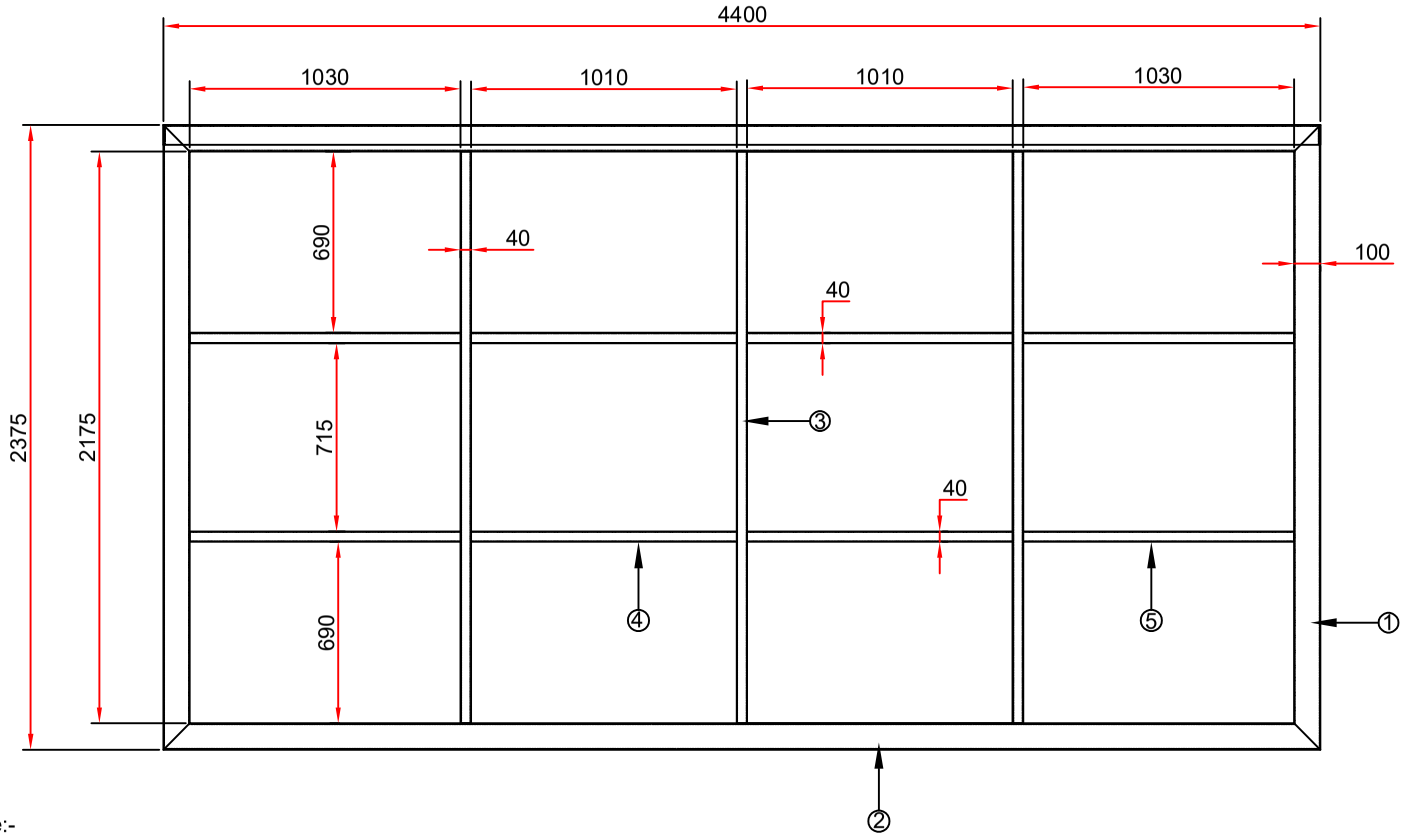

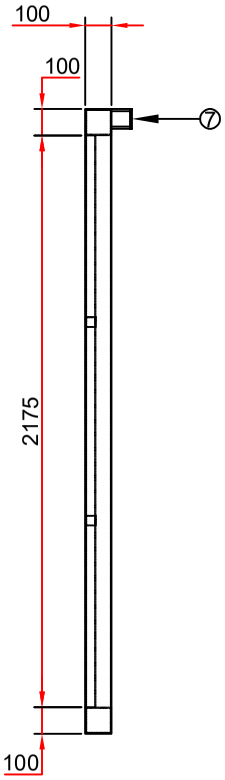

Note:-

1.All Dimension are in MM

2.Kindly Maintain the Given dimension

BOM			
SL NO.	DESCRIPTION	SPECIFICATION	QTY
1	MS SQ. TUBE	100X100X4X2375L	2NOS
2	MS SQ. TUBE	100X100X4X4400L	2NOS
3	MS SQ. TUBE	40X40X3.2X2175L	3NOS
4	MS SQ. TUBE	40X40X3.2X1010L	4NOS
5	MS SQ. TUBE	40X40X3.2X1030L	4NOS
6	MS FLAT	75X8X70L	2NOS
7	MS FLAT	75X8X4400L	1NO

Rev No.	Revision	Date	Revised By

This drawing & design is the property of NIHVA TECHNOLOGIES. Not to be sold or copied to any other concern.

TITLE:- Master Sliding Leaf

NIHVA TECHNOLOGIES PVT. LTD.

NIHVA TECHNOLOGIES PVT. LTD. PUNE
Tel : 020 66304033
Email:- info@nihva.com
Website:- www.nihva.com

	NAME	DATE	SIGN
DRAWN	SUJATA	21/07/2022	
CHECK	M.S	21/07/2022	
APPRD.	A.K	21/07/2022	

If any queries contact : design1@nihva.com

ALL DIMENSION ARE IN mm

CLIENT - OC Specialities

LOCATION - Solapur

PRODUCT - Master Sliding Leaf | QTY-01

DWG NO:- NIHVA/22-23/MFG/0042 | REV-00

SCALE: NTS | SCALE:-- 1:1 | SHEET: 01 OF 01