

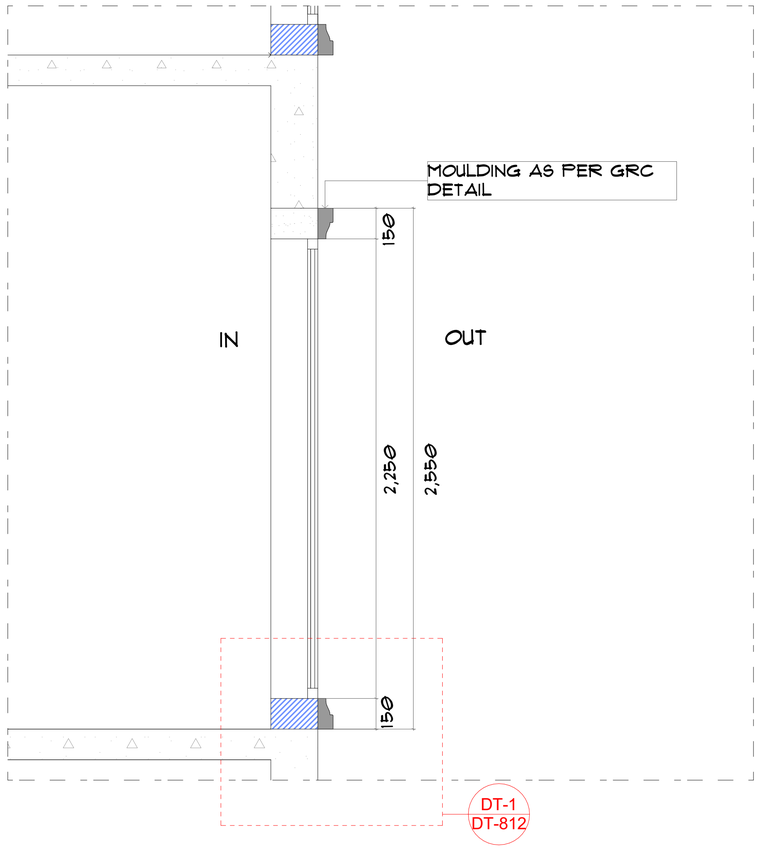



SE-01 / DT-812 SECTION SCALE- 1:10

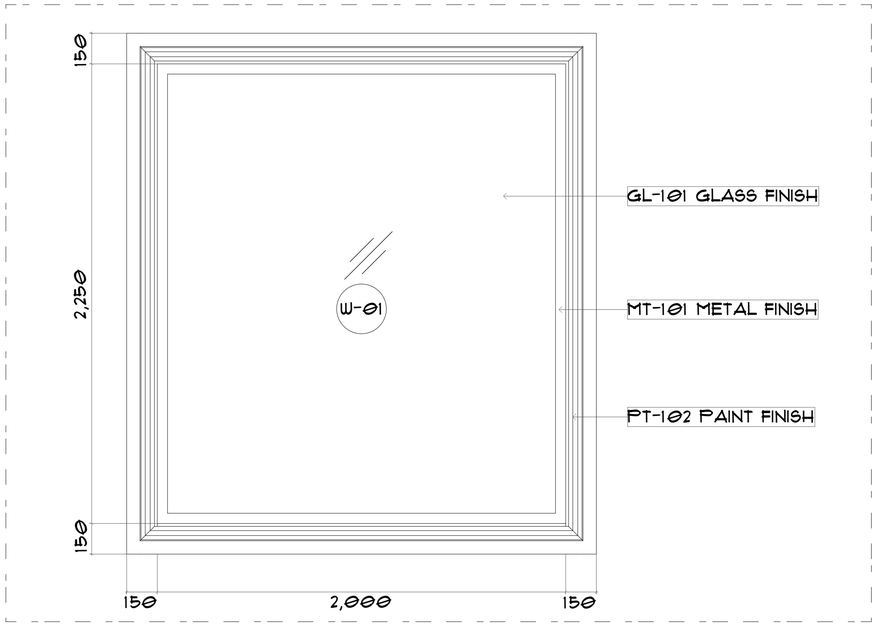


EL-01 / DT-812 ELEVATION SCALE- 1:10

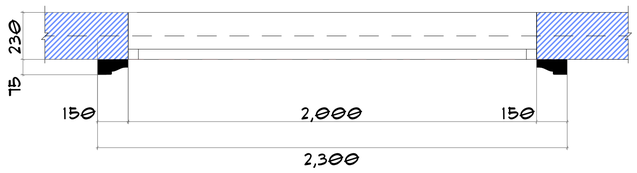

PL-01 / DT-812 PLAN SCALE- 1:10

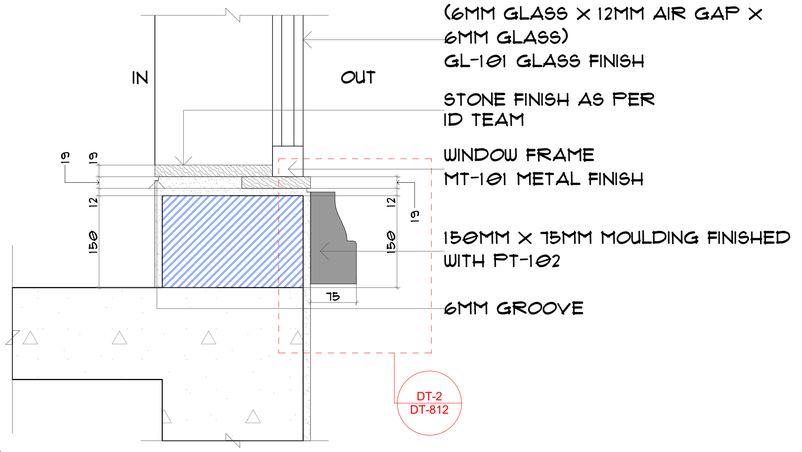

DT-01 / DT-812 DETAIL SCALE- 1:05

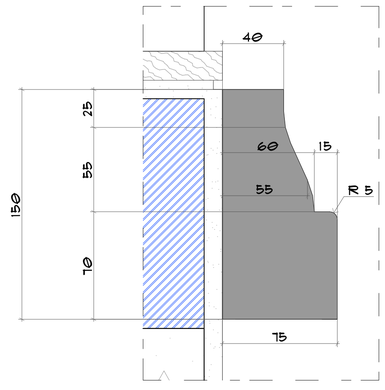

DT-02 / DT-812 DETAIL SCALE- 1:05

WINDOW DETAIL

SCALE 1:15, 1:5, 1:2 @ A1

KINDLY NOTE:
FINAL MEASURMENTS TO BE TAKEN FROM ON SITE.
STONE FINISH WILL BE AT BOTTOM OF WINDOW & REMAINING 3 SIDE WILL FINISHED WITH PAINT.

NOTE
- ALL DESIGNS, PRINTS & SPECIFICATIONS ARE THE PROPERTY OF DESIGNERS GROUP AND CANNOT BE USED WITHOUT THEIR WRITTEN PERMISSION.
- DO NOT SCALE THIS DRAWING. USE FIGURED DIMENSIONS ONLY.
- CONTRACTOR MUST VERIFY ALL DIMENSIONS ON SITE BEFORE COMMENCING ANY WORK.
- THESE DRAWINGS ARE TO BE READ IN CONJUNCTION WITH ARCHITECTURAL BASE DRAWINGS & RELEVANT CONSULTANT DRAWINGS.
- MANUFACTURER SHALL PREPARE 'SHOP DRAWINGS' OR 'PROTOTYPE SAMPLES' FOR RELEVANT ITEMS AND SUBMIT THEM TO THE DESIGNER FOR APPROVAL.

ISSUE	REV	DESCRIPTION	DATE

N

GFC COPY

Designers Group ARCHITECTS AND INTERIOR DESIGNERS
Address 2 - SUMEET SADAN, GR.FLOOR
BHAGOJI KEER MARG,
NEAR PARADISE THEATRE,
MAHIM (W), MUMBAI - 400 016.
TEL: 022 24442500 FAX: 022 24442700
EMAIL: admin@designers-group.com
https://www.designers-group.com

Holiday Inn BY IHG

Structural Consultant
R.D. MAGDUM

BOH Consultant
Mr. Imtiaz Mistry

M.E.P Consultant
Mr. Riyaz Pathan

Project
HOLIDAY INN UJJAIN

Area
DETAILS

Title
WINDOW DETAIL

Scale	Project Number
A1@ AS SHOWN	AR-497-2023-2024

Drawn	Checked	Dated
AR.SAI	AR.ANKITA	26-01-2026

Drawing Numbers	Issue
DT-812	B