



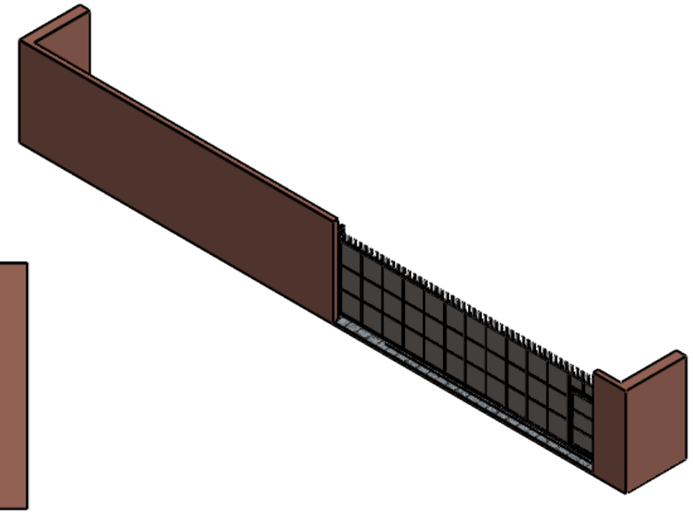

13000.00
LEAF LENGTH


12000.00
CLEARING OPENING

THURSTBEARING

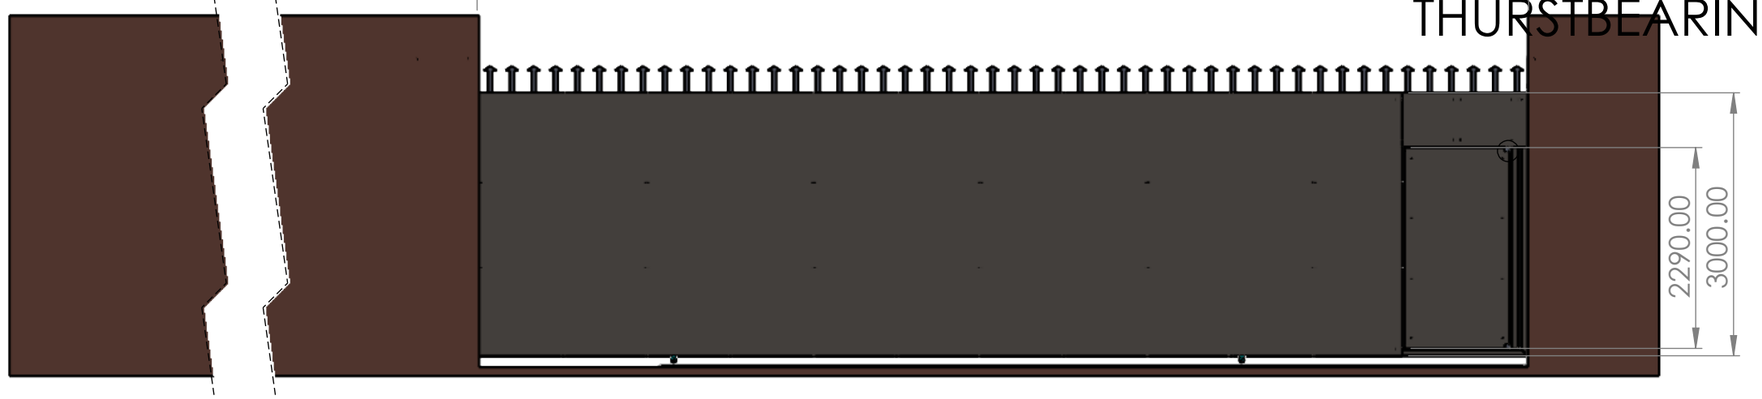

2290.00
3000.00


NYLOAN BEARING

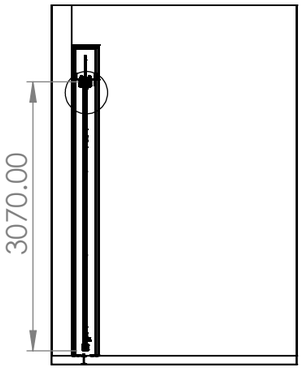

3070.00




THURSTBEARING
SCALE 1 : 10

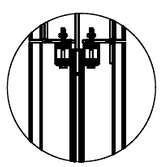


NYLOAN BEARING
SCALE 1 : 20


TITLE - AEGIS GROUP				NIHVA TECHNOLOGIES PVT.LTD.PUNE
DWG NO -			QTY - 1	Website - www.nihva.com
	NAME	SIGNATURE	DATE	PROJECT NO -
DRAWN	B.S.		04.07.2026	PRODUCT -
CHK'D	V.T.		04.07.2026	SITE LOCATION -
APPV'D	V.T.		04.07.2026	
if any queries contact - sales@nihva.com				REVISION -
ALL DIMENSION ARE IN mm			A3	SCALE - SHEET 1 OF 9

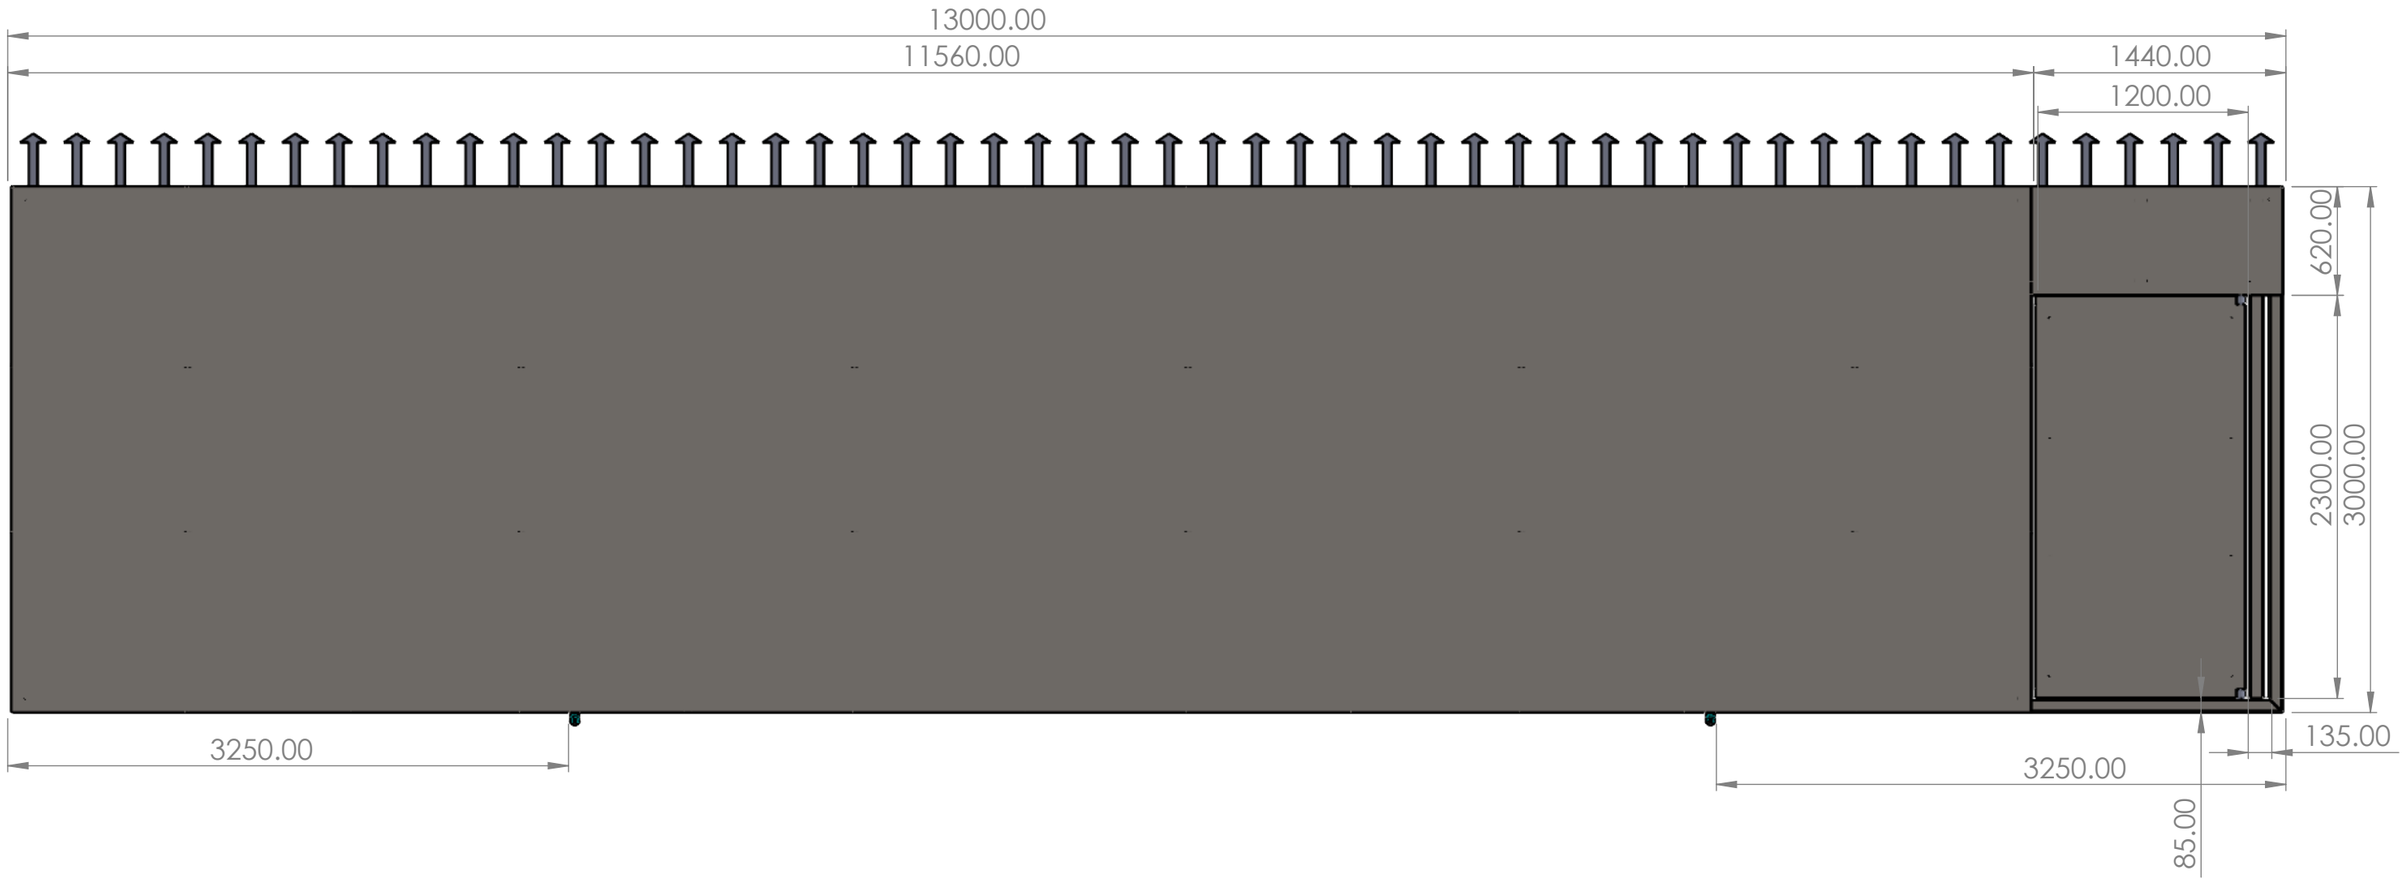


TITLE - AEGIS GROUP				NIHVA TECHNOLOGIES PVT.LTD.PUNE
DWG NO -			QTY -1	Website - www.nihva.com
	NAME	SIGNATURE	DATE	PROJECT NO -
DRAWN	B.S.		19.06.2026	PRODUCT -
CHK'D	V.T.		19.06.2026	SITE LOCATION -
APPV'D	V.T.		19.06.2026	
if any queries contact - sales@nihva.com				REVISION -
ALL DIMENSION ARE IN mm		A3		SCALE - SHEET 2 OF 9

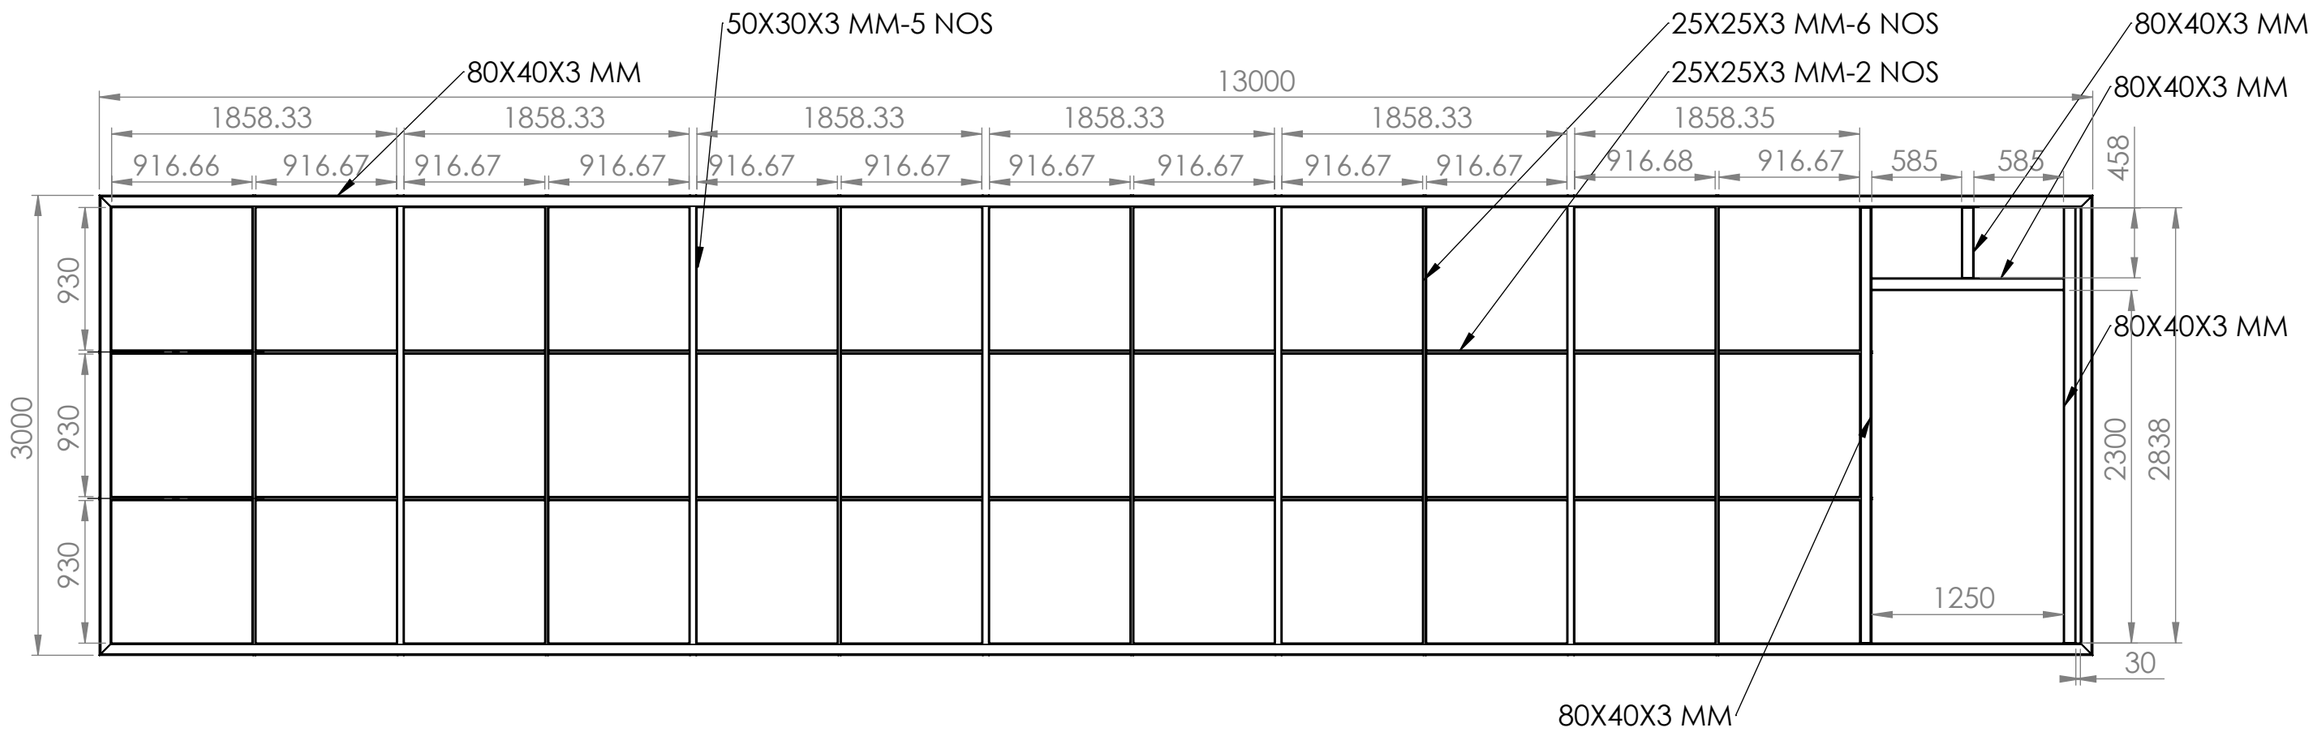


TITLE - AEGIS GROUP				NIHVA TECHNOLOGIES PVT.LTD.PUNE
DWG NO -			QTY - 1	Website - www.nihva.com
	NAME	SIGNATURE	DATE	PROJECT NO - NTPL 125
DRAWN	B.S.		06.06.2023	PRODUCT - RETRACTABLE ROOF
CHK'D	V.T.		06.06.2023	SITE LOCATION -
APPV'D	V.T.		06.06.2023	
if any queries contact - sales@nihva.com				REVISION -
ALL DIMENSION ARE IN mm		A3		SCALE - SHEET 3 OF 9

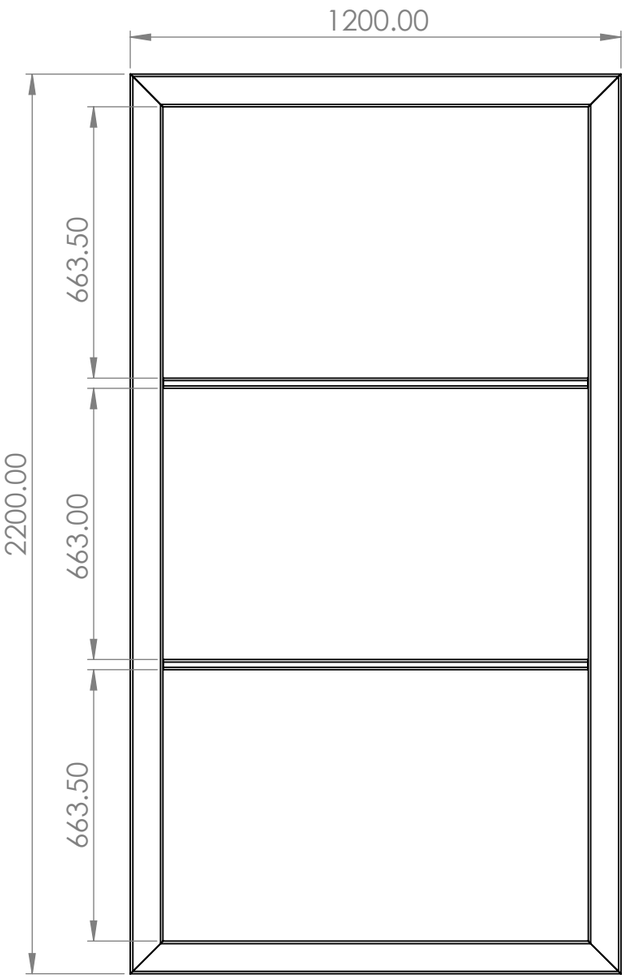

TITLE - AEGIS GROUP				NIHVA TECHNOLOGIES PVT.LTD.PUNE Website - www.nihva.com
DWG NO -			QTY - 1	
	NAME	SIGNATURE	DATE	PROJECT NO -
DRAWN	H.B.		06.06.2023	PRODUCT -
CHK'D	P.M.		06.06.2023	SITE LOCATION -
APPV'D	V.T.		06.06.2023	
if any queries contact - supportautomation@nihva.com				REVISION -
ALL DIMENSION ARE IN mm			A3	SCALE - SHEET 4 OF 9

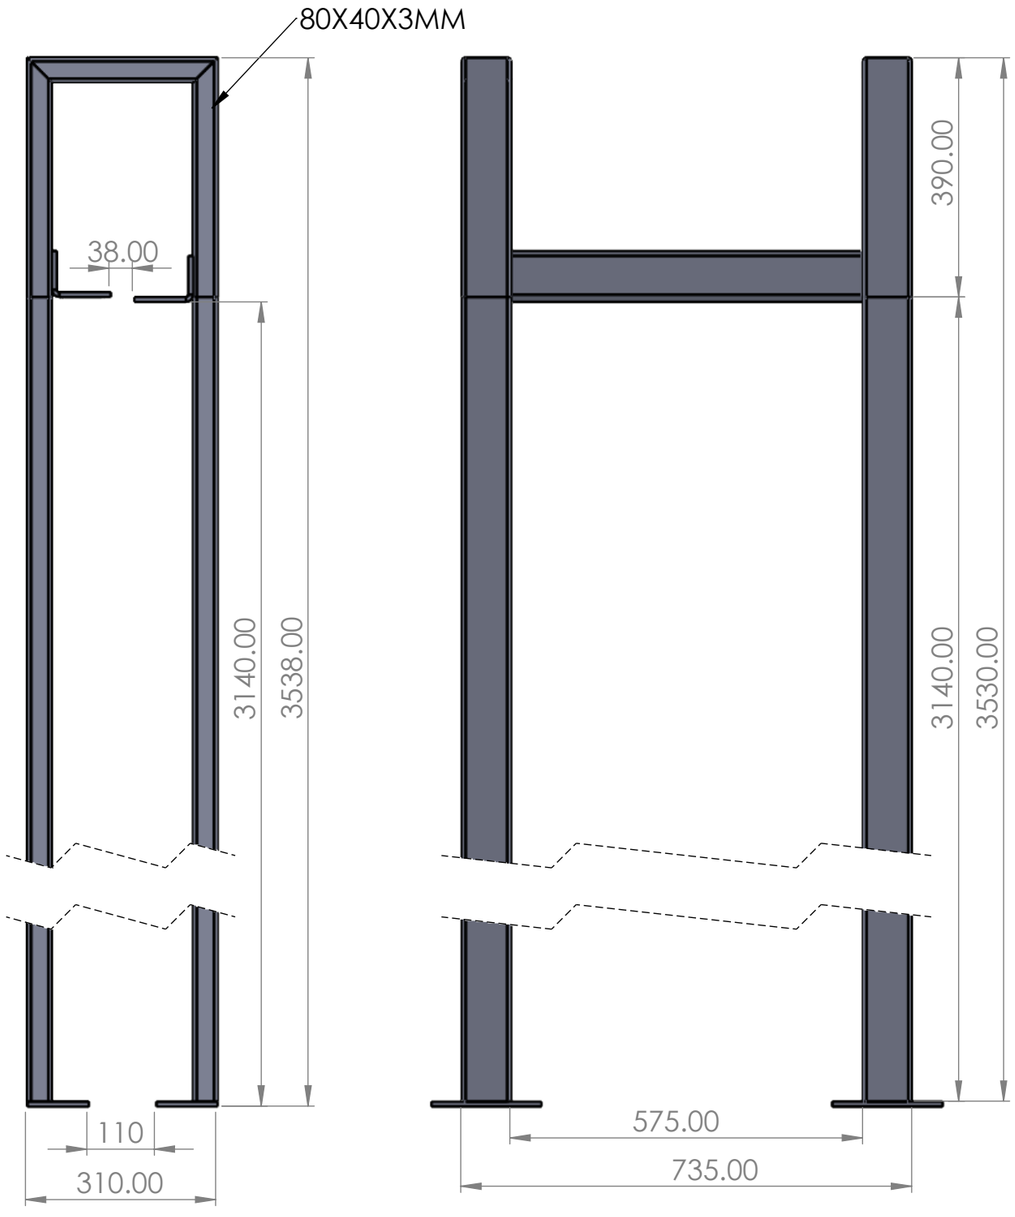


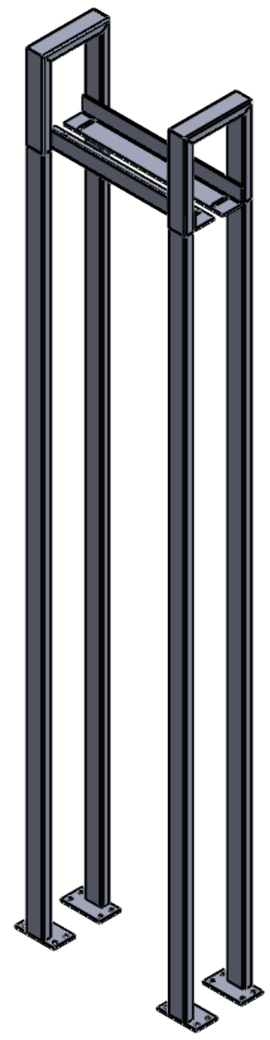


QTY - 1 NOS
3140 MM- 4 NOS

TITLE - AEGIS GROUP				NIHVA TECHNOLOGIES PVT.LTD.PUNE Website - www.nihva.com
DWG NO -			QTY - 1	
	NAME	SIGNATURE	DATE	PROJECT NO -
DRAWN	B.S.		19.06.2026	PRODUCT -
CHK'D	V.T.		19.06.2026	SITE LOCATION -
APPV'D	V.T.		19.06.2026	
if any queries contact - sales@nihva.com				REVISION -
ALL DIMENSION ARE IN mm		A3		SCALE - SHEET 5 OF 9




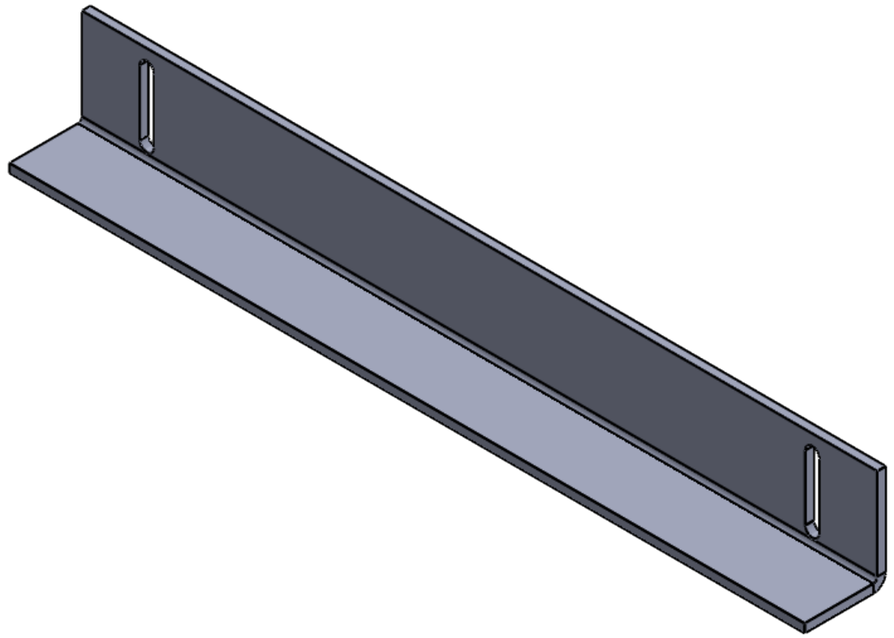


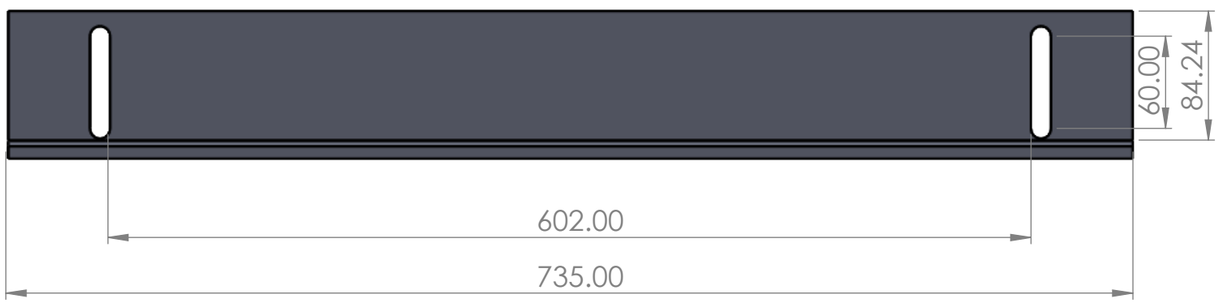


QTY - 21 NOS
THICKNESS - 8 MM

TITLE - AEGIS GROUP				NIHVA TECHNOLOGIES PVT.LTD.PUNE Website - www.nihva.com
DWG NO -			QTY - 1	
	NAME	SIGNATURE	DATE	PROJECT NO -
DRAWN	B.S.		19.06.2026	PRODUCT -
CHK'D	V.T.		19.06.2026	SITE LOCATION -
APPV'D	V.T.		19.06.2026	
if any queries contact - supportautomation@nihva.com				REVISION -
ALL DIMENSION ARE IN mm			A3	SCALE - SHEET 6 OF 9

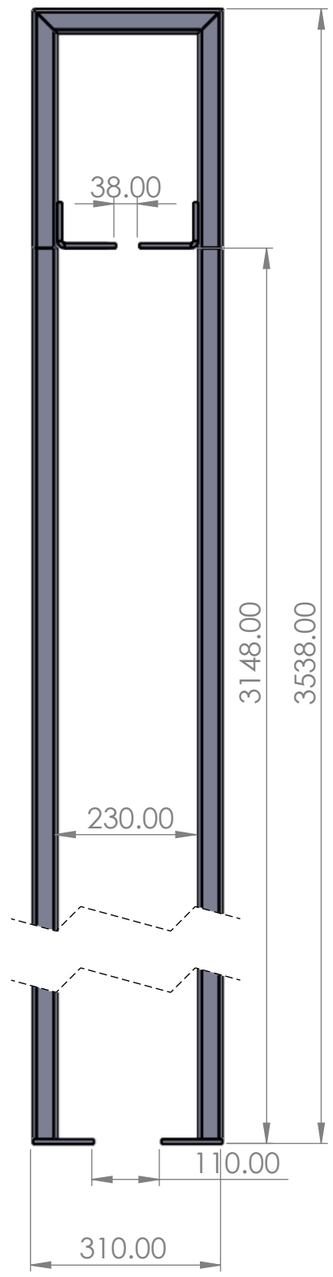


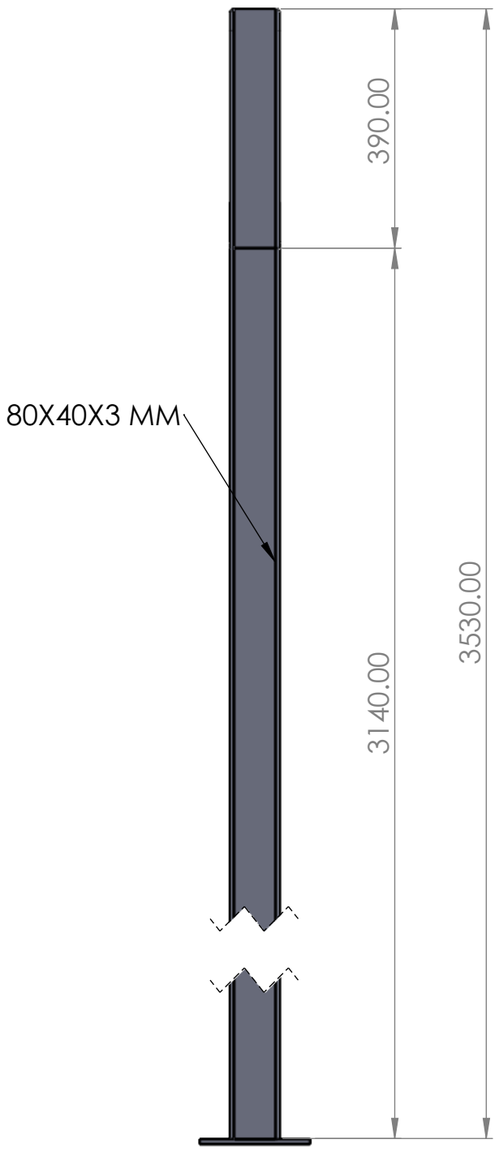


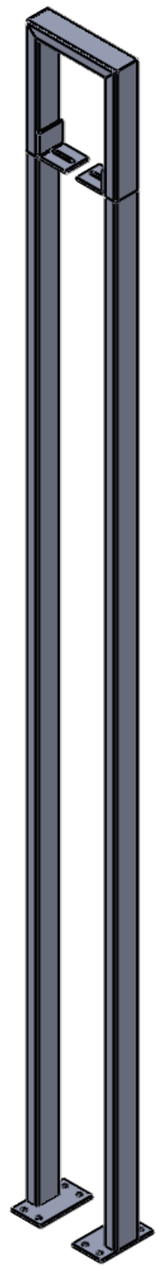


QTY - 2 NOS
3140 MM - 4 NOS

TITLE - AEGIS GROUP				NIHVA TECHNOLOGIES PVT.LTD.PUNE Website - www.nihva.com
DWG NO -			QTY - 1	
	NAME	SIGNATURE	DATE	PROJECT NO -
DRAWN	B.S.		19.06.2026	PRODUCT -
CHK'D	V.T.		19.06.2026	SITE LOCATION -
APPV'D	V.T.		19.06.2026	
if any queries contact - supportautomation@nihva.com				REVISION -
ALL DIMENSION ARE IN mm			A3	SCALE - SHEET 7 OF 9

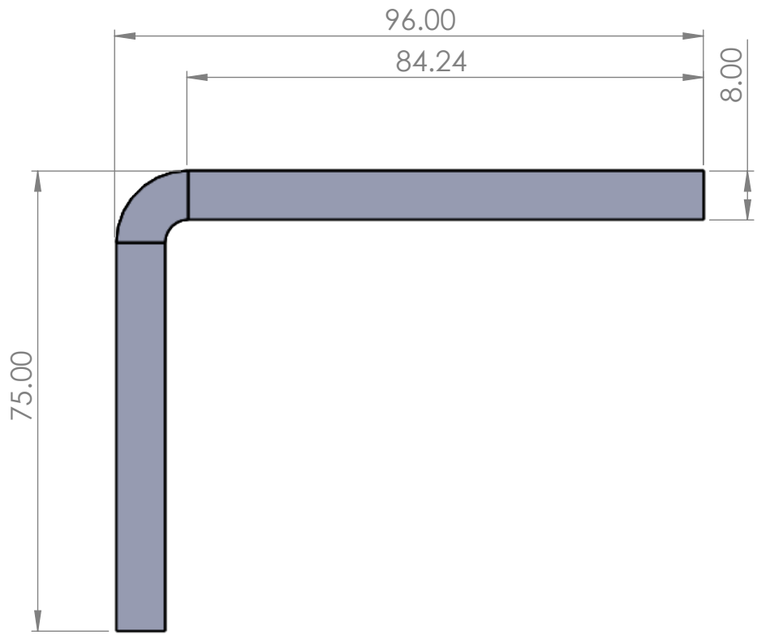


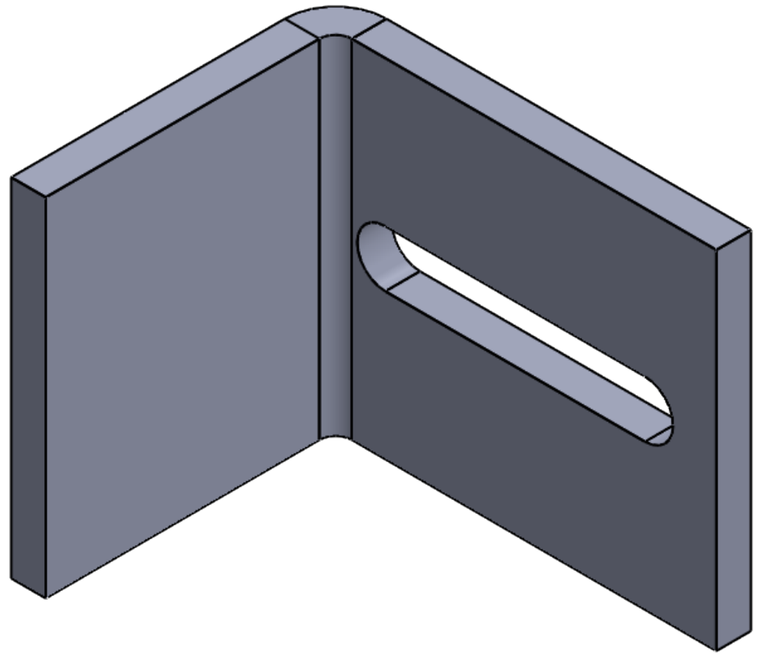


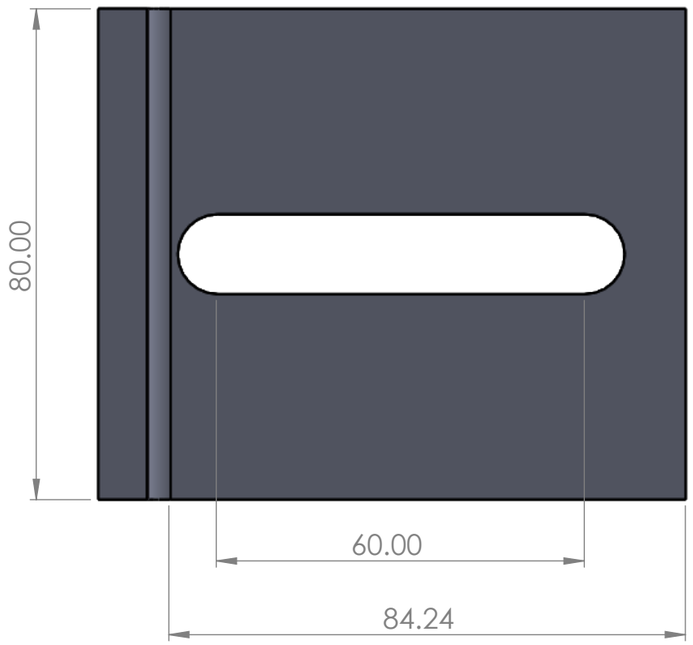


QTY - 4 NOS
MATERIAL - MS
THICKNESS-8 NOS

TITLE - AEGIS GROUP				NIHVA TECHNOLOGIES PVT.LTD.PUNE
DWG NO -			QTY - 1	Website - www.nihva.com
	NAME	SIGNATURE	DATE	PROJECT NO -
DRAWN	B.S		19.06.2026	PRODUCT -
CHK'D	V.T		19.06.2026	SITE LOCATION -
APPV'D	V.T.		19.06.2026	
if any queries contact - supportautomation@nihva.com				REVISION -
ALL DIMENSION ARE IN mm			A3	SCALE - SHEET 8 OF 9

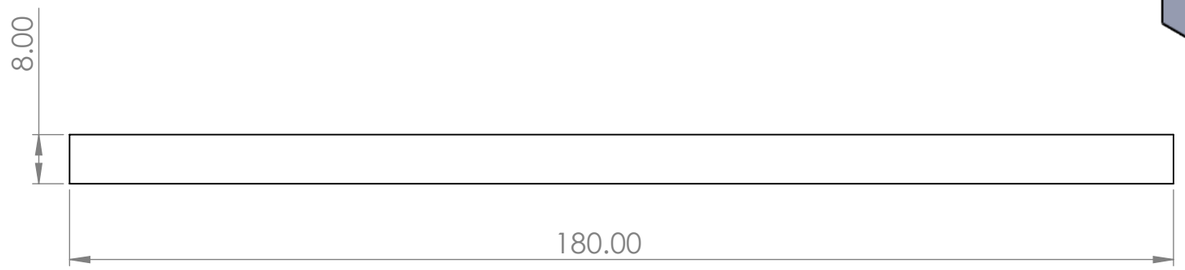

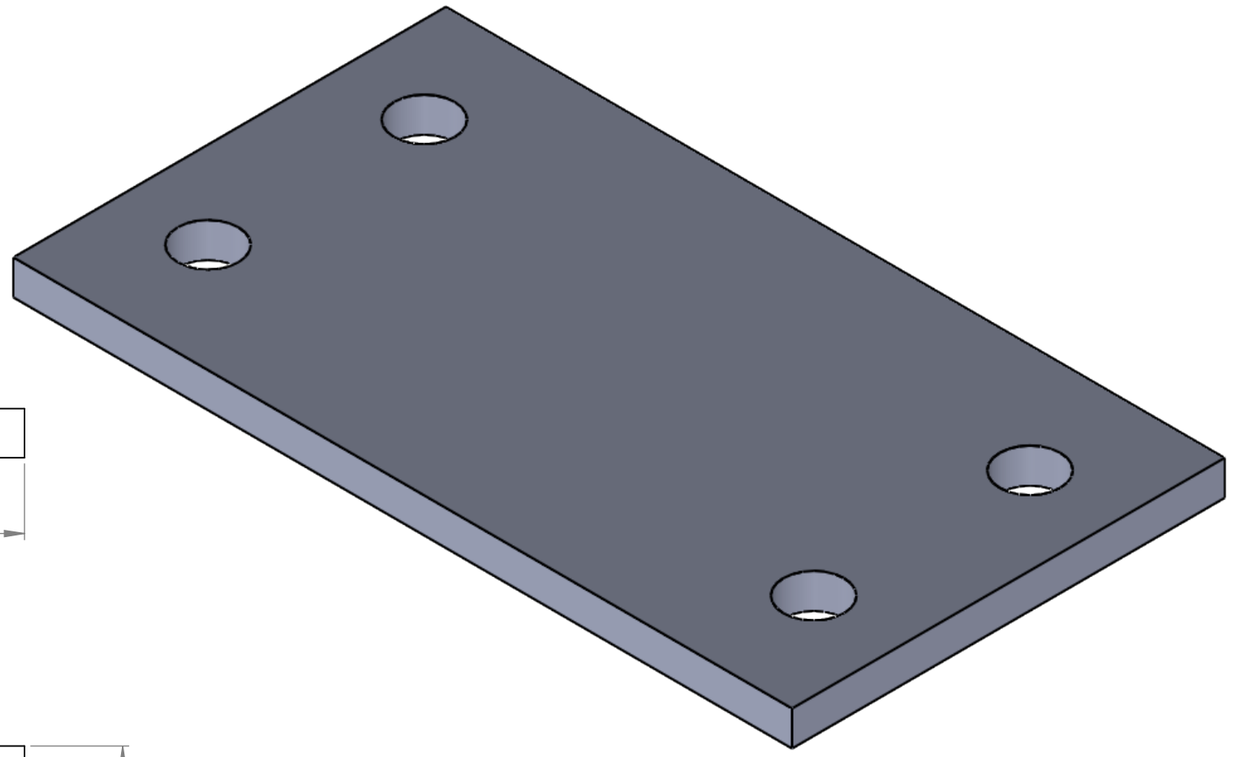

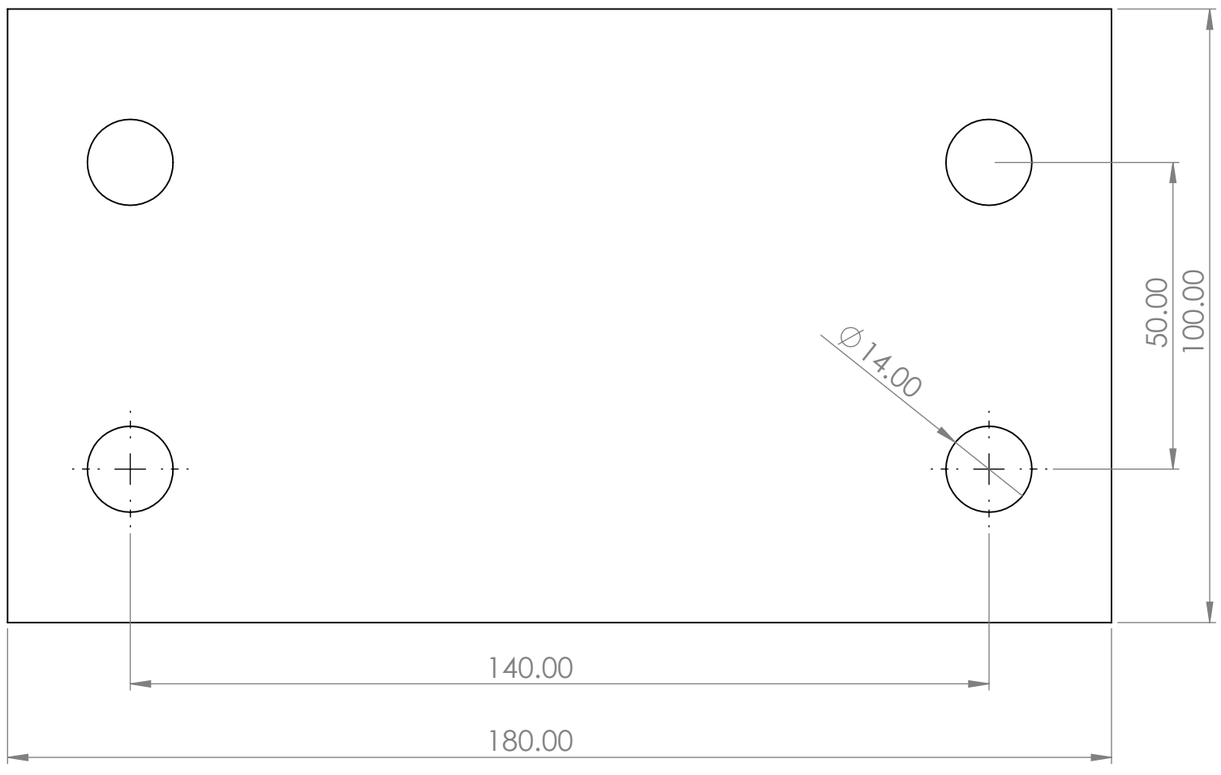

QTY - 8 NOS
THICKNESS - 8 MM

TITLE - AEGIS GROUP				NIHVA TECHNOLOGIES PVT.LTD.PUNE Website - www.nihva.com
DWG NO -			QTY - 1	
	NAME	SIGNATURE	DATE	PROJECT NO -
DRAWN	H.B.		06.06.2023	PRODUCT -
CHK'D	P.M.		06.06.2023	SITE LOCATION -
APPV'D	V.T.		06.06.2023	
if any queries contact - supportautomation@nihva.com				REVISION -
ALL DIMENSION ARE IN mm			A3	SCALE - SHEET 9 OF 9