


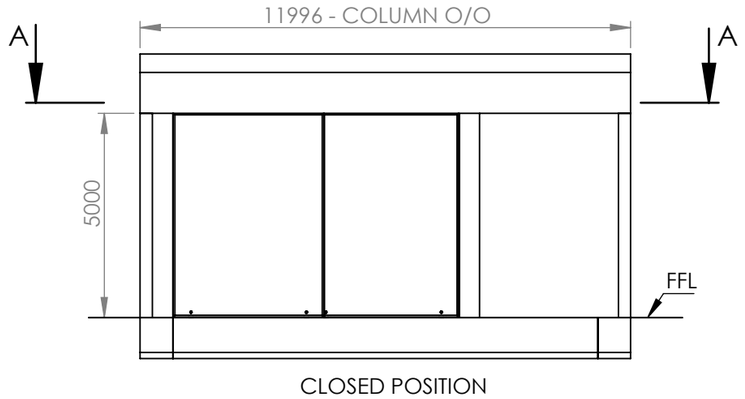



CLOSED POSITION

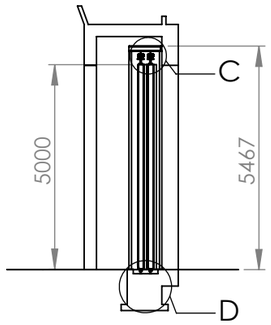


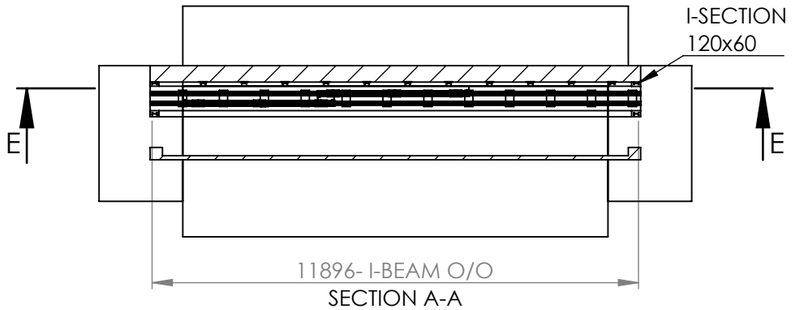


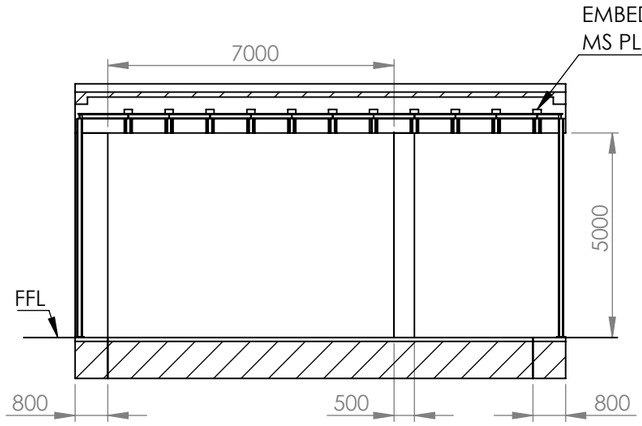

SECTION A-A

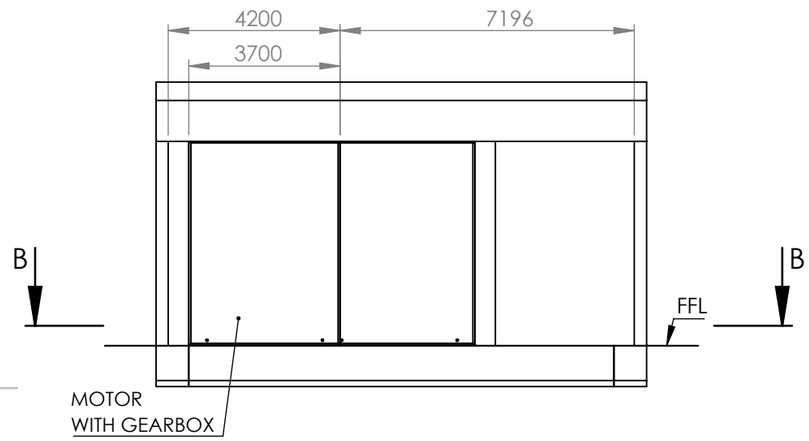



SECTION E-E

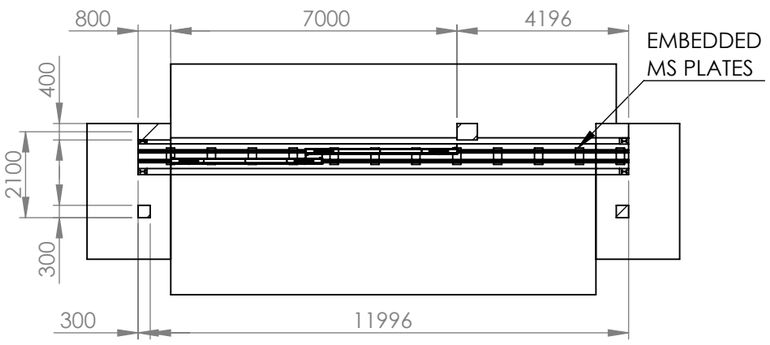





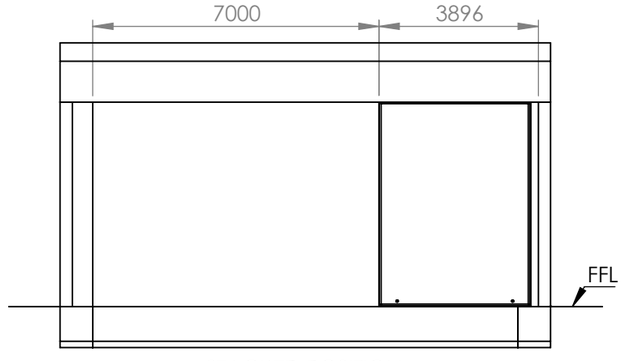

SECTION B-B

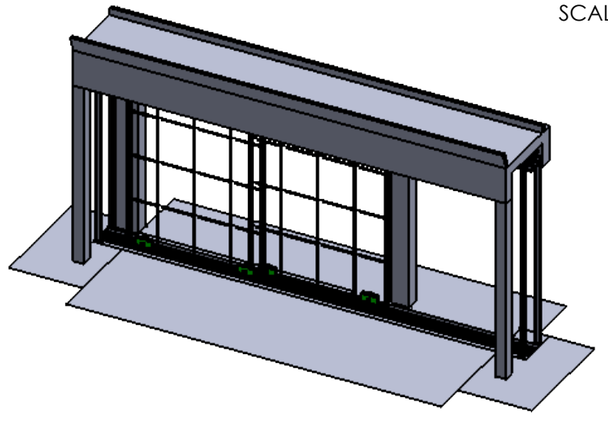



STACKED POSITION

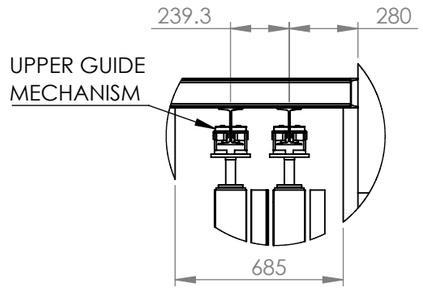




DETAIL C
SCALE 1 : 25

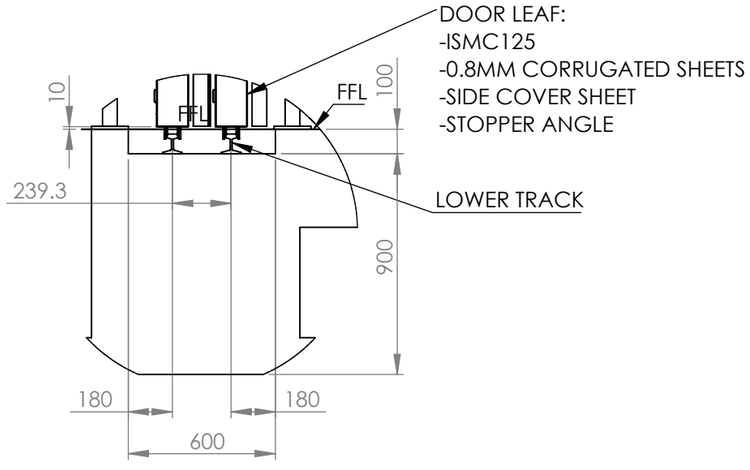


DETAIL D
SCALE 1 : 25

| | | | |
|---|---|---|---|
| **TITLE :** | **HANGING SLIDING DOOR** | | |
| | **NAME** | **SIGN** | **DATE** |
| DRAWN | BHARATI SABALE | | 23-12-2024 |
| **CHK'D** | SURAJ WARALE | | 23-12-2024 |
| **APPV'D** | VIJAY T | | 23-12-2024 |
| | | DIMENSIONS ARE IN MILLIMETERS | |

NIHVA Technologies Pvt. Ltd.

**NIHVA TECHNOLOGIES PVT LTD**

**CLIENT NAME :** ISRO

**PRODUCT NAME :** HANGING SLIDING DOOR

**SITE LOCATION :** ALUVA, KERALA

**DWG NO.** GA

A3

REVISION : 1

SCALE:

SHEET 1 OF 1