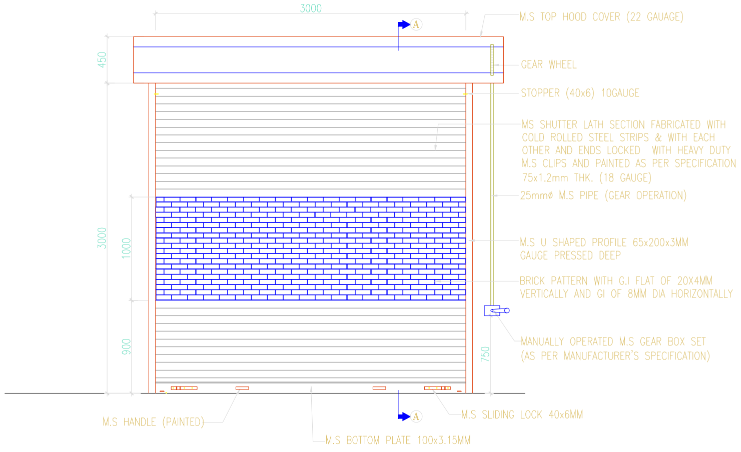
3000
450
3000
1000
900
750
A
M.S TOP HOOD COVER (22 GAUAGE)
GEAR WHEEL
STOPPER (40x6) 10GAUGE
MS SHUTTER LATH SECTION FABRICATED WITH COLD ROLLED STEEL STRIPS & WITH EACH OTHER AND ENDS LOCKED WITH HEAVY DUTY M.S CLIPS AND PAINTED AS PER SPECIFICATION 75x1.2mm THK. (18 GAUGE)
25mmø M.S PIPE (GEAR OPERATION)
M.S U SHAPED PROFILE 65x200x3MM GAUGE PRESSED DEEP
BRICK PATTERN WITH G.I FLAT OF 20X4MM VERTICALLY AND GI OF 8MM DIA HORIZONTALLY
MANUALLY OPERATED M.S GEAR BOX SET (AS PER MANUFACTURER'S SPECIFICATION)
M.S HANDLE (PAINTED)
M.S SLIDING LOCK 40x6MM
M.S BOTTOM PLATE 100x3.15MM

ELEVATION OF GRILLED ROLLING SHUTTER

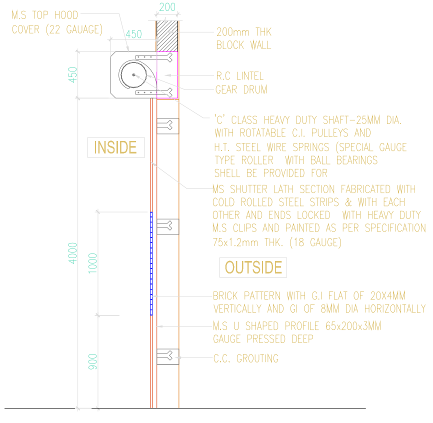
M.S TOP HOOD COVER (22 GAUAGE)
200
450
450
4000
1000
900
INSIDE
OUTSIDE
200mm THK BLOCK WALL
R.C LINTEL
GEAR DRUM
'C' CLASS HEAVY DUTY SHAFT-25MM DIA. WITH ROTATABLE C.I. PULLEYS AND H.T. STEEL WIRE SPRINGS (SPECIAL GAUGE TYPE ROLLER WITH BALL BEARINGS SHELL BE PROVIDED FOR
MS SHUTTER LATH SECTION FABRICATED WITH COLD ROLLED STEEL STRIPS & WITH EACH OTHER AND ENDS LOCKED WITH HEAVY DUTY M.S CLIPS AND PAINTED AS PER SPECIFICATION 75x1.2mm THK. (18 GAUGE)
BRICK PATTERN WITH G.I FLAT OF 20X4MM VERTICALLY AND GI OF 8MM DIA HORIZONTALLY
M.S U SHAPED PROFILE 65x200x3MM GAUGE PRESSED DEEP
C.C. GROUTING

SECTION AT AA

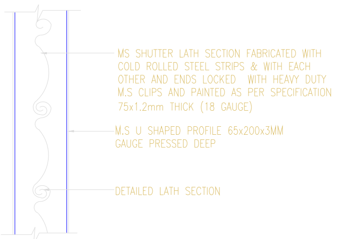
MS SHUTTER LATH SECTION FABRICATED WITH COLD ROLLED STEEL STRIPS & WITH EACH OTHER AND ENDS LOCKED WITH HEAVY DUTY M.S CLIPS AND PAINTED AS PER SPECIFICATION 75x1.2mm THICK (18 GAUGE)
M.S U SHAPED PROFILE 65x200x3MM GAUGE PRESSED DEEP
DETAILED LATH SECTION

DETAIL-A

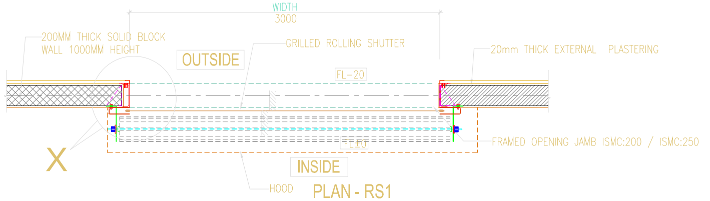
WIDTH
3000
200MM THICK SOLID BLOCK WALL 1000MM HEIGHT
OUTSIDE
GRILLED ROLLING SHUTTER
20mm THICK EXTERNAL PLASTERING
FL-20
FL-10
FRAMED OPENING JAMB ISMC:200 / ISMC:250
X
INSIDE
HOOD

PLAN - RS1

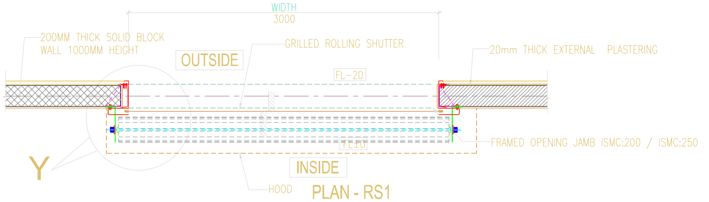
WIDTH
3000
200MM THICK SOLID BLOCK WALL 1000MM HEIGHT
OUTSIDE
GRILLED ROLLING SHUTTER
20mm THICK EXTERNAL PLASTERING
FL-20
FL-10
FRAMED OPENING JAMB ISMC:200 / ISMC:250
Y
INSIDE
HOOD

PLAN - RS1

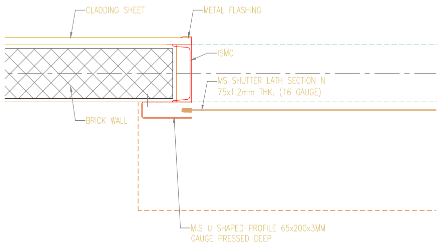
CLADDING SHEET
METAL FLASHING
ISMC
MS SHUTTER LATH SECTION N 75x1.2mm THK. (16 GAUGE)
BRICK WALL
M.S U SHAPED PROFILE 65x200x3MM GAUGE PRESSED DEEP

DETAIL X-X

SCALE : 1:10

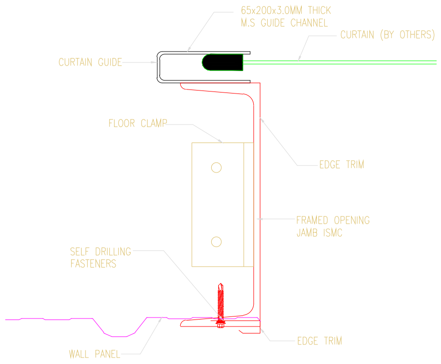

DETAIL Y-Y

SCALE : 1:10

KEY PLAN:
(NOT TO SCALE)

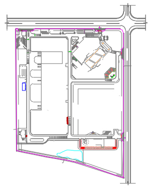

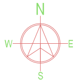

GENERAL NOTES :

ALL DIMENSIONS ARE IN MILLIMETRES AND ARE UNFINISHED DIMENSIONS UNLESS OTHERWISE SPECIFIED.

ALL LEVELS ARE IN METRES AND ARE UNFINISHED LEVELS UNLESS OTHERWISE SPECIFIED.

DO NOT SCALE DRAWINGS. ONLY WRITTEN DIMENSIONS SHALL BE FOLLOWED, ANY DISCREPANCIES NOTED SHALL BE BROUGHT TO THE NOTICE OF THE ARCHITECT PRIOR TO EXECUTION.

FOR DETAILS SUCH AS DOORS, WINDOWS, GRILLS, GATES, SKYLIGHT, TOILETS, STAIRCASES, HANDRAIL, RAILING, ETC. REFER RESPECTIVE ARCHITECTURAL DRAWINGS.

THESE DRAWINGS SHALL BE CORRELATED AND READ IN CONJUNCTION WITH RESPECTIVE CONSULTANT'S APPROVED DRAWINGS FOR STRUCTURAL MEMBERS, SERVICES SUCH AS PLUMBING, SANITARY, ELECTRICAL, AIR-CONDITIONING, VENTILATION, RAINWATER DRAINAGE & WATERPROOFING AND LANDSCAPING. ANY DISCREPANCIES NOTED SHALL BE BROUGHT TO THE NOTICE OF THE ARCHITECT PRIOR TO EXECUTION.

ALL TOILETS WILL HAVE SUNK FLOORS (UNLESS OTHERWISE SPECIFIED) AS PER RESPECTIVE STRUCTURAL DRAWINGS, AND WATERPROOFING AS PER SPECIFICATION.

ALL ROOF SLABS TO HAVE WATERPROOFING AND INSULATION TREATMENT AS PER SPECIFICATIONS.

NOTE:-
FOR ROLLING SHUTTERS MORE THAN 4.5M HEIGHT ADDITIONAL STIFFENER BASED ON WIND PRESSURE SHOULD BE CONSIDERED AND ALSO MUST COMPLY WITH FM GLOBAL REQUIREMENTS

SCHEDULE OF JOINERY

TYPE	DESCRIPTION	SIZE
ALV1	ALUMINUM LOUVERED VENTILATOR	6000 x 1500
ALV2	ALUMINUM LOUVERED VENTILATOR	5000 x 1500
RS	ROLLING SHUTTER	8000 x 9000
RS1	ROLLING SHUTTER	3000 x 3000
D3	FLUSH DOOR	750 x 2100
FD	FIRE EXIT DOOR	1200 x 2400
SW	SLIDING WINDOW	2100 x 1500
FW	WINDOW	3000 x 1500
FW1	WINDOW	1500 x 1500
V1	VENTILATOR	750 X 600

REV.	DESCRIPTION	DATE	BY	CHD.
R1	GOOD FOR CONSTRUCTION	05.03.2016	SPM	KC

AMENDMENT

Construction work shall be executed only as per the latest revision drawing. Once a revision drawing is issued, the validity of the previous revision drawing stands cancelled and as such construction shall not be carried out as per superseded revisions. The Contractor is expected to:
1. Maintain a register of Drawing Receipts, listing drawing number & revision number, title, from whom received, date received, number of copies received, details of transmittal from the issuer & any other relevant details to be advised from time to time.
2. Archive all previous revision issues immediately upon receipt of a new revision and no superseded drawing shall remain in the site of works except in the Contractor's archives for record and reference purposes only.
3. While archiving superseded drawing, the Contractor is expected to stamp all previously issued drawings / prints appropriately, mentioning the date and revision number of the new revision on account of which the previous revision is archived.
4. The Contractor shall allow the representative of Client / PMC / Architect to inspect Contractor's archives for ensuring compliance.
5. Any work carried out by the Contractor using a superseded drawing after the issue of a new revision is liable for rejection and reinstatement as per new revision at Contractor's risk and cost without any entitlement to extension of time

GRAPHIC SCALE: 0.2M 0 0.2M 0.4M 0.6M 1.0M

CLIENT:

GE India Industrial PVT LTD
Chakan, Pune.

PROJECT:

PROPOSED MULTIMODAL PROJECT AT PUNE

DRAWING TITLE:

GRILLED ROLLING SHUTTER DETAILS
RS1 - 3000 X 3000

SCALE : 1:25,10 (A1)
DRAWN : S.PRAGASAM
DATE : 05.03.16
CHKD : KC
REV
DRAWING NO:
GE-P-LAB1-AR10-01-01-203224
R1

design | interiors | engineering | construction management

C.R.Narayana Rao (Consultants) Private Limited

CRN
C R NARAYANA RAO

No. 10, Karpagambal Nagar,
Mylapore, Chennai-600 004.
India.
www.crn.co.in

THESE DRAWINGS ARE UNDER COPYRIGHT AND ARE THE PROPERTY OF CRN. NONE OF THE DRAWINGS AND RELATED DOCUMENTS CAN BE REPRODUCED, COPIED IN WHOLE OR IN PART WITHOUT PRIOR EXPRESSED WRITTEN CONSENT OF CRN. THESE DRAWINGS CANNOT BE HANDED OVER TO A THIRD PARTY OR USED FOR ANY PURPOSE, OTHER THAN THAT FOR WHICH IT HAS BEEN LOANED. AFTER FULFILLING THE PURPOSE OF ISSUE THE DRAWINGS SHALL BE RETURNED TO CRN.

DTS CELL - JOINERY DETAILS