



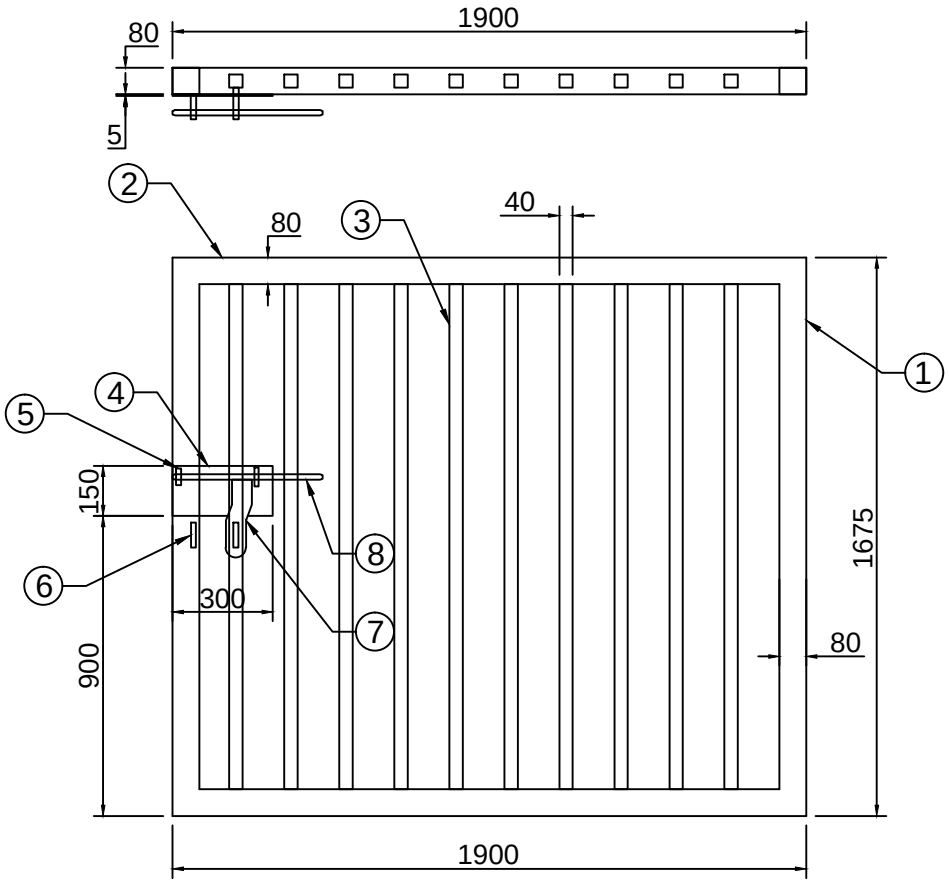


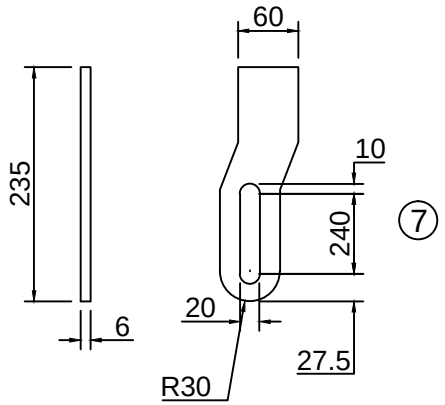

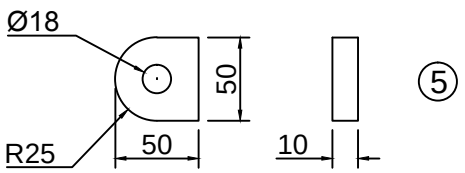

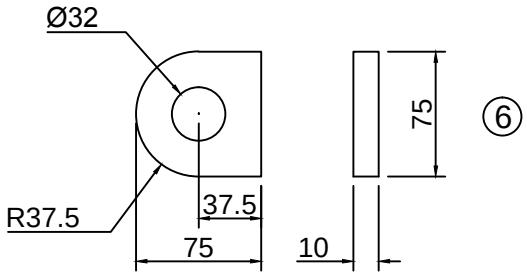

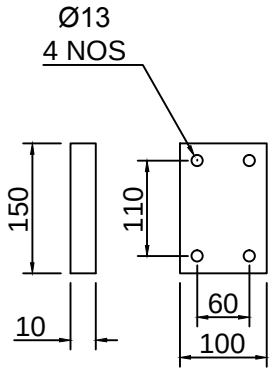

SR.NO	DESCRIPTION	SPECIFICATION	QTY	WEIGHT
11	FLAT	100 X 10 X 150L	2 NOS	2 KGS
10	HINGE BEARING	4" BEARING HINGES (4 THRUST + 4 BALL BEARING SET)	2 NOS	
9	ISMC	75 X 40 X 200L	2 NOS	3 KGS
8	M.S ROD	Ø16 X 450L	2 NOS	1.5 KGS
7	PROFILE	60 X 6 X 235L	2 NOS	2 KGS
6	PROFILE	75 X 10 X 75L	4 NOS	2 KGS
5	PROFILE	50 X 10 X 50L	4 NOS	1 KG
4	FLAT	150 X 6 X 300L	2 NOS	5 KGS
3	SQ. TUBE	40 X 40 X 2 THK X 1515L	10 NOS	37 KGS
2	SQ. TUBE	80 X 80 X 3.2 THK X 1900L	2 NOS	32 KGS
1	SQ. TUBE	80 X 80 X 3.2 THK X 1675L	2 NOS	27 KGS

This drawing & designing is the property of NIHVA TECHNOLOGIES. Not be sold or copy to any other concern.

TITLE	WICKET GATE		
	SIGN	DATE	
DRAWN	P.V.A	04.06.19	
CHECK	V.M.T	04.06.19	
REV.			
APPROVAL			
If any queries contact : design@nihva.com			
ALL DIMENSION ARE IN mm			

NIHVA TECHNOLOGIES PVT. LTD.
NIHVA TECHNOLOGY PVT. LTD. PUNE
Tel : 020 66304033
Email:- info@nihva.com
Website:- www.nihva.com

CLIENT -
PROJECT -
SITE -
DWG. NO. : NIHVA/19-20/VDR/056 | REV : R01
SCALE: NTS | WT: | SHEET: 01 OF 01