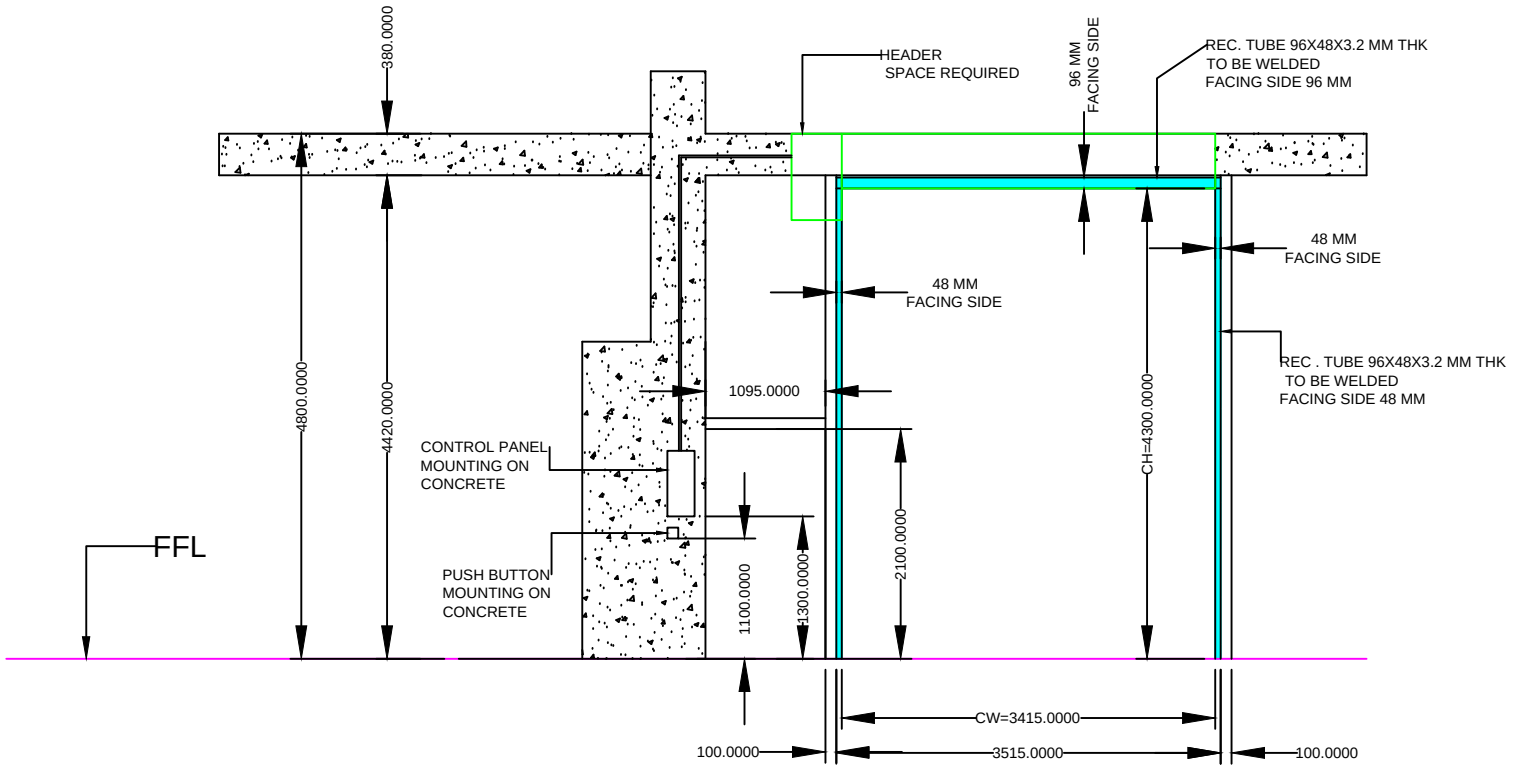

REQUIRED RECTANGULAR TUBE SIZES-
R. TUBE 96X48X3.2 MM THK L=4420 MM QTY=2
R. TUBE 96X48X3.2 MM THK L=3415 MM QTY=1

REV NO	DATE	DRAWN	REMARK
R01	7.12.2020	S.M.S.	(1) MODIFICATION IN EXISTING STRUCTURE (2) DIMENSIONS OF CW & CH CHANGED

CLEAR WIDTH (CW)	CLEAR HEIGHT (CH)	QTY
3415 MM	4300 MM	1 NO

KINDLY NOTE THAT REQUIRED MS STRUCTURE , FITTING & ALL CIVIL WORK IN CLIENT SCOPE .

This drawing & design is the property of NIHVA TECHNOLOGIES. Not to be sold or copied to any other concern.

TITLE- HIGH SPEED DOOR
M.S. STRUCTURE

NIHVA TECHNOLOGIES PVT. LTD.
NIHVA TECHNOLOGIES PVT. LTD. PUNE
Tel : 020 66304033
Email:- info@nihva.com
Website:- www.nihva.com

	NAME	SIGN	DATE
DRAWN	SIDDHESHWAR		3.12.2020
CHECK	K.P.		3.12.2020
APPRD.			

CLIENT - CONGLOMERATE
PROJECT - CONGLOMERATE
SITE LOCATION - PUNE
If any queries contact : projectsupport @nihva.com
DWG. NO. : NIHVA/20-21/0100 REV- R01
ALL DIMENSION ARE IN mm
SCALE: NTS WT: SHEET: