

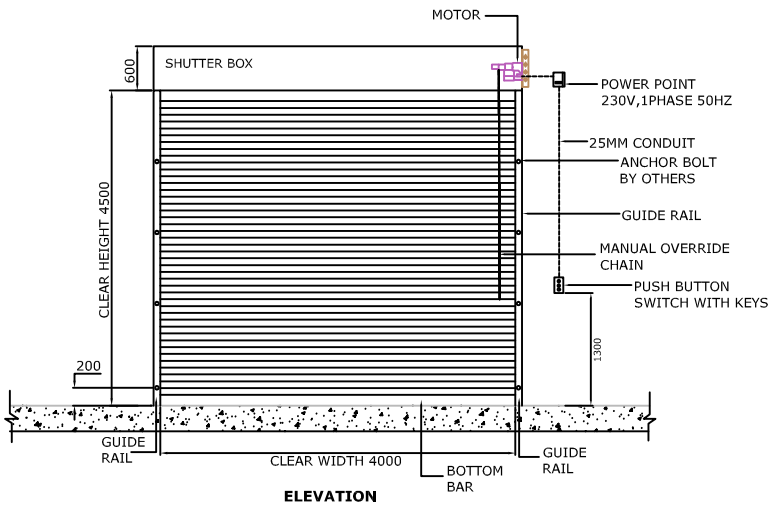



ELEVATION

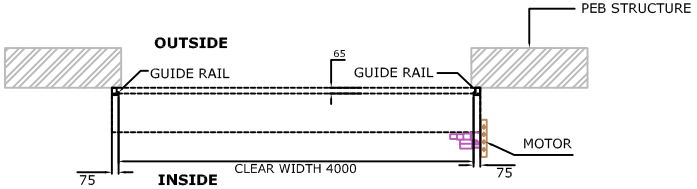


PLAN

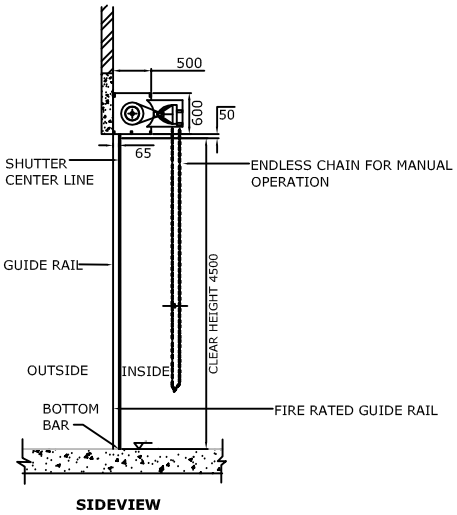


SIDEVIEW

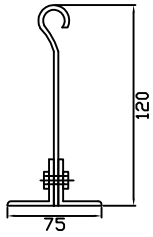

BOTTOM BAR

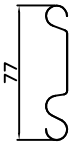

SHUTTER SLAT

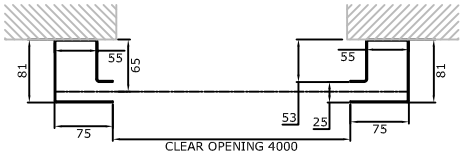

GALVANISED STEEL GUIDE RAIL

FIRE RATED SHUTTER SIZE:- 4000(W) X 4500 (H)

SHUTTER QTY :- 08 NO

SHUTTER TYPE	2 hrs FIRE RATED ROLLING SHUTTER
SHUTTER SLATS	ZINCALUME SOLID SLATS
SLATS THICKNESS	1.0 MM
GUIDE RAIL	GALVANISED SURFACE MOUNTED,3mm THICK
FINISHING OF SLATS	POWER COAT STANDARD RAL COLOUR
BOX DESIGN	MILD STEEL SECTION FRAME DESIGN
BOX COVER PLATE	0.8mm ZINCALUME STEEL SHEET
OPERATION	MOTORISE WITH MANUAL OVERRIDE CHAIN
MOTOR POWER SOURCE	230 VOLTS,1 PHASE,50HZ
PUSH BUTTON	STANDARD
FIRE MODE	WILL AUTO CLOSE VIA 71C DEGREE THERMAL FUSIBLE LINK
COLOR	POWDER COATED WITH 50 MICRON

REMARKS :-

PEB STRUCTURE MUST ABLE TO WITHSTAND THE SHUTTER WEIGHT 30KG/M2
(MINIMUM 300KGS)

LOCATION	SHUTTER NO.	CLEAR WIDTH	CLEAR HEIGHT	QUANTITY
	FRS	4000MM	4500MM	8

TITLE:

FIRE RATED ROLLING SHUTTER

DO NOT SCALE DRAWING

CLIENTS APPROVEL:-

ALL DIMENSION ARE IN M.M.

	SIGN	DATE
DRAWN ANIL		30-05-14
CHECK VT		30-05-14
ENG		
APPRD.		
PROD		
MFG		
Ref. No.		

CLIENT:

PROJECT / SITE:

PRODUCT NAME: FIRE.RATED-ROLLING.SHUTTER

DWG. NO.:

REV.: 0

SCALE: NTS WT: SHEET: 1 OF 1