
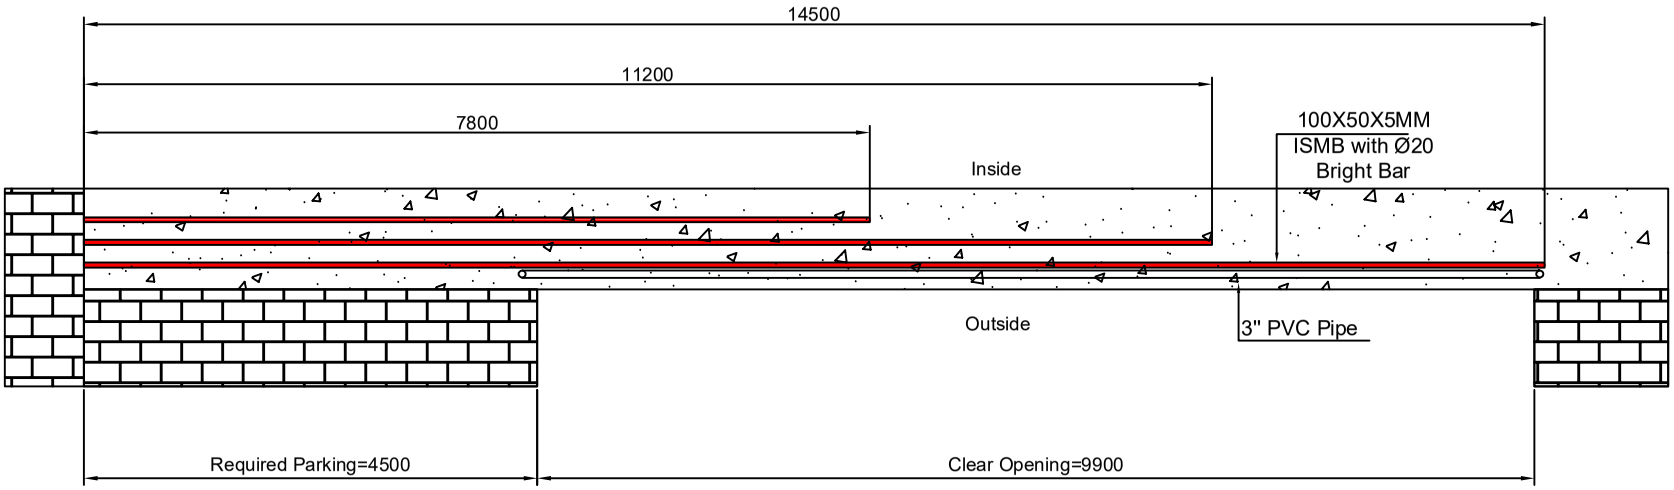


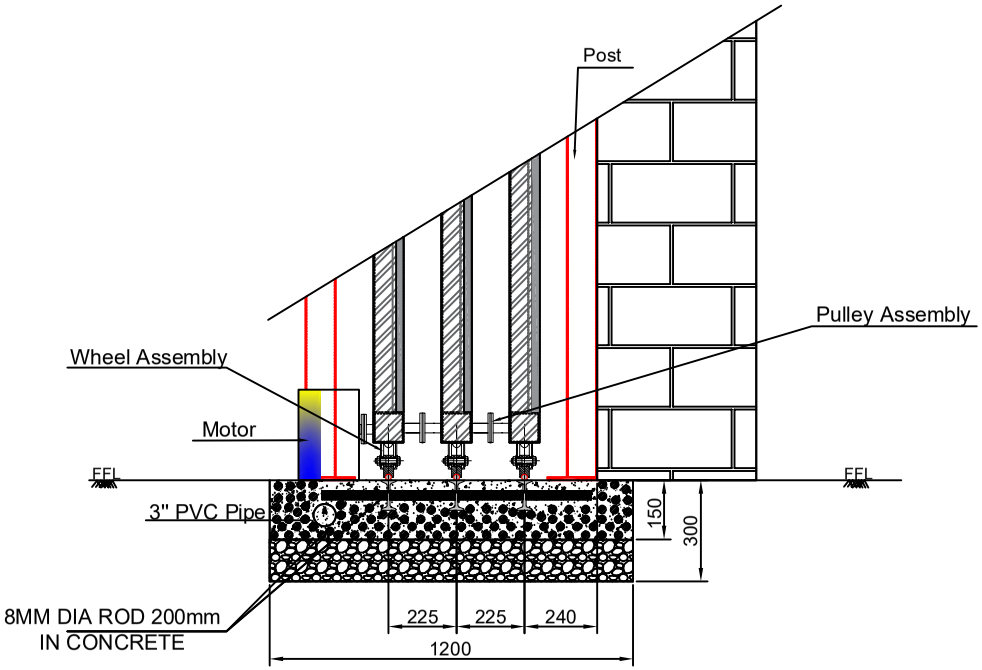

Note:-
1.All Dimension are in MM.
2.All Civil work will be in Client scope
3.Civil,Installation and Fabrication Tolerance will be ±20mm

This drawing & design is the property of NIHVA TECHNOLOGIES. Not to be sold or copied to any other concern.

TITLE:- 3L Telescopic Sliding Gate (E18,ADM)

NIHVA TECHNOLOGIES PVT. LTD.

NIHVA TECHNOLOGIES PVT. LTD. PUNE
Tel : 020 66304033
Email:- info@nihva.com
Website:- www.nihva.com

	NAME	DATE	SIGN
DRAWN	SUJATA	30/06/2022	
CHECK	A.K	30/06/2022	
APPRD.	V.T	30/06/2022	

If any queries contact : design@nihva.com

ALL DIMENSION ARE IN mm

CLIENT - OC Specialities

LOCATION - Solapur

PRODUCT - Telescopic Sliding Gate | QTY-01

DWG NO:- NIHVA/22-23/CLT/0050_2 | REV- 0

SCALE: NTS | SCALE:-- 1:1 | SHEET: 01 OF 01

Rev No.	Revision	Date	Revised By
1.	Civil Details Has Been Added	09/07/2022	Sujata