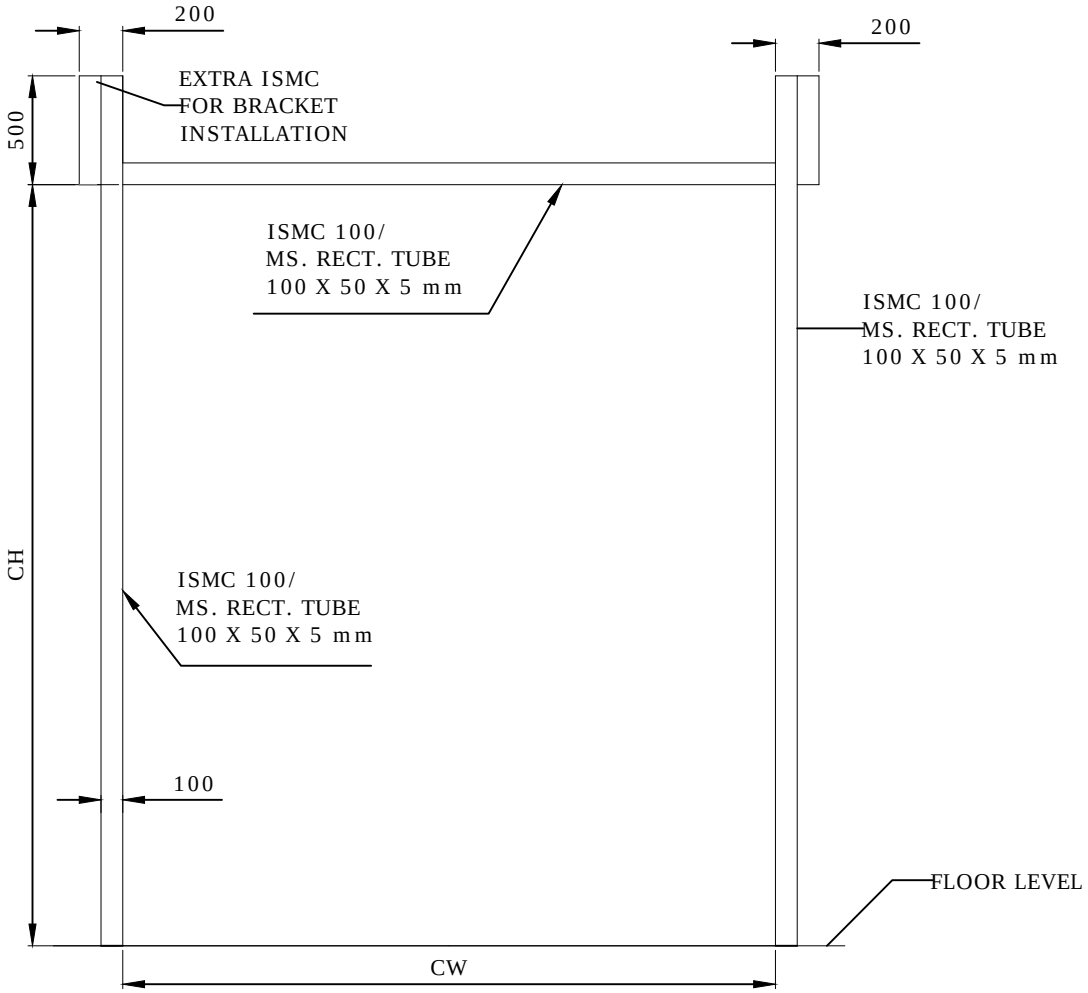

ELEVATION

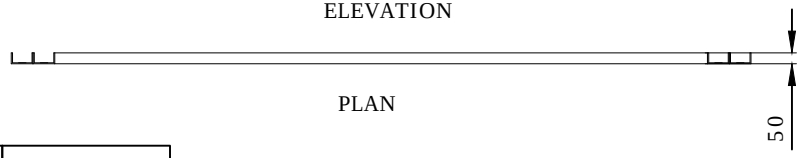

PLAN

CLEAR WIDTH (CW)	CLEAR HEIGHT (CH)	QUANTITY
3000	3000	1
4000	4000	1

This drawing & designing is the property of NIHVA TECHNOLOGIES. Not to be sold or copied to any other concern.

TITLE
STRUCTURE DETAILS FOR ROLLING SHUTTER

	SIGN	DATE
DRAWN	OMKAR	02.06.18
CHECK	SHEKHAR	02.06.18
APPROVAL	SHEKHAR	02.06.18
MFG.		

If any queries contact : design@nihva.com

ALL DIMENSION ARE IN mm

NIHVA TECHNOLOGIES PVT. LTD.
NIHVA TECHNOLOGIES PVT. LTD. PUNE
Tel : 020 66304033
Email:- info@nihva.com
Website:- www.nihva.com

CLIENT - Shapoorji Pallonji and Co.Pvt Ltd
PROJECT -
SITE -
DWG. NO. : NIHVA/18-19/0052 | REV-0
SCALE: NTS | WT: | SHEET: 01 OF 01