


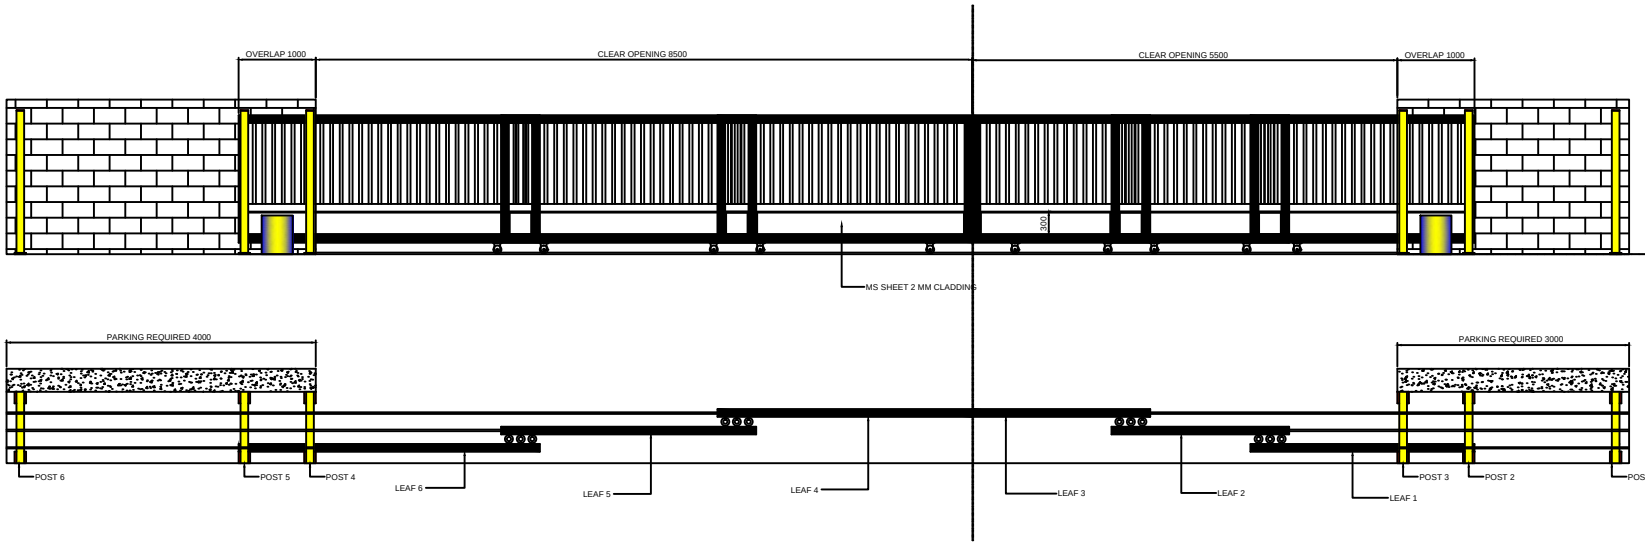


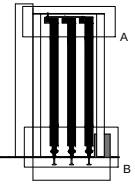

SIDE VIEW

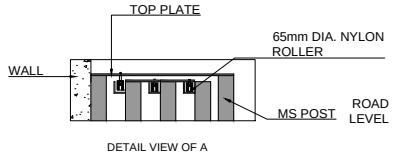

DETAIL VIEW OF A

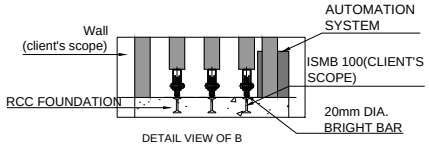

DETAIL VIEW OF B

Note-

1. All dimension are in mm.
2. All civil work is under client scope.
3. ISMB in the foundation will be provided by the client.
4. 3" PVC pipe in the foundation to be provided by client.

GATE WIDTH	GATE HEIGHT	QUANTITY	LOCATION
8500mm	1800mm	1 NOS	
5500mm	1800mm	1 NOS	

This drawing & design is the property of NIHVA TECHNOLOGIES. Not to be sold or copied to any other concern.

TITLE
AUTOMATIC THREE LEAF
BI-PARTING TELESCOPIC GATE

NIHVA TECHNOLOGIES PVT. LTD.

NIHVA TECHNOLOGIES
PVT. LTD. PUNE
Tel : 020 66304033
Email:- info@nihva.com
Website:- www.nihva.com

	NAME	DATE
DRAWN	G.I.P.	18/08/21
CHECK	A.K.	18/08/21
REV.	00	
APPROVAL	V.T.	18/08/21

If any queries contact : design@nihva.com

ALL DIMENSION ARE IN mm

CLIENT - LUPIN LIMITED

PROJECT -

SITE LOCATION - GHOTAWADE

DWG. NO. : NIHVA/21-22/0213

SCALE: NTS | WT: | SHEET: 01 OF 01