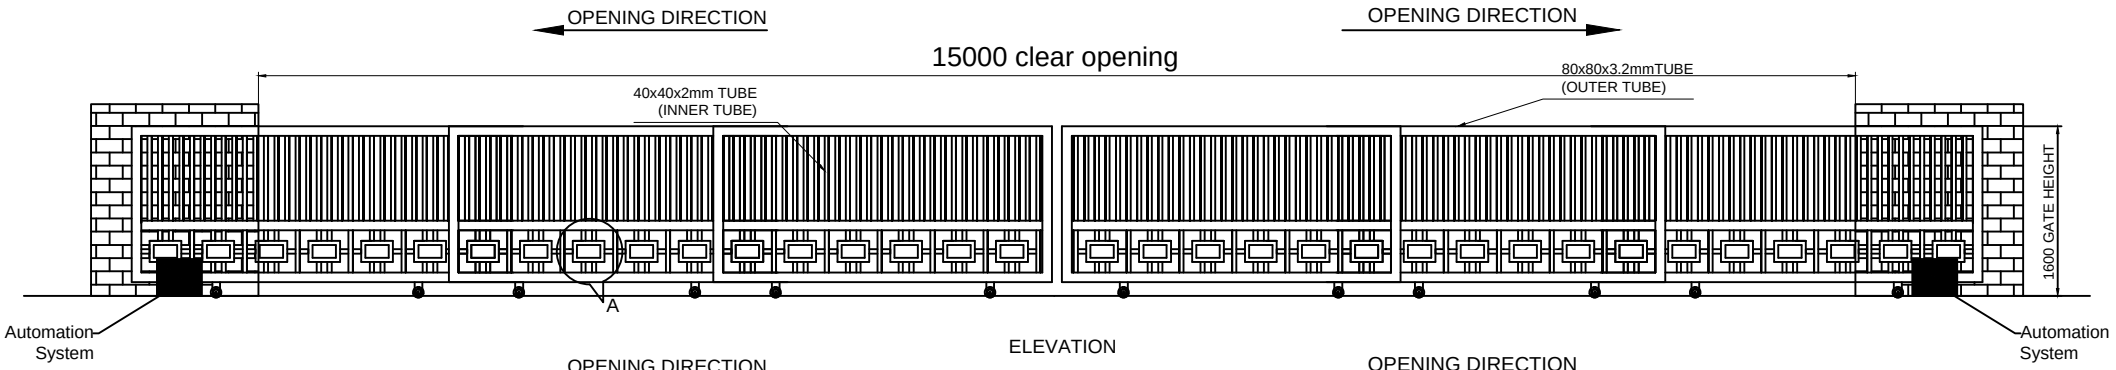

ELEVATION

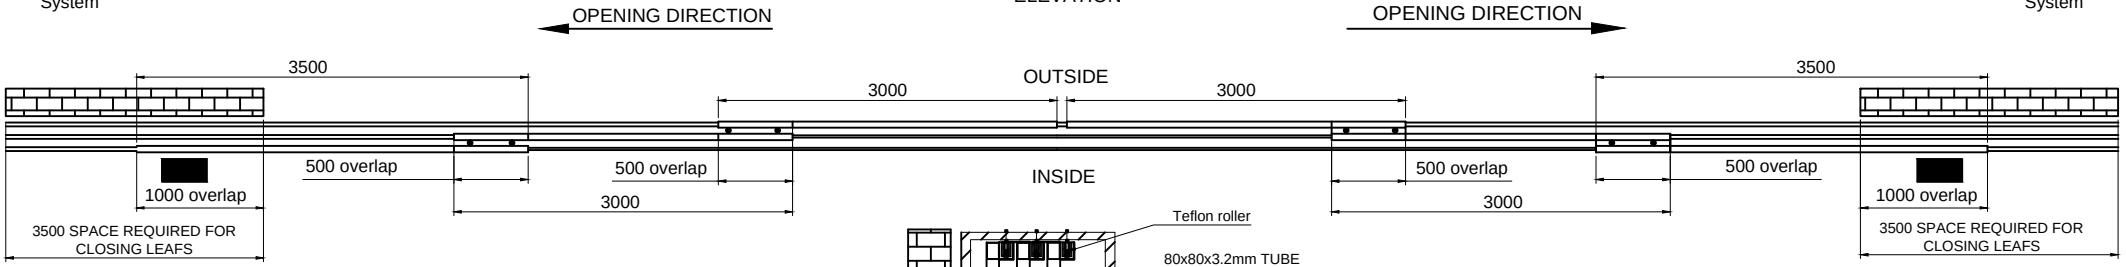

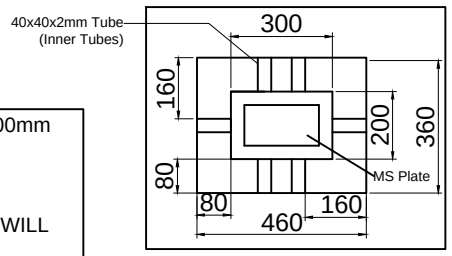

DETAILED VIEW OF A

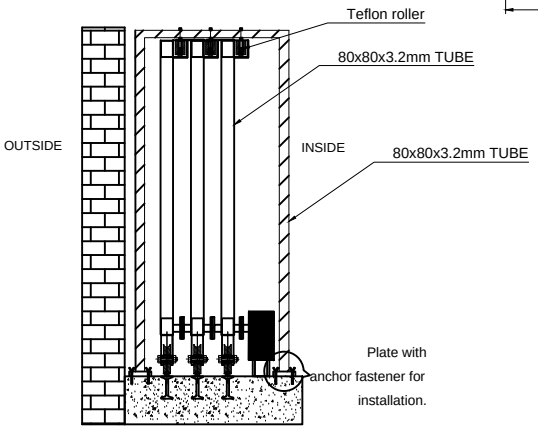

Clear Opening size -15000mm x 1600mm
Total No. of Leaf - 6 Leaf
Outer Tube Size-80x80x3.2mm
Inner Tube Size-40x40x2mm
NOTE :- *ALL REQ. CIVIL WORK WILL BE IN CLIENT SCOPE.

This drawing & designing is the property of NIHVA TECHNOLOGIES. Not be sold or copy to any other concern.

TITLE: TELESCOPIC SLIDING GATE		
	SIGN	DATE
DRAWN	OMKAR	23/03/16
CHECK	ANIL	23/03/16
REV.	01	
APPROVAL		
If any queries contact : projects@nihva.com		
ALL DIMENSION ARE IN mm		

NIHVA TECHNOLOGIES PVT. LTD.
NIHVA TECHNOLOGY PVT. LTD. PUNE
Tel : 020 66304033
Email:- info@nihva.com
Website:- www.nihva.com

CLIENT - TAIIN STEEL FAB & INFRA PVT.LTD.		
PROJECT - HYOSUNG T&D		
SITE -		
DWG. NO. : NIHVA/15-16/226		
SCALE: 01	WT:	SHEET: 01 OF 01