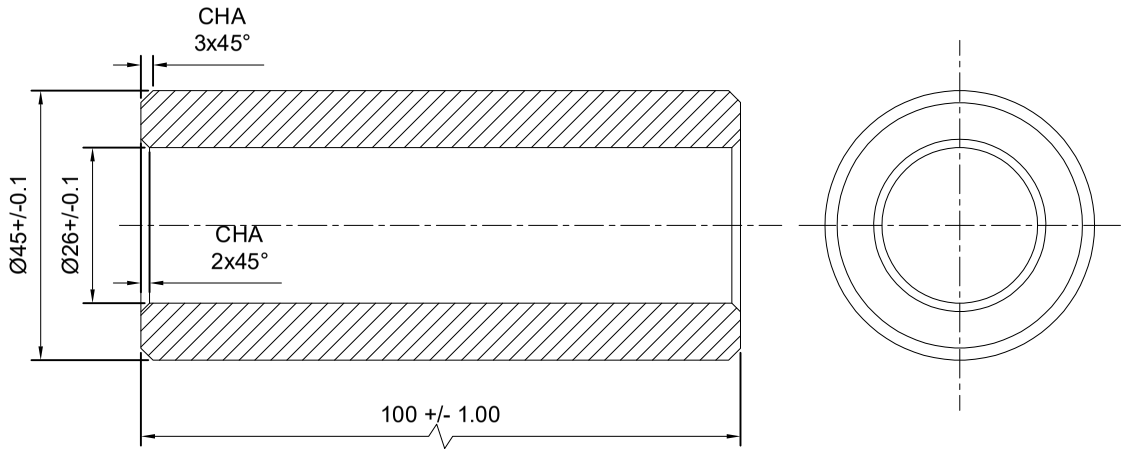


NOTE:~ MTL : MS

BUSH Ø45 X 100L = 80NOS

NOTE : ~ PLEASE MAINTAIN 7 MM GAP BETWEEN TWO LIP BUSHES.

This drawing & design is the property of NIHVA TECHNOLOGIES. Not to be sold or copied to any other concern.

TITLE				NIHVA TECHNOLOGIES PVT. LTD. PUNE
LIP MOUNTING BUSH				Tel : 020 66304033
	NAME	DATE	SIGN	Email:- info@nihva.com
DRAWN	SUJATA	17/04/2023		Website:- www.nihva.com
CHECK	A.K	17/04/2023		CLIENT - NIHVA TECHNOLOGIES PVT LTD
APPRD.	V.T	17/04/2023		PROJECT - DL
				SITE LOCATION - PUNE
If any queries contact : design1@nihva.com				DWG. NO. : NIHVA/23-24/VDR/0118
ALL DIMENSION ARE IN mm				SCALE: NTS / WT: / REV- 0