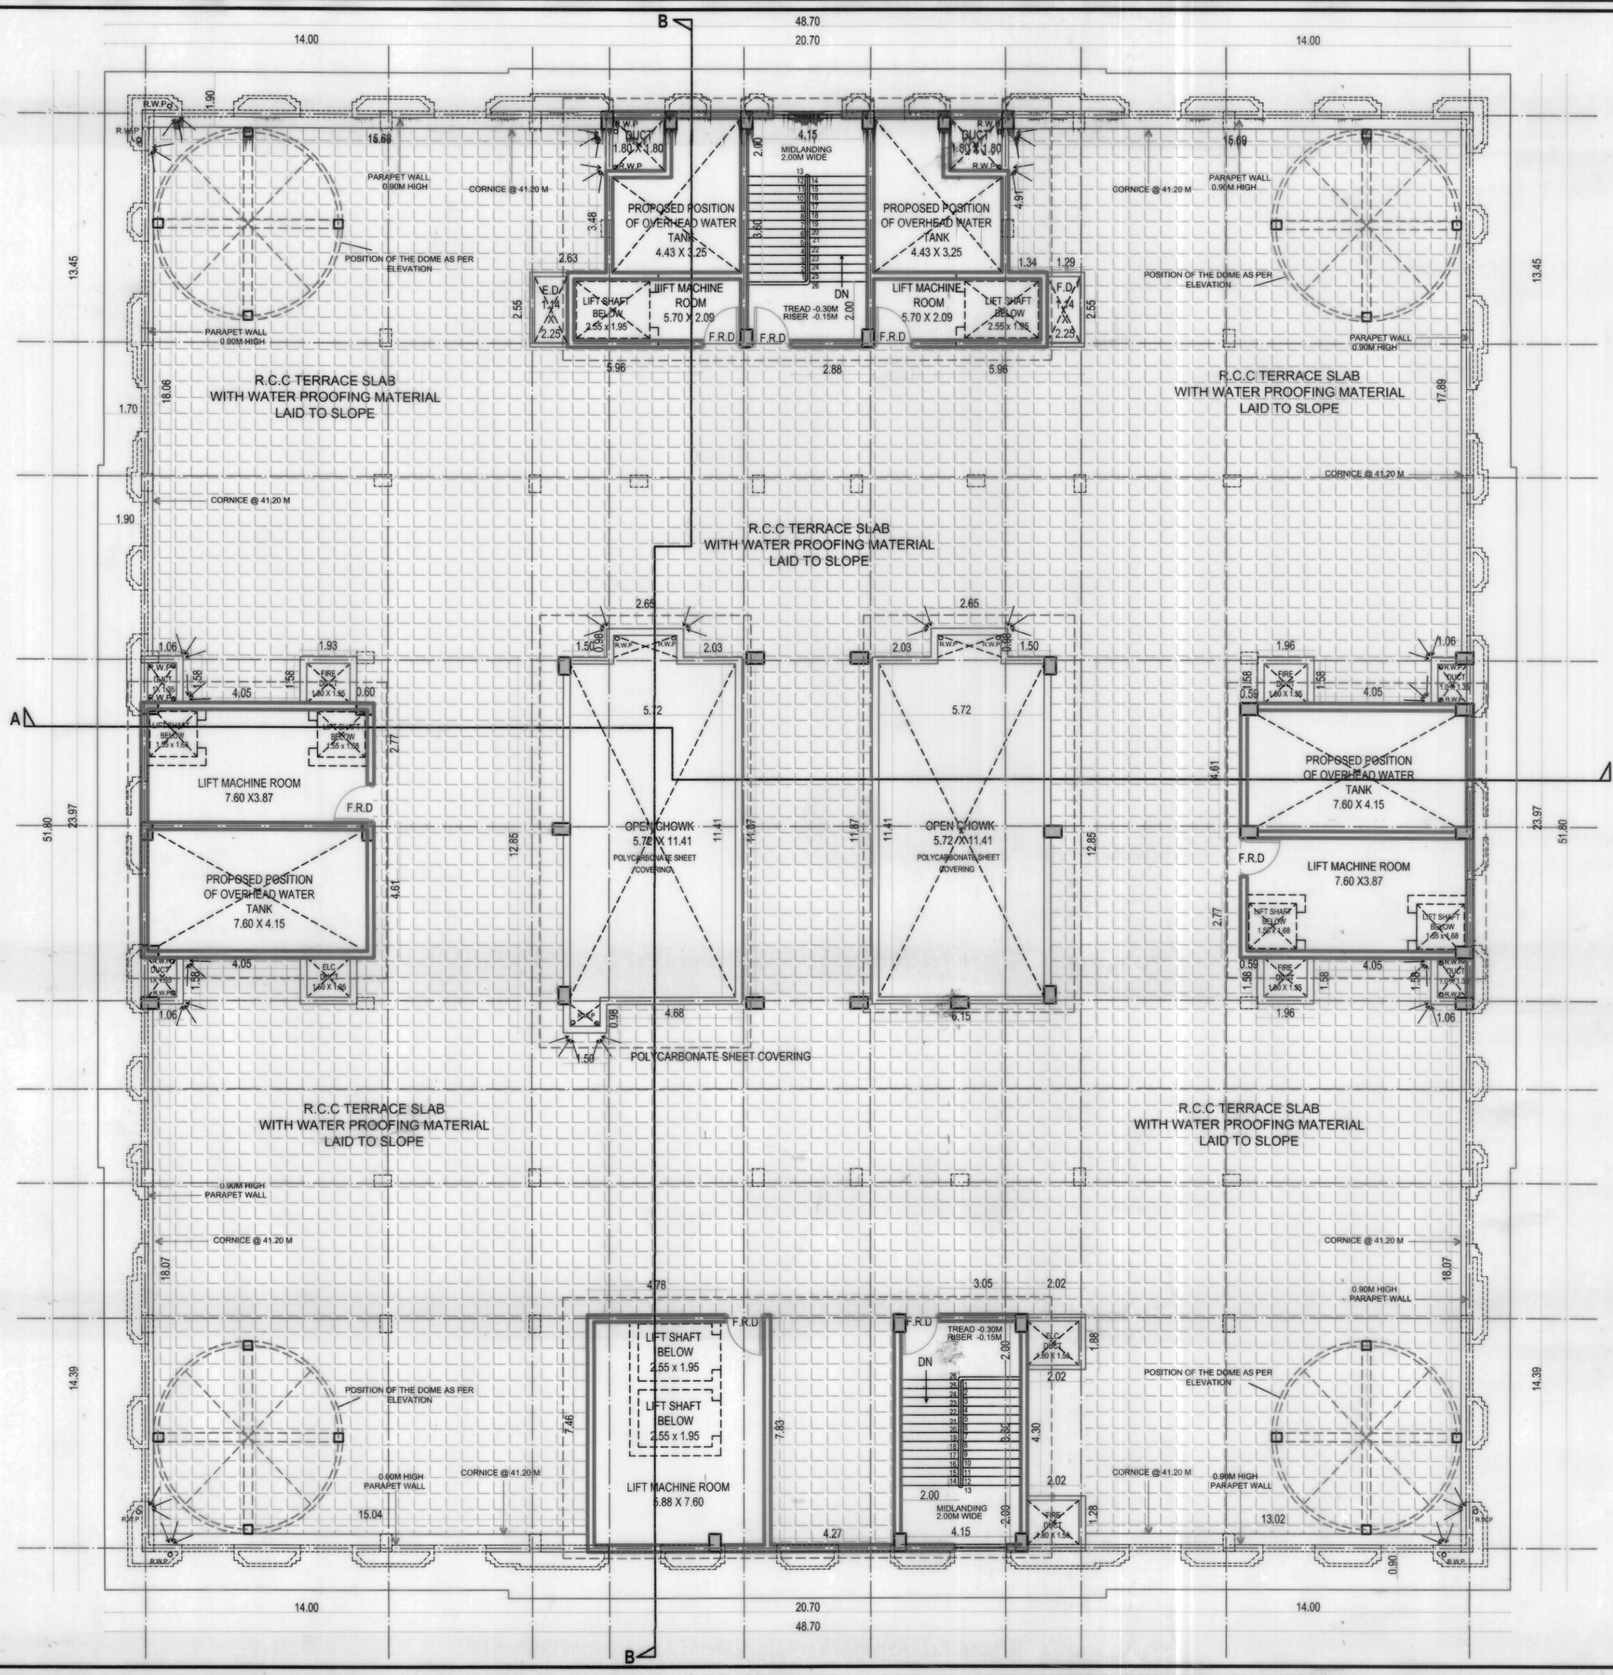


NOTES:

- ANY DISCREPANCY NOTICED IN THIS DRG. SHALL BE BROUGHT TO THE NOTICE OF THE CHIEF ARCHITECT, M.S., P.W.D., MUMBAI , BEFORE EXECUTION OF WORK.
- ALL DIMENSIONS ARE IN MTS. EXCEPT WHEREVER MENTIONED BY UNITS.
- ONLY WRITTEN DIMENSIONS ARE TO BE FOLLOWED.
- ALL SIZES OF DOORS, WINDOWS & VENTILATOR ARE INCLUSIVE OF FRAMES.
- ALL DOOR HTS. ARE FROM FINISHED FLOOR LEVEL.
- FINISHED FLOOR LEVELS OF TOILETS AND BALCONIES SHALL BE SUNK BY 1.5 CMS. THAN THE GENERAL FLOOR LEVEL.
- OVERALL SIZES OF R.C.C COLUMNS AND BEAMS ARE APPROX. AND MAY VARY ACCORDING TO THE STRUCTURAL DESIGN.
- PLANS SHOULD BE GOT APPROVED FROM CONCERNED LOCAL AUTHORITY BEFORE EXECUTION.
- DATE OF COMMENCEMENT AND DATE OF COMPLETION OF WORK SHALL BE INFORMED TO THIS OFFICE ATLEAST TWO WEEKS IN ADVANCE.

SR. NO.	DATE	SIGN.	CONTENTS

REVISIONS

OFFICE OF
THE CHIEF ARCHITECT,
MAHARASHTRA STATE,
P.W.D., MUMBAI.
25,MURZBAN ROAD,
FORT, MUMBAI.

S.W. GEDAAM (CA/90/13011)
CHIEF ARCHITECT(I.C)

Y.N . DESHPANDE (CA/92/15391)
DY. CHIEF ARCHITECT

S.S. GANGAN (CA/05/36805)
ARCHITECT

PROPOSED THANE COURT BLDG. STILT+8 FLR.(22 NOS. COURTS) ON PLOT NO. 32,33 IN THE PREMISES OF DIST. & SESSIONS COURT BUILDING AT THANE.

WORKING DRAWINGS
(FOR R.C.C. & ESTIMATE PURPOSE ONLY)

TERRACE PLAN

1 : 100	5·11·19	
SCALE	DATE	DEALT BY

TNE/231/II	172
JOB NO.	DRG. NO.