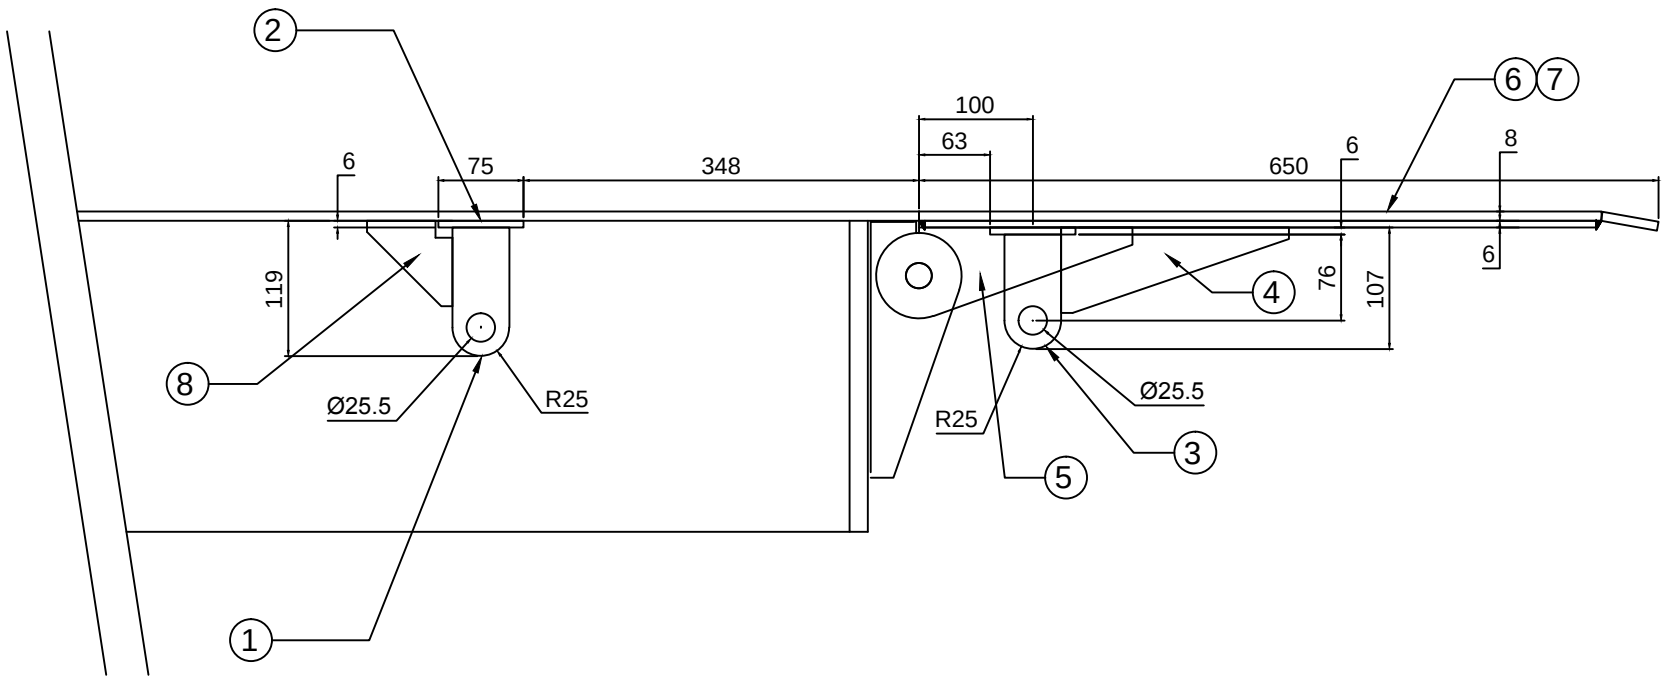


SR NO	DESCRIPTION	SPECIFICATION	QTY
15	FLAT	75 X 5 X 150L	4 NOS
14	FLAT	75 X 10 X 150L	4 NOS
13	SPLIT PIN	3 MM THK X 50L	10 NOS
12	WASHER	ID25 X 3 THK	4 NOS
11	BANDED SEAL		2+ 2 NOS
10	ADAPTOR	3/8 X 1/4	2 NOS
9	STD LIP CYL	BORE 50	1 NO
8	PROFILE	75 X 12 X 75L	4 NOS
7	CHEQ. SHEET	650 X 8 X 2000L	1 NO
6	PLAIN SHEET	590 X 6 X 2000L	1 NO
5	PROFILE	80 X 12 X 225L	16 NOS
4	PROFILE	75 X 12 X 200L	2 NOS
3	PROFILE	50 X 12 X 100L	2 NOS
2	FLAT	75 X 6 X 100L	2 NOS
1	PROFILE	50 X 12 X 113L	2 NOS

NOTE : REMOVE OLD DOCK LIP CYLINDER.

This drawing & design is the property of NIHVA TECHNOLOGIES. Not to be sold or copied to any other concern.

TITLE
DOCK LIP MODIFICATION

	NAME	SIGN	DATE
DRAWN	P.V.A		04.07.19
CHECK	V.M.T		04.07.19
APPV'ED			

If any queries contact : design@nihva.com

ALL DIMENSION ARE IN mm

NIHVA
NIHVA TECHNOLOGIES PVT. LTD.
NIHVA TECHNOLOGIES PVT. LTD. PUNE
Tel : 020 66304033
Email:- info@nihva.com
Website:- www.nihva.com

CLIENT :-
PROJECT :-
LOCATION :-
DWG. NO. :- NIHVA/19-20/VDR/102 REV.:-00
SCALE: NTS WT: SHEET: 01 OF 01