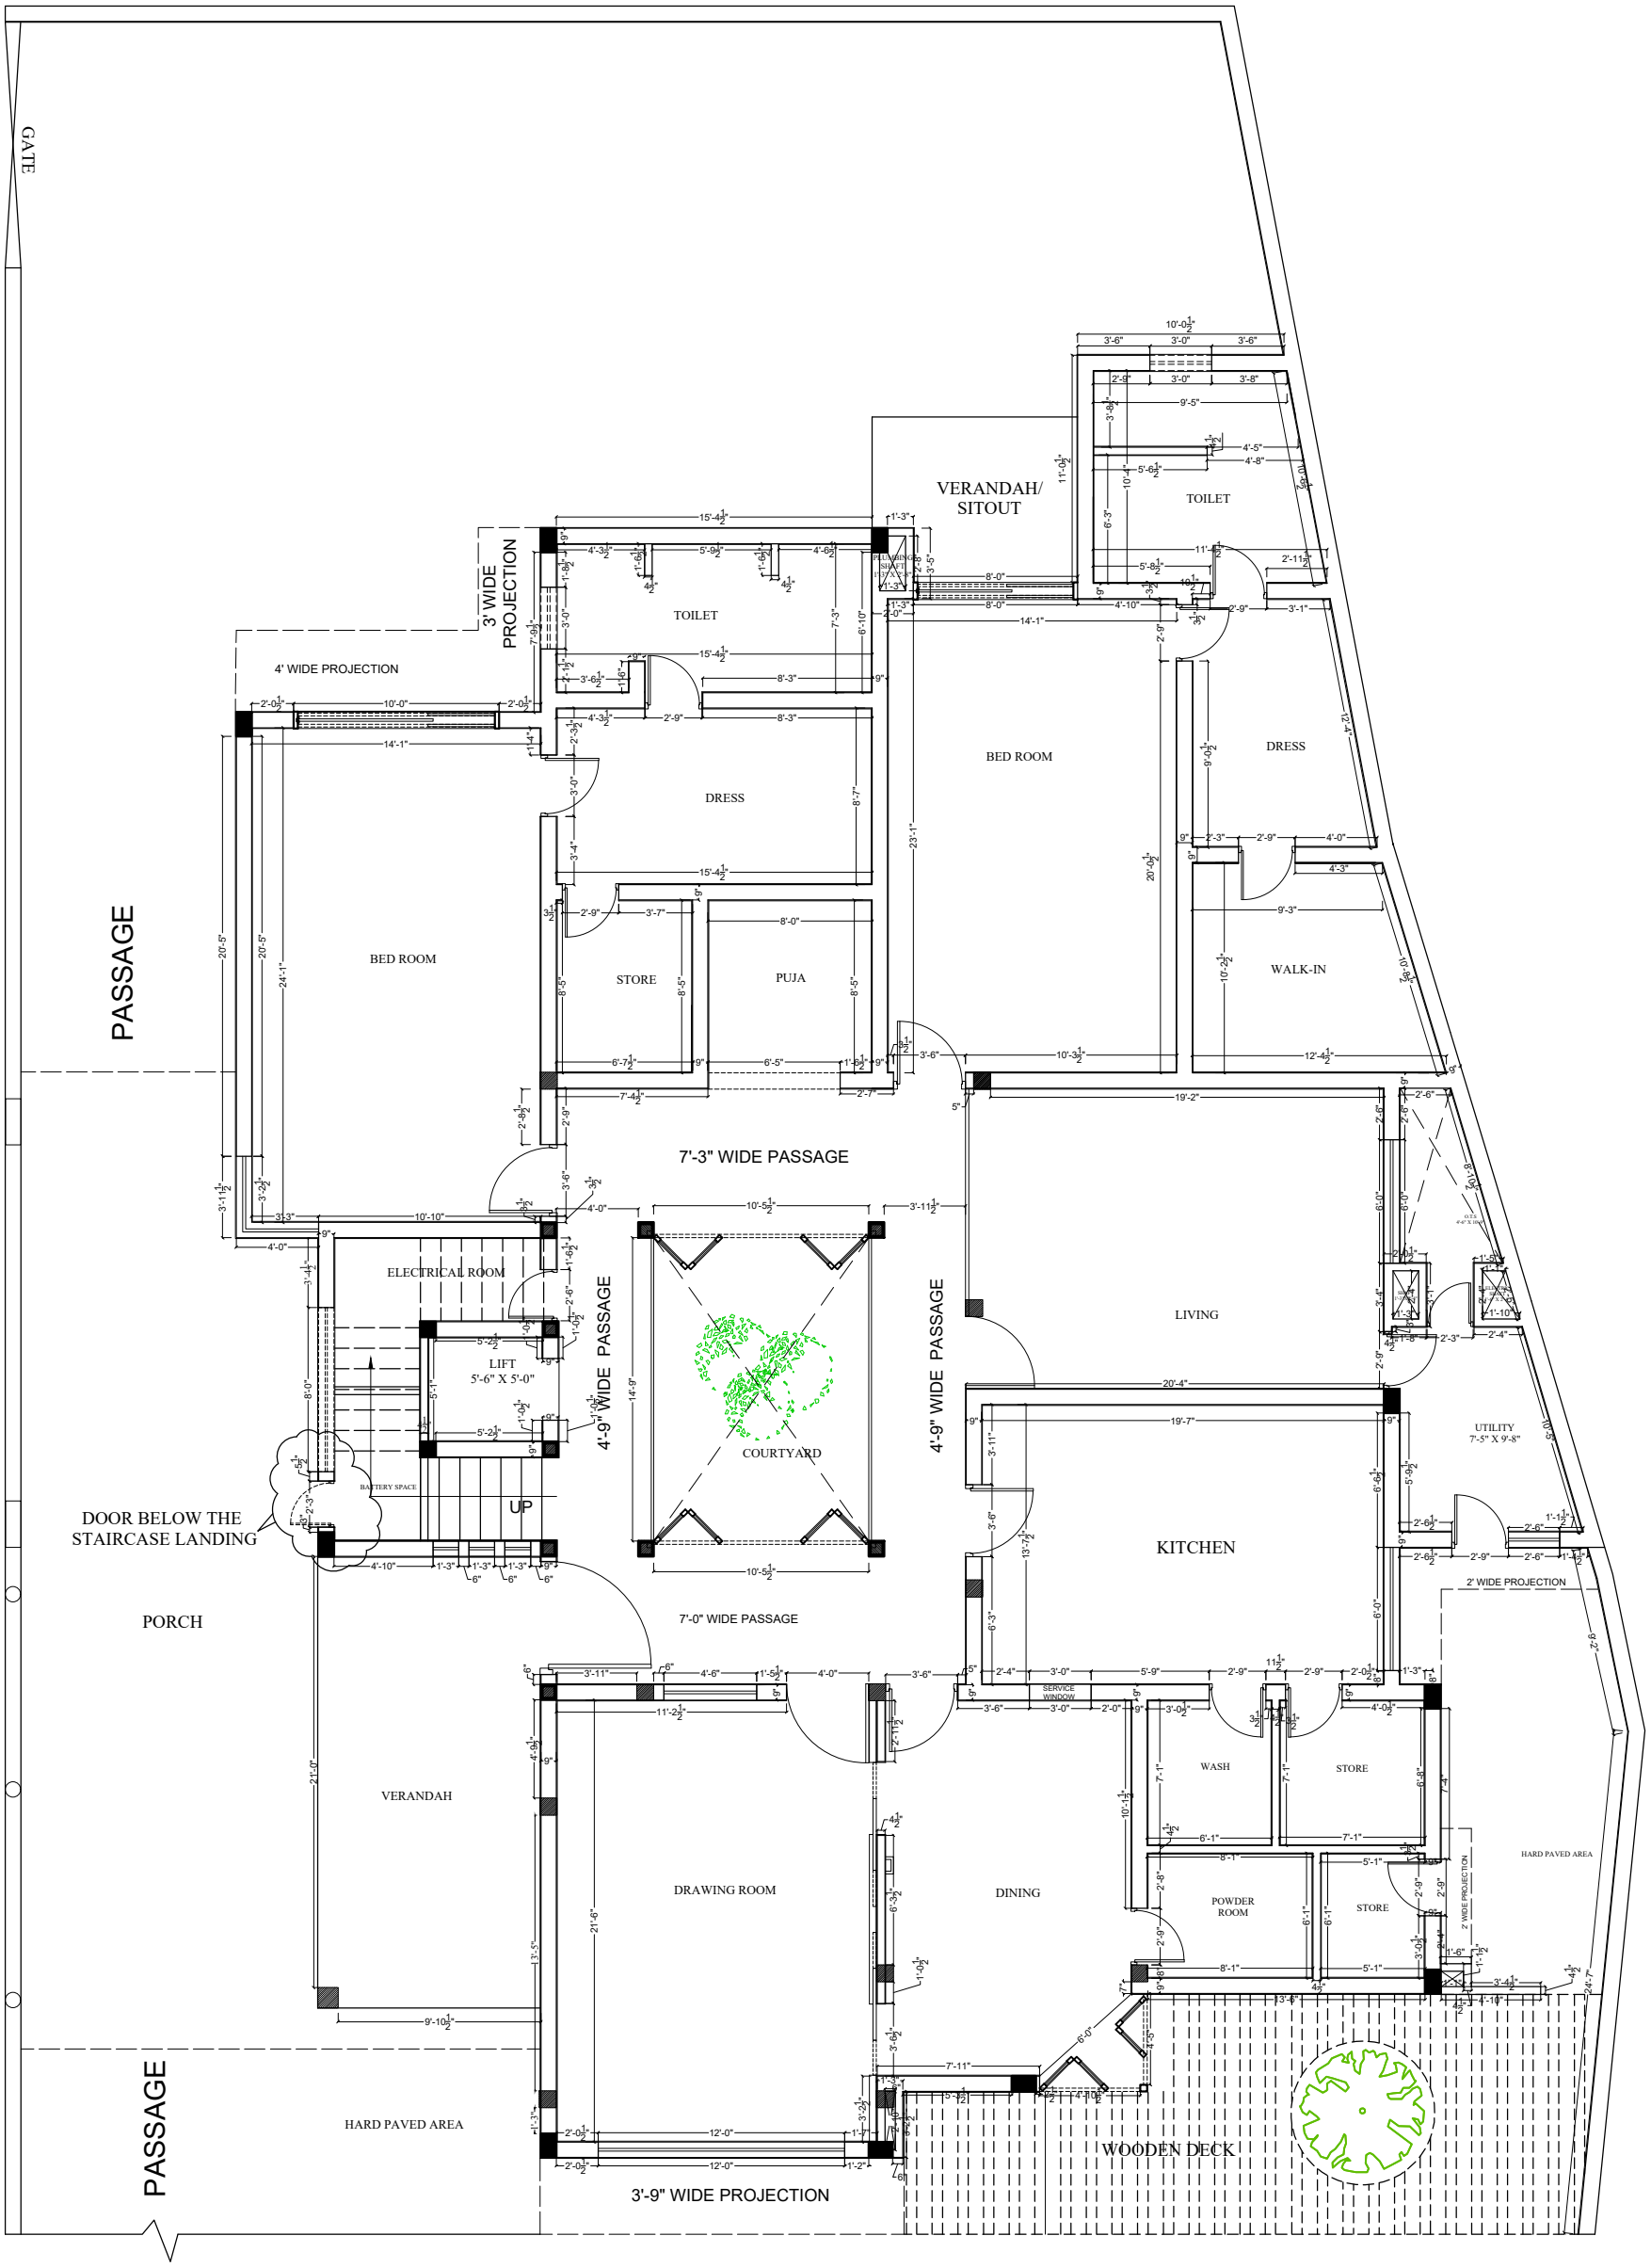


REV NO.	DATE :	REMARKS :
R4	14.09.2022	

PROJECT NAME & ADDRESS :

RESIDENCE AT BAGHPAT ROAD, MEERUT

OWNER NAMES :

Mr. SUBHENDRA MITTAL

CONSULTANTS NAME & ADDRESS :

Acro Ventures Pvt. Ltd.

First Floor, S2S, Nirmal Arcade 47, Near Hotel Harmony Inn, Garh Road, Meerut- 250004 **(Uttar Pradesh)**
K-1/ 39, Lower Ground Floor,
Chitteranjan Park, New Delhi-110019
Ph: 0121-4053301-03, Fax 0121-4053304
@: info@acroventures.in

DEALT :	OWNER'S SIGN:
Ar. Ankit Agarwal	

BUILDING NAME :

ADDITION/ALTERATION RESIDENCE

DRAWING TITLE :

WORKING DRAWING GROUND FLOOR

DEALT :	CHECKED :
Ar. Saloni	Ar. Harshit
DRG. NO. R4	DATE : 14.09.2022