



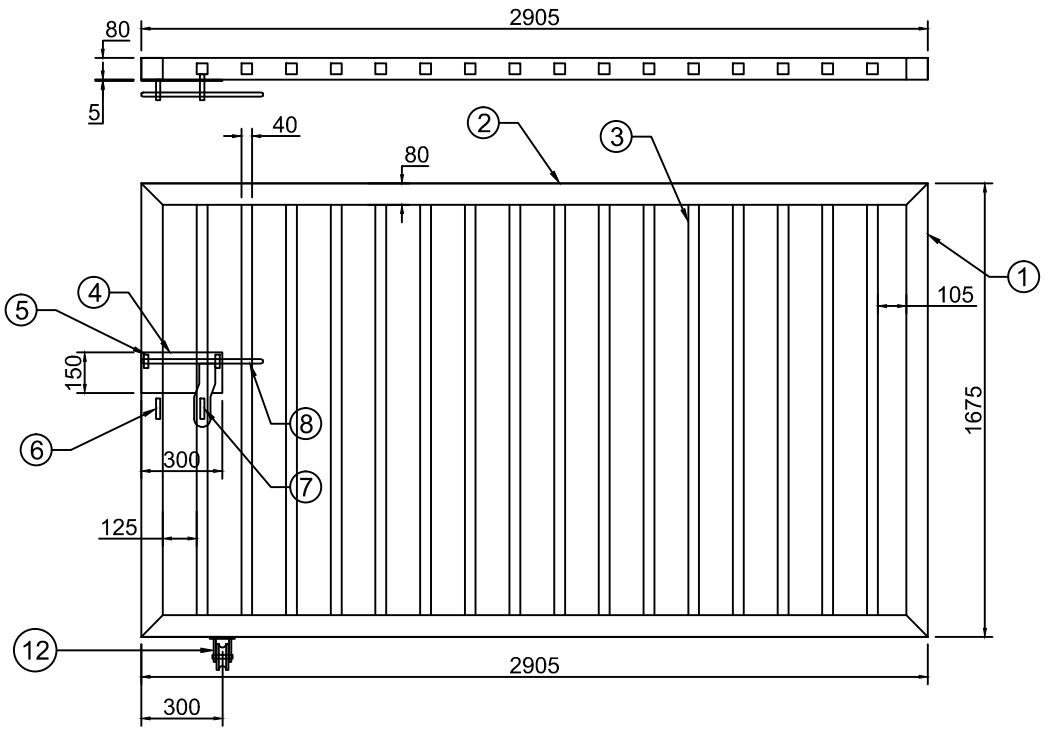


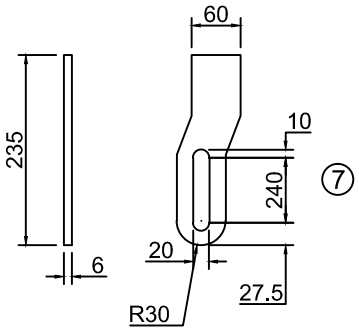

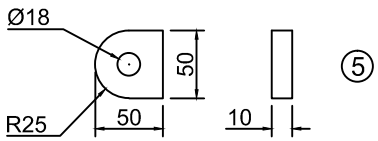

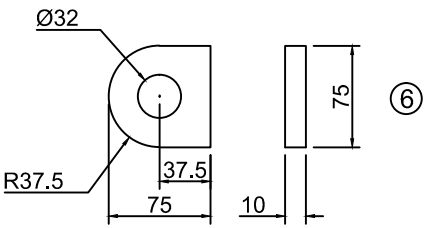

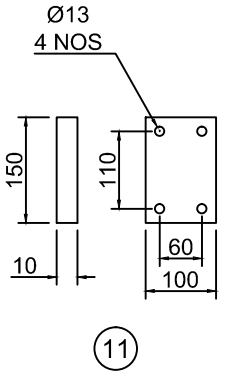

SR.NO	DESCRIPTION	SPECIFICATION	QTY	WEIGHT
12	WHEEL & BKT	STD 4 " WHEEL & BRACKET ASSEMBLY	2 NOS	
11	FLAT	100 X 10 X 150L	2 NOS	2 KGS
10	HINGE BEARING	4" BEARING HINGES (4 THRUST + 4 BALL BEARING SET)	2 NOS	
9	ISMC	75 X 40 X 200L	2 NOS	3 KGS
8	M.S ROD	Ø16 X 450L	2 NOS	1.5 KGS
7	PROFILE	60 X 6 X 235L	2 NOS	2 KGS
6	PROFILE	75 X 10 X 75L	4 NOS	2 KGS
5	PROFILE	50 X 10 X 50L	4 NOS	1 KG
4	FLAT	150 X 6 X 300L	2 NOS	5 KGS
3	SQ. TUBE	40 X 40 X 2 THK X 1515L	16 NOS	60 KGS
2	SQ. TUBE	80 X 80 X 3.2 THK X 2905L	2 NOS	48 KGS
1	SQ. TUBE	80 X 80 X 3.2 THK X 1675L	2 NOS	27 KGS

LEAF QTY : 4 NOS
GATE QTY : 2 NOS

This drawing & designing is the property of NIHVA TECHNOLOGIES. Not be sold or copy to any other concern.

TITLE: SWING GATE

NIHVA TECHNOLOGIES PVT. LTD.
NIHVA TECHNOLOGY PVT. LTD. PUNE
Tel : 020 66304033
Email:- info@nihva.com
Website:- www.nihva.com

	SIGN	DATE
DRAWN	P.V.A	04.06.19
CHECK	V.M.T	04.06.19
REV.		
APPROVAL		

If any queries contact : design@nihva.com

ALL DIMENSION ARE IN mm

CLIENT -
PROJECT -
SITE -
DWG. NO. : NIHVA/19-20/VDR/057 | REV : R01
SCALE: NTS | WT: | SHEET: 01 OF 01