





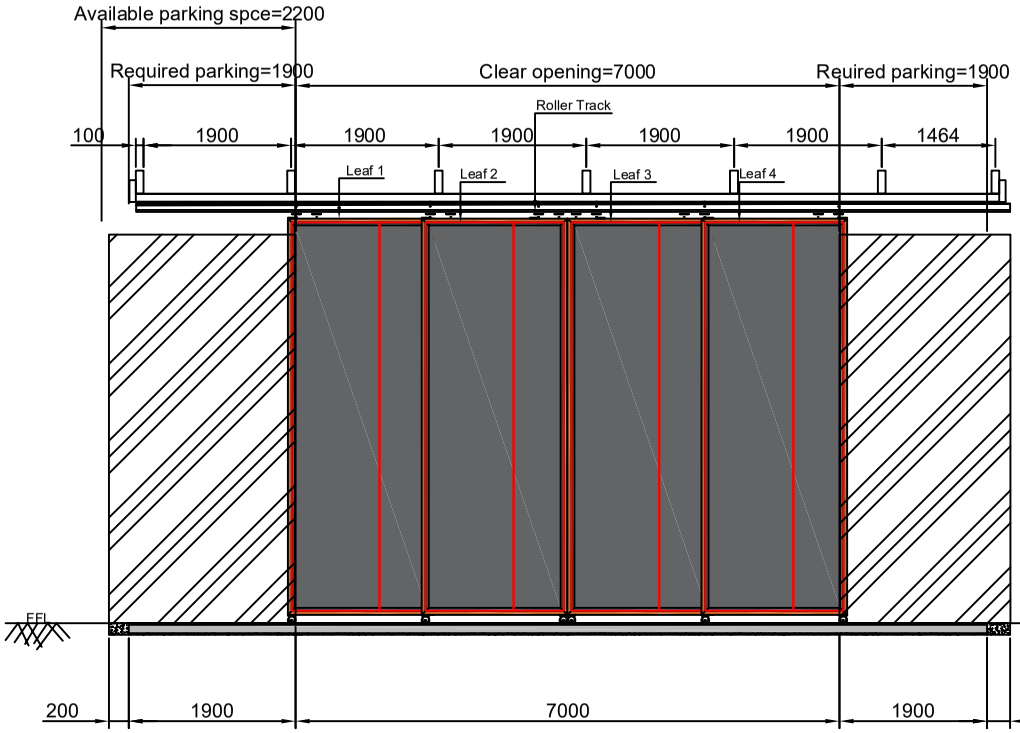

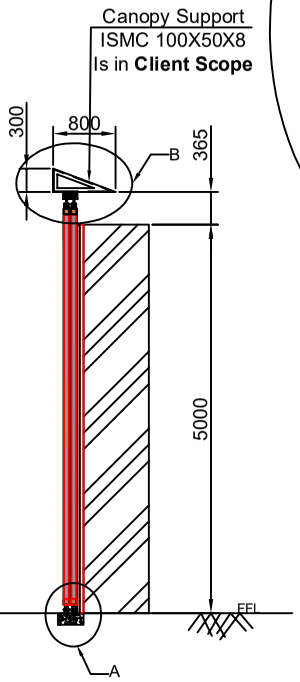

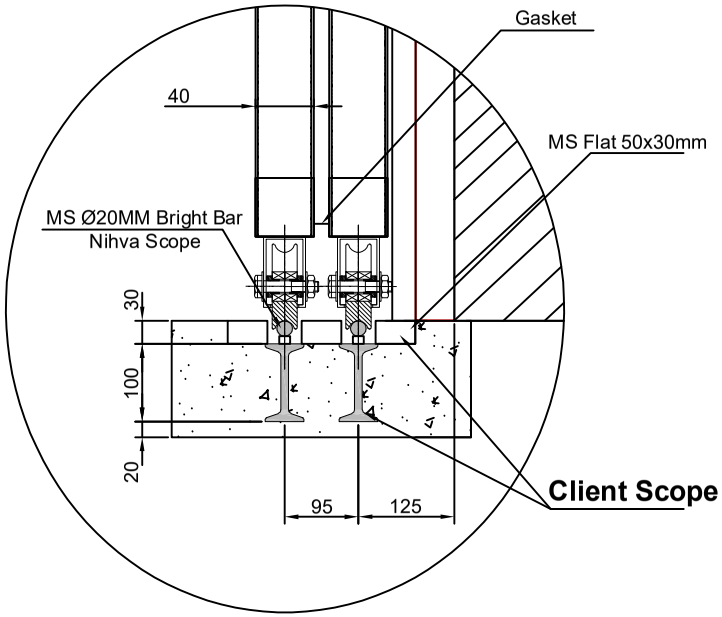

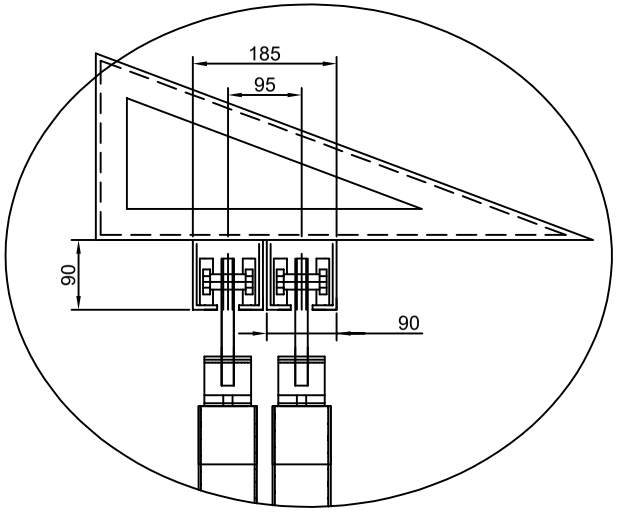

Client scope
*Roof need to be shift at top Approx 300mm *Drainage area need to be remove frome left side appox.200mm *Gutter area need to be remove *Civil foundation need to be done for tracks

Color code	Color	Approval
9002	Offwhite	
5012	Lightblue	

Note:-
1.All dimension are in MM
2.Manufacturing,civil and installation tolerance will be ±10mm
3.Top and Bottom track should be in parallal within ±3mm

Rev No.	Revision	Date	Revised By

This drawing & design is the property of NIHVA TECHNOLOGIES. Not to be sold or copied to any other concern.

TITLE:-4LEAF BOTH SIDE SLIDING
CRM DOOR-10

	NAME	DATE	SIGN
DRAWN	SUJATA	30/04/2022	
CHECK	M.SUTAR	30/04/2022	
APPRD.	V.TARAK	30/04/2022	

If any queries contact : design@nihva.com

ALL DIMENSION ARE IN mm

NIHVA
NIHVA TECHNOLOGIES PVT. LTD.

NIHVA TECHNOLOGIES PVT. LTD. PUNE
Tel : 020 66304033
Email:- info@nihva.com
Website:- www.nihva.com

CLIENT - LESTECH
LOCATION - POSCO MANGAON
PRODUCT - SLIDING DOOR
DWG NO:-NIHVA/22-23/CLT/0017 | REV- 0
SCALE: NTS | SCALE:-- 1:1 | SHEET: 01 OF 01