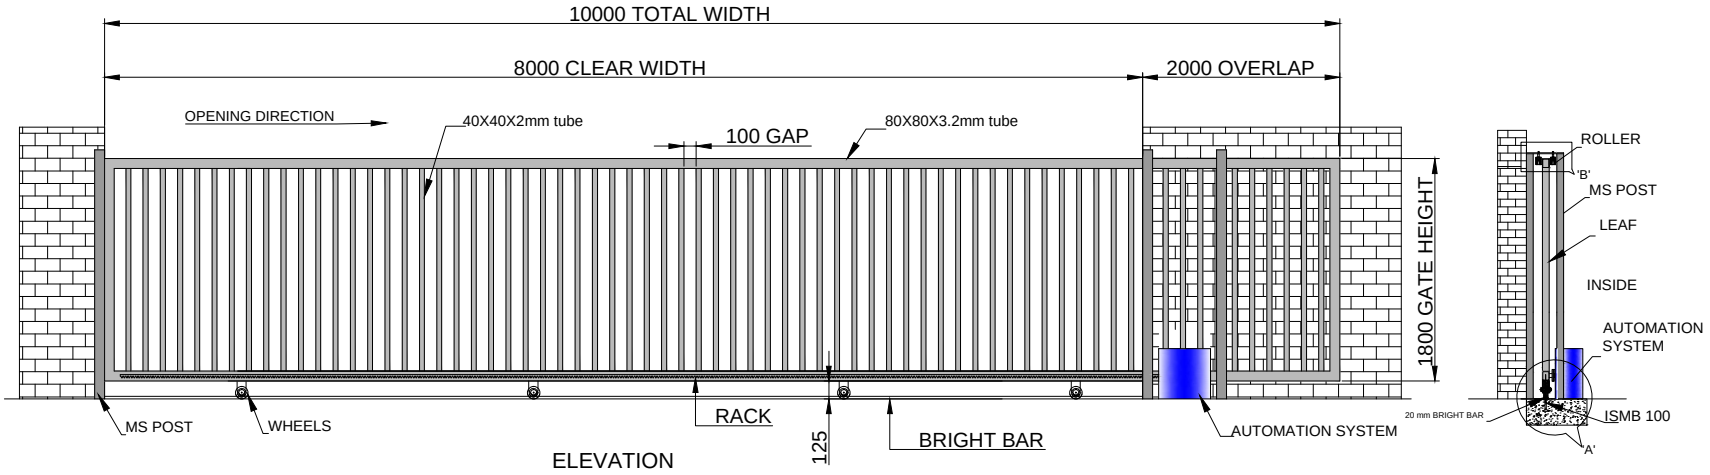
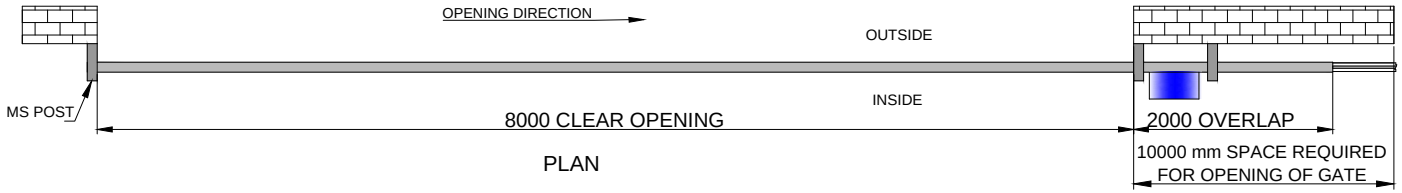
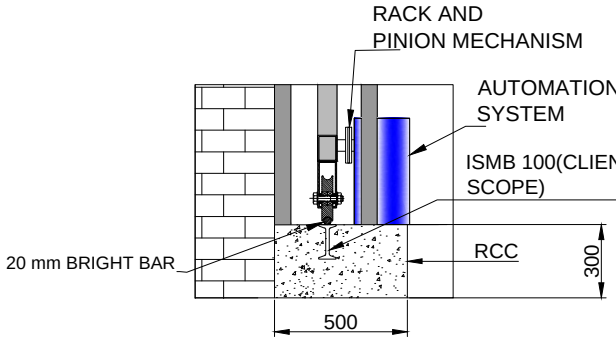


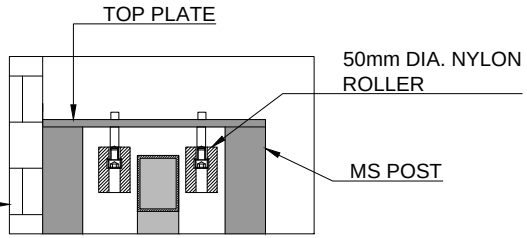

ELEVATION




PLAN




DETAIL VIEW OF A




DETAIL VIEW OF B

| SR NO | TUBE SPECIFICATION | |
|---|---|---|
| 1 | 80X80X3.2mm | OUTER FRAME |
| 2 | 40X40X2mm | INNER PATTERN |
| 3 | 80X80X3.2mm | FOR MS POST |

TOTAL NO OF POST ARE 5.

| CLEAR WIDTH | CLEAR HEIGHT | QUANTITY | LOCATION |
|---|---|---|---|
| 8000mm | 1800mm | 1 NOS | MAIN ENTRANCE TO LPC |
| 8000mm | 1800mm | 1 NOS | MAIN ENTRANCE TO FACTORY |

TOLERANCE- ±10mm

DIMENSION :

| CLEAR WIDTH | CLEAR HEIGHT | QUANTITY |
|---|---|---|
| 8000mm | 1800mm | 2 NOS |

MATERIAL:

THICKNESS :

NOTE-
1. ALL REQUIRED CIVIL WORK WILL BE IN CLIENTS SCOPE.
2. ONE COAT OF RED OXIDE & TWO COAT OF APPROVED RAL SHADE WILL BE GIVEN TO THE GATE.
3.GATE LEAF WILL BE IN TWO PARTS FOR TRANSPORTATION & WILL BE WELD TOGETHER ON SITE.

NIHVA TECHNOLOGIES PVT. LTD.
NIHVA TECHNOLOGIES PVT. LTD. PUNE
Email:- info@nihva.com
Website:- www.nihva.com

TITLE:

# AUTOMATIC SINGLE LEAF SLIDING GATE

CLIENT'S APPROVAL :

CLIENT -

PROJECT -

SITE LOCATION -

DWG. NO. : NIHVA/17-18/VDR/0048

SCALE: NTS | WT: | SHEET:1 OF 1

DRAWN BY: SURAJ | DATE: 20-05-2017

CHECK BY : SAGAR P | DATE: 20-05-2017

APPROVED BY : S.S | DATE: 20-05-2017

If any queries contact : projects@nihva.com

NOTE: ALL DIMENSIONS ARE IN mm

THIS DRAWING & DESIGN IS THE PROPERTY OF NIHVA TECHNOLOGIES. NOT TO BE SOLD OR COPIED TO ANY OTHER CONCERN.