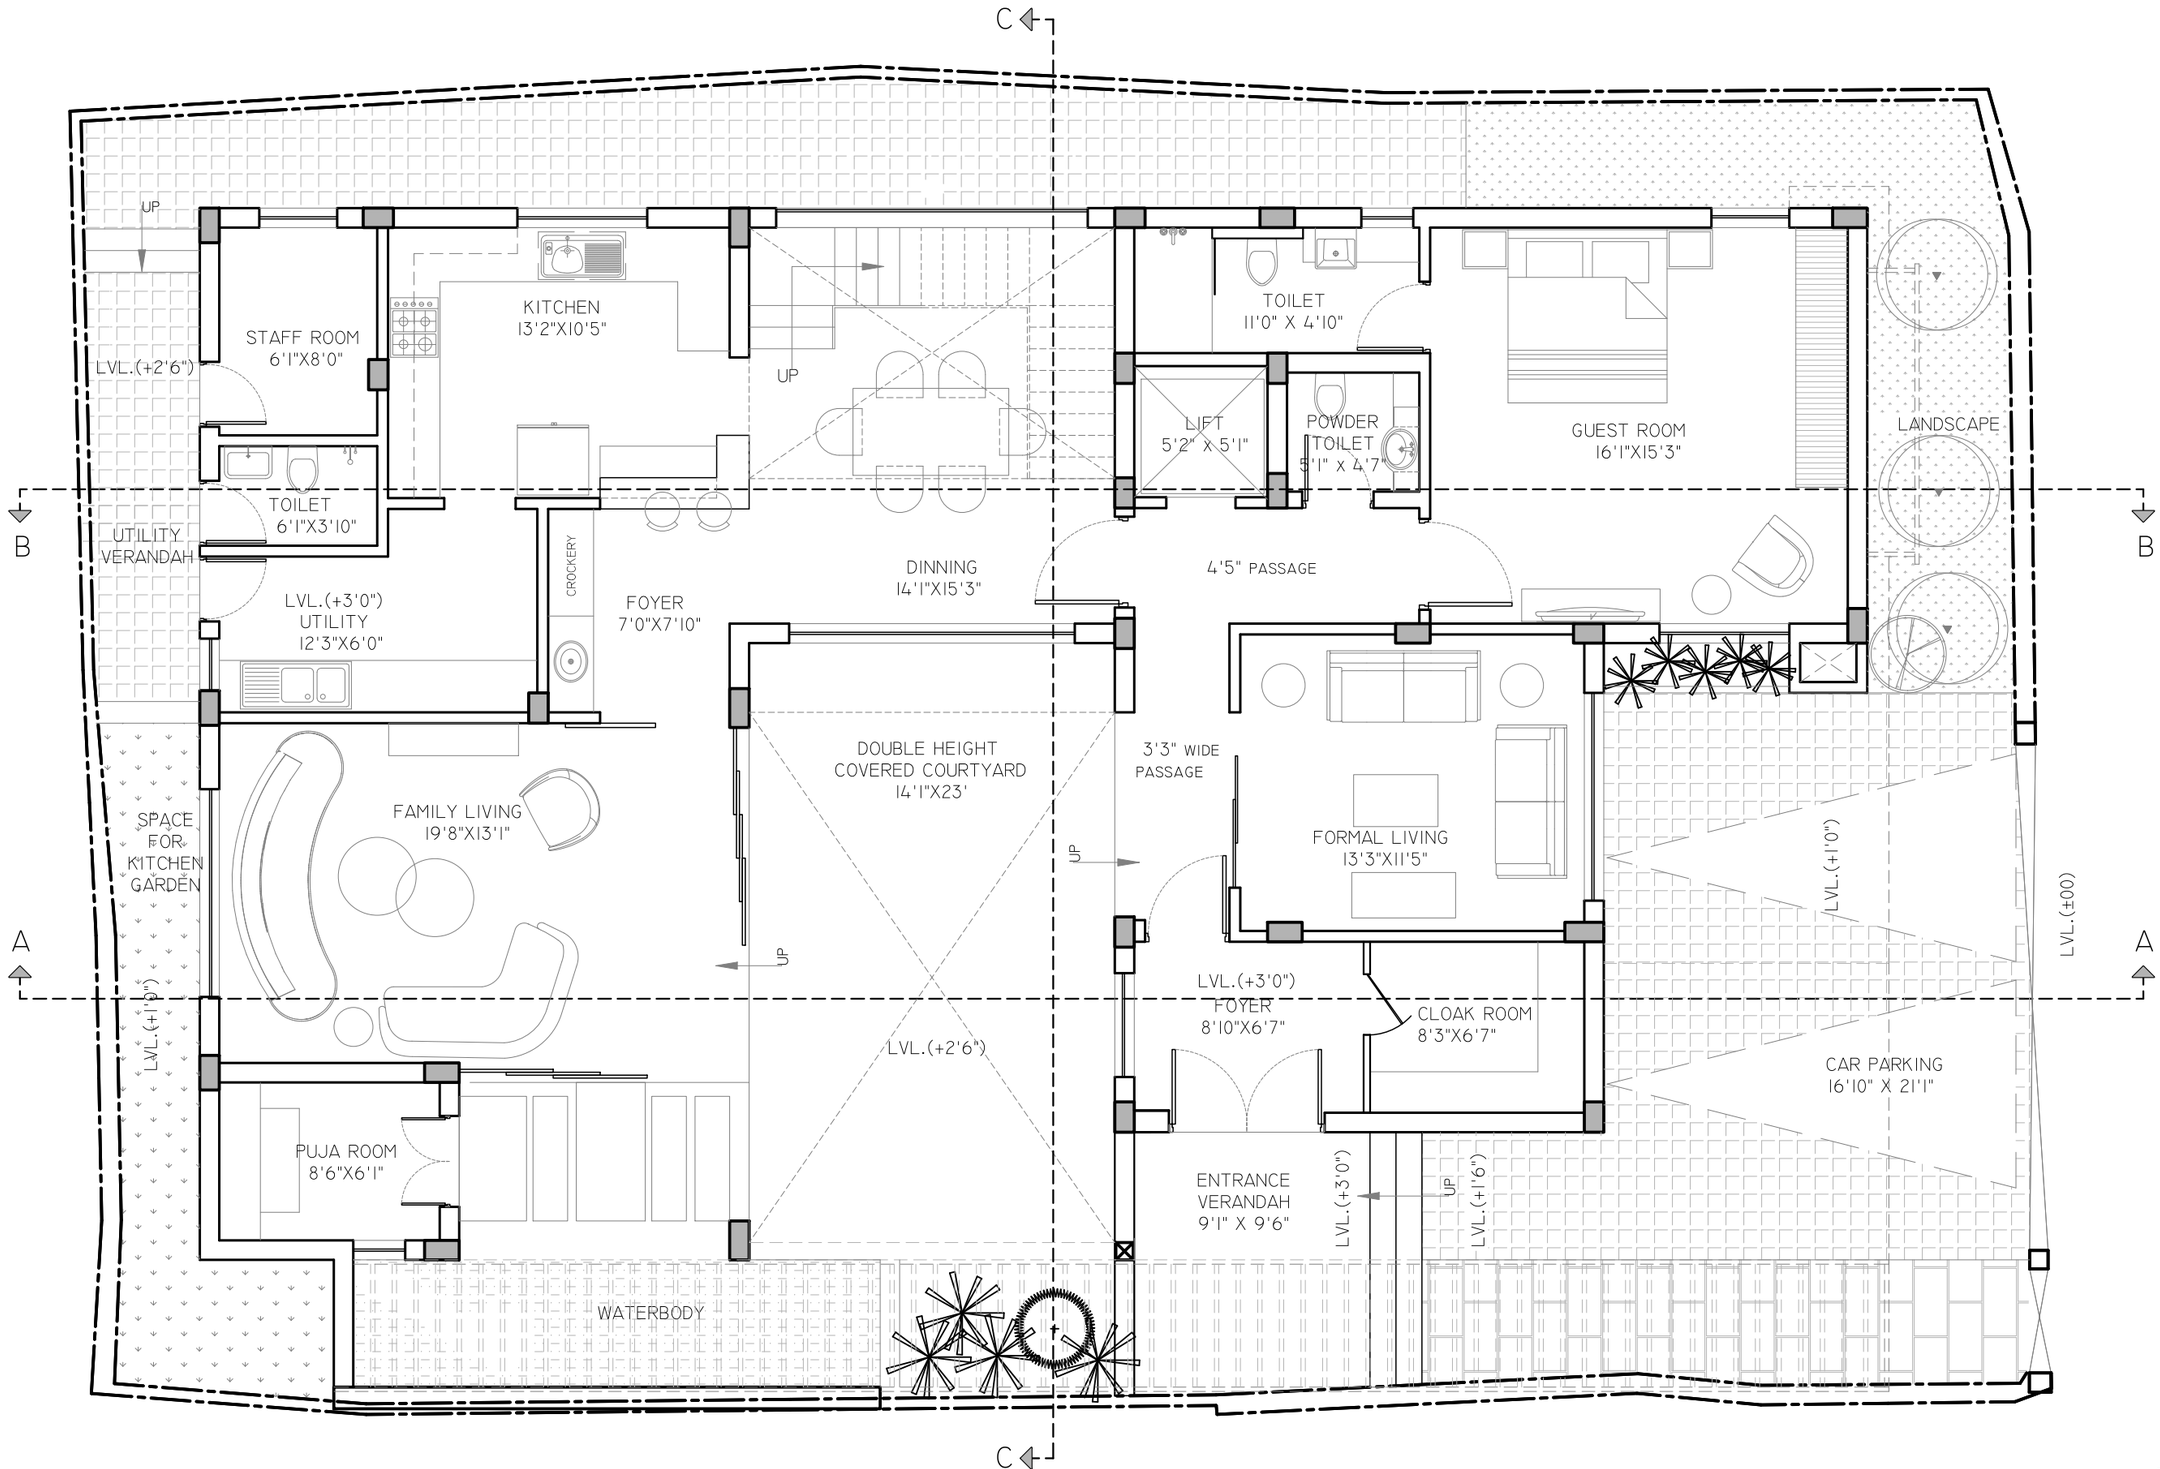


This drawing is an instrument of service and shall remain the property of I.D.E.A.Z. This drawing and the concepts contained herein shall not be used, reproduced, revised or retained without written approval of I.D.E.A.Z.. This drawing should not be scaled, written dimensions are indicative and must be confirmed at site.

ideaz
architectural consultants
8th floor OCHC complex near ram mandir
janpath bhubaneswar orissa 751 001
ph: +91 674 6538010 fax: +91 674 2391710
email : admin@ideaz.co.in web : www.ideaz.co.in

WORKING DRAWING - ARCHITECTURE

PROJECT

Proposed Residence at DD 11

Civil Township, RKL

REVISIONS

SCALE	DATE
1"=6'-0"	15 JAN 2024
DEALT BY	CHECKED BY
SJ	SJ

DRAWING No.
D014/001/001

TITLE

Ground Floor Plan