


ITEM NO.	PART NUMBER	DESCRIPTION	QTY.
1	TRACK GNT_007	GNT_007	2
2	PANEL _022	GNT_006	2
3	NYLON WHEEL _01	STD PART	4
4	kriti nagar Track locking plate	TRACK LOCKING PLATE	4
5	PANEL _021_01	GNT_006	1
6	INTERMEDIAT SUPPORT WELDING PLATE ASSEMBALLY	INTERMEDIAT SUPPORT WELDING PLATE	8
7	PANEL _00021	GNT_006	1

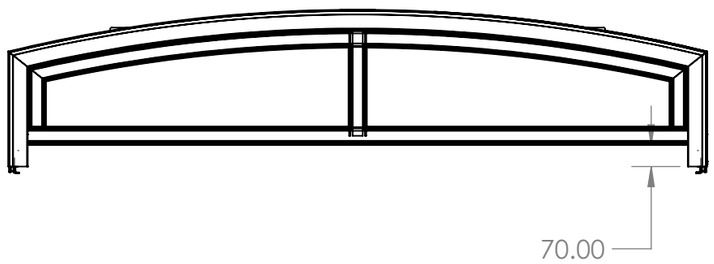


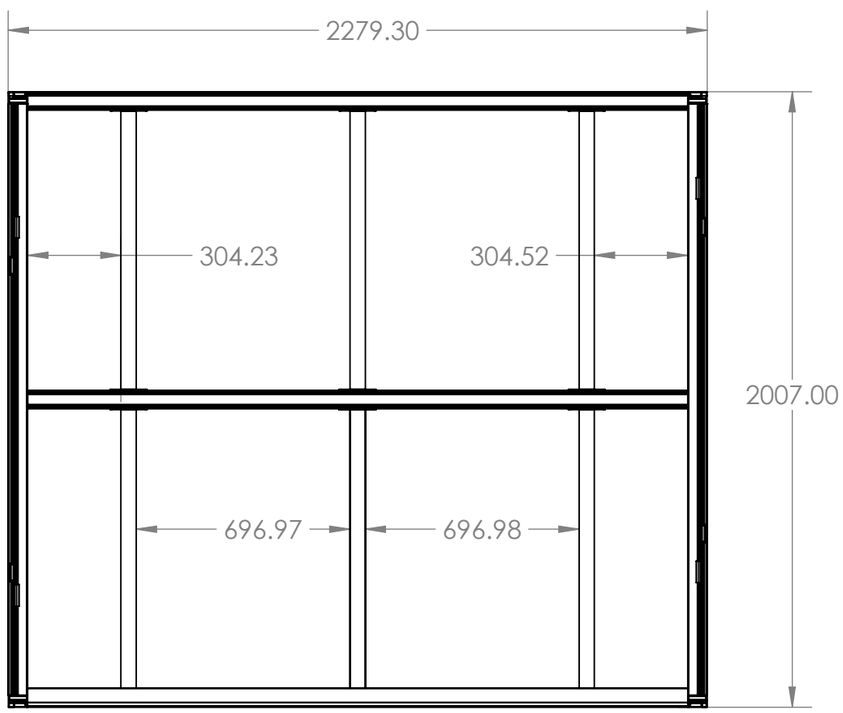

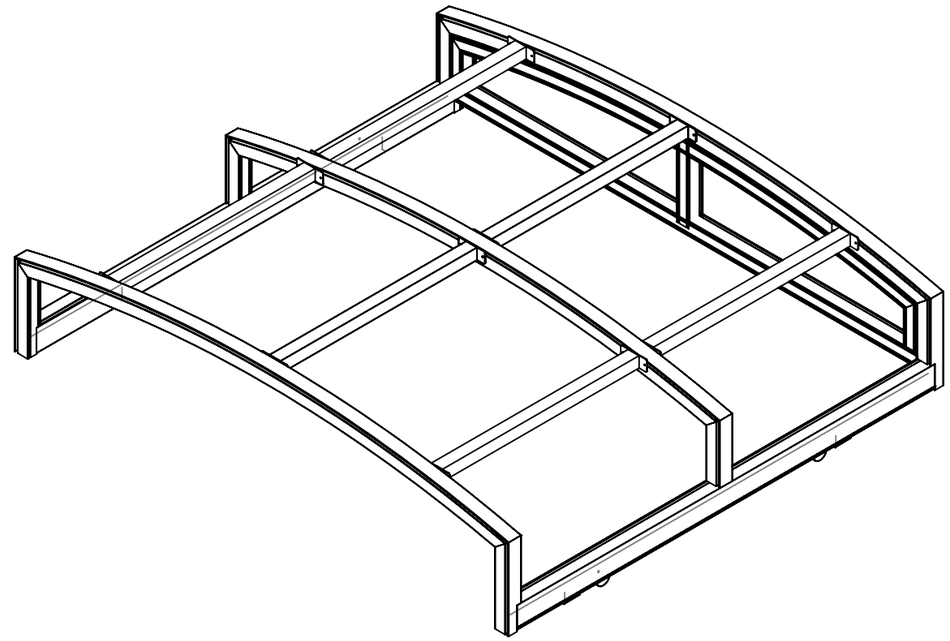


TITLE - PROFILE FOR FRAME_02				NIHVA TECHNOLOGIES PVT.LTD.PUNE Website - www.nihva.com
DWG NO - NTPL-229-FRAME_02			QTY - 1	
	NAME	SIGNATURE	DATE	PROJECT NO - NTPL-229-PM
DRAWN	S.W		28.05.2024	PRODUCT - SLIDING ROOF
CHK'D	P.M.		28.05.2024	SITE LOCATION - KIRTI NAGAR 2
APPV'D	V.T.		28.05.2024	
if any queries contact - supportautomation@nihva.com				REVISION -
ALL DIMENSION ARE IN mm			A3	SCALE - SHEET 1 OF 6

ITEM NO.	PART NUMBER	DESCRIPTION	QTY.
1	PANEL _021Encloser	GNT_006	1

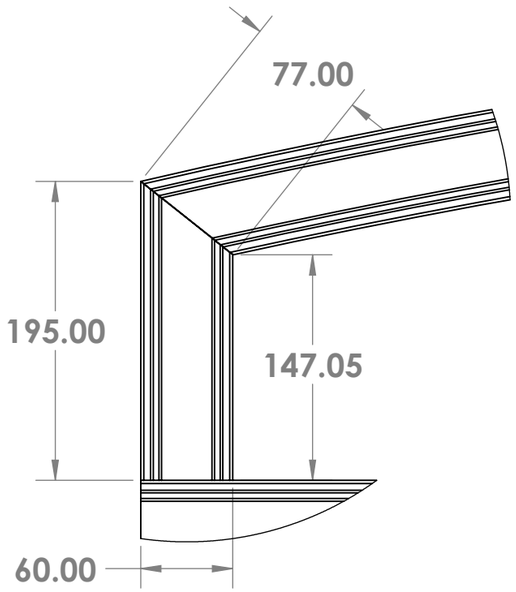



DETAIL A
SCALE 1 : 4

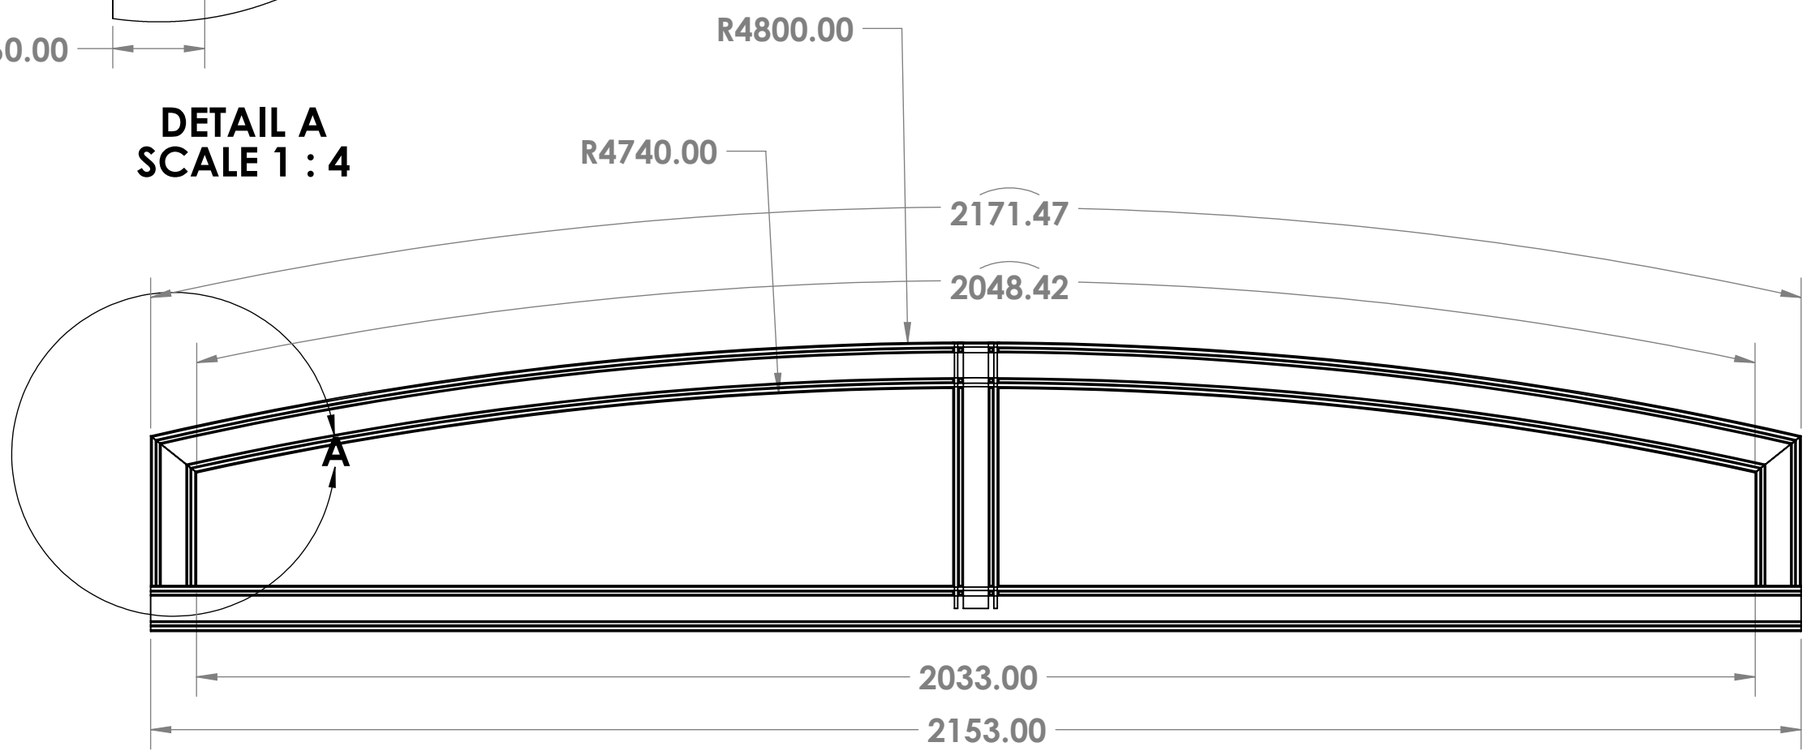

TITLE - SLIDING ROOF				NIHVA TECHNOLOGIES PVT.LTD.PUNE
DWG NO - NTPL-229- Enclosure			QTY - 1	Website - www.nihva.com
	NAME	SIGNATURE	DATE	PROJECT NO - NTPL-229
DRAWN	S.W		28.05.2024	PRODUCT - SLIDING ROOF
CHK'D	P.M.		28.05.2024	SITE LOCATION - KIRTI NAGAR
APPV'D	V.T.		28.05.2024	
if any queries contact - supportautomation@nihva.com				REVISION -
ALL DIMENSION ARE IN mm			A3	SCALE - SHEET 2 OF 6


ITEM NO.	PART NUMBER	DESCRIPTION	QTY.
1	TRACK GNT_007	GNT_007	2

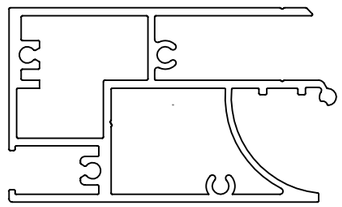

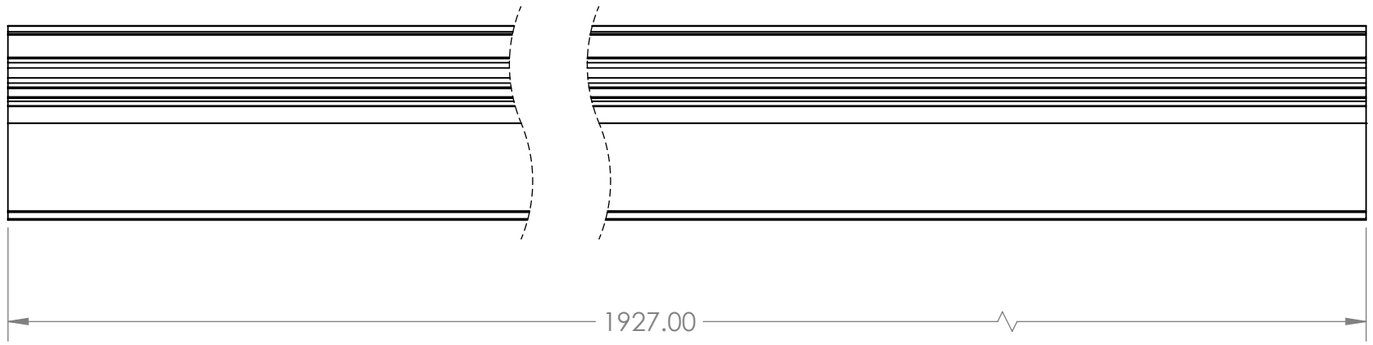


TITLE - SLIDING ROOF				NIHVA TECHNOLOGIES PVT.LTD.PUNE Website - www.nihva.com
DWG NO - NTPL-229-FRAME_02			QTY - 1	
	NAME	SIGNATURE	DATE	PROJECT NO - NTPL-229-PM
DRAWN	S.W		28.05.2024	PRODUCT - SLIDING ROOF
CHK'D	P.M.		28.05.2024	SITE LOCATION - KIRTI NAGAR
APPV'D	V.T.		28.05.2024	
if any queries contact - supportautomation@nihva.com				REVISION -
ALL DIMENSION ARE IN mm			A3	SCALE - SHEET 3 OF 6


ITEM NO.	PART NUMBER	DESCRIPTION	QTY.
1	PANEL _022	GNT_006	2

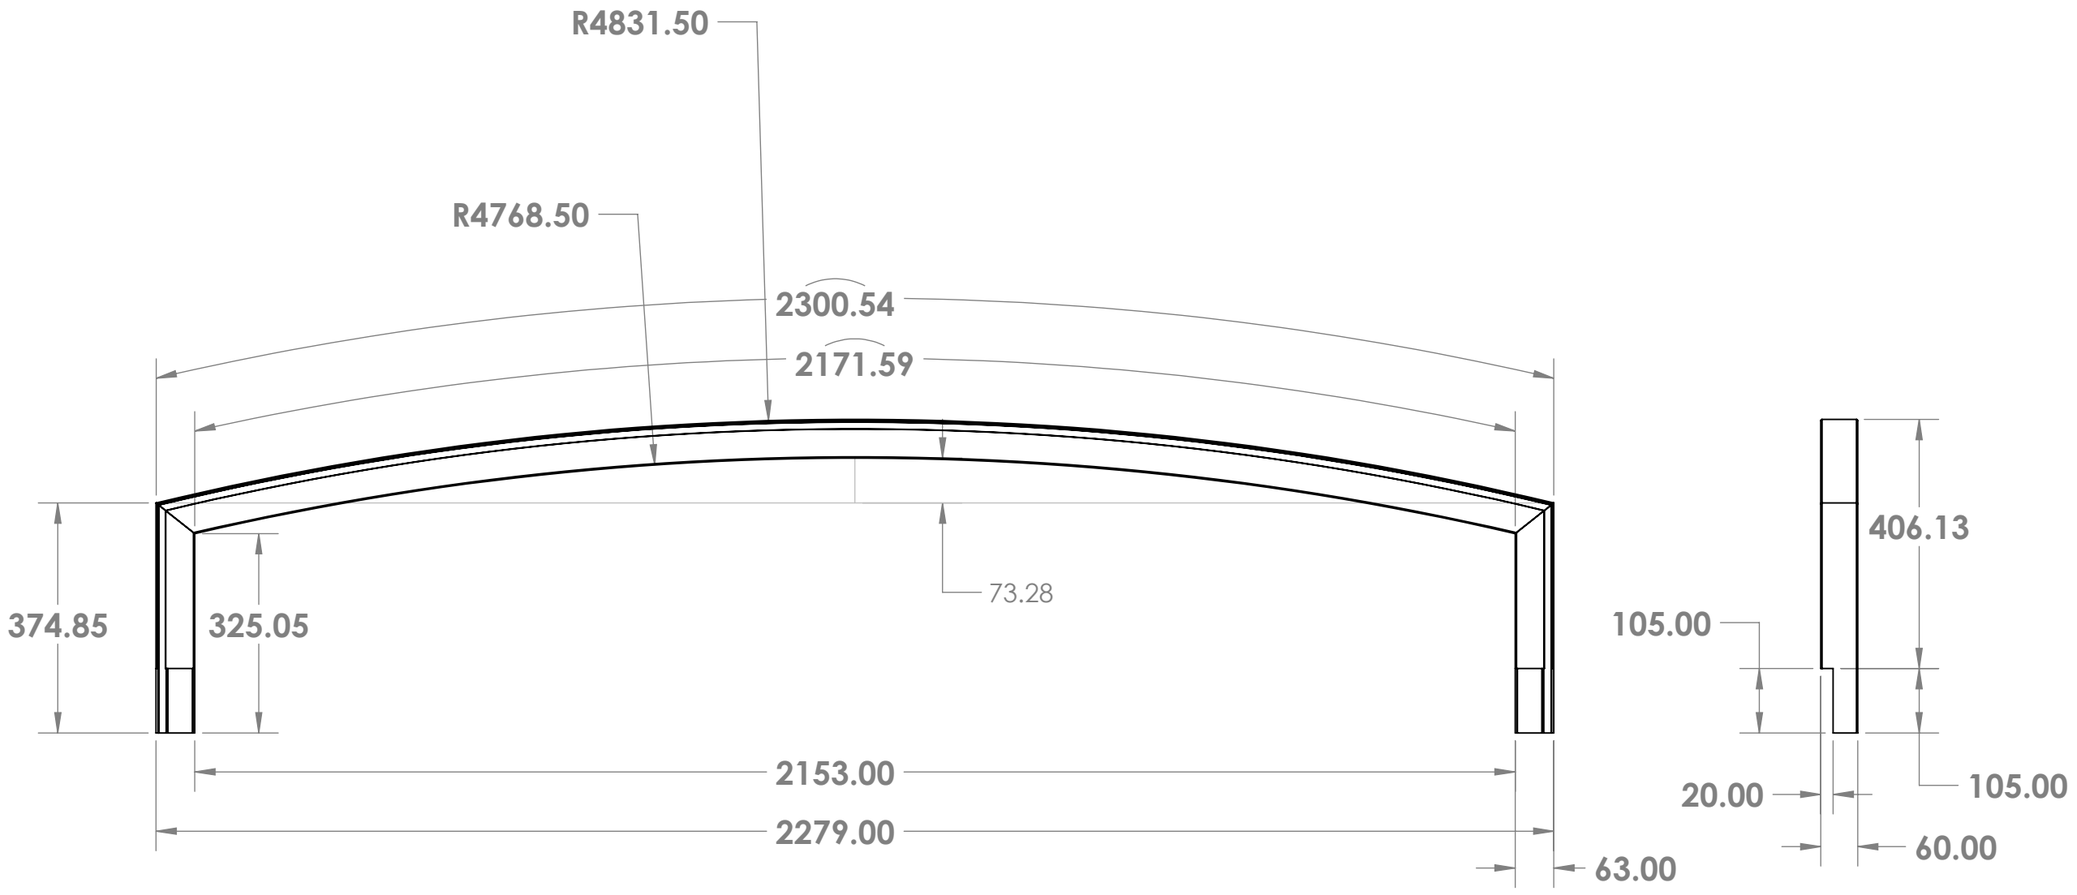

TITLE - SLIDING ROOF				NIHVA TECHNOLOGIES PVT.LTD.PUNE Website - www.nihva.com
DWG NO - NTPL-229-FRAME_02			QTY - 1	
	NAME	SIGNATURE	DATE	PROJECT NO - NTPL229-PM
DRAWN	S.W		28.05.2024	PRODUCT - SLIDING ROOF
CHK'D	P.M.		28.05.2024	SITE LOCATION - KIRTI NAGAR
APPV'D	V.T.		28.05.2024	
if any queries contact - supportautomation@nihva.com				REVISION -
ALL DIMENSION ARE IN mm			A3	SCALE - SHEET 4 OF 6


ITEM NO.	PART NUMBER	DESCRIPTION	QTY.
1	kriti nagar Track locking plate	TRACK LOCKING PLATE	4

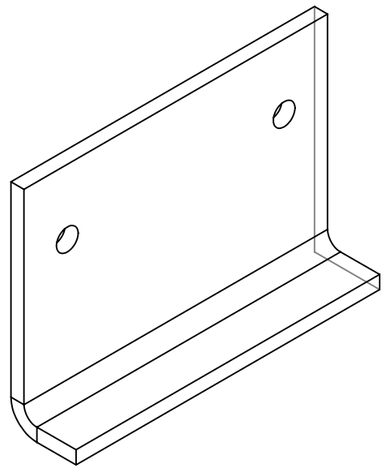

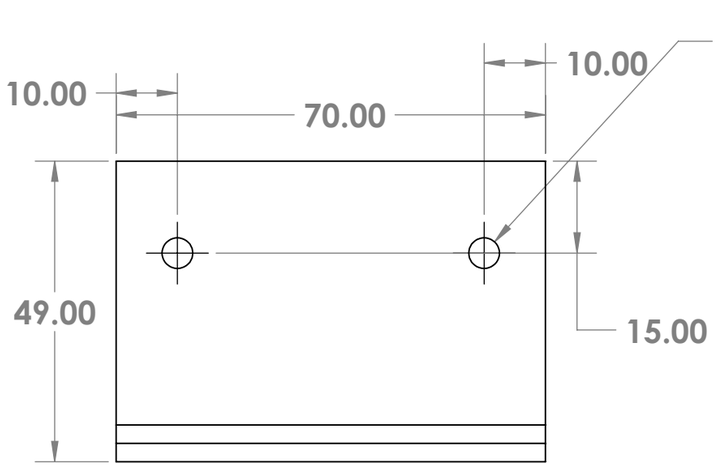

TITLE - SLIDING ROOF				NIHVA TECHNOLOGIES PVT.LTD.PUNE
DWG NO - NTPL-229-FRAME_02			QTY - 1	Website - www.nihva.com
	NAME	SIGNATURE	DATE	PROJECT NO - NTPL-229
DRAWN	S.W		28.05.2024	PRODUCT - SLIDING ROOF
CHK'D	P.M.		28.05.2024	SITE LOCATION - KIRTI NAGAR
APPV'D	V.T.		28.05.2024	
if any queries contact - supportautomation@nihva.com				REVISION -
ALL DIMENSION ARE IN mm			A3	SCALE - SHEET 5 OF 6

ITEM NO.	PART NUMBER	DESCRIPTION	QTY.
1	PANEL _021_01	GNT_006	1

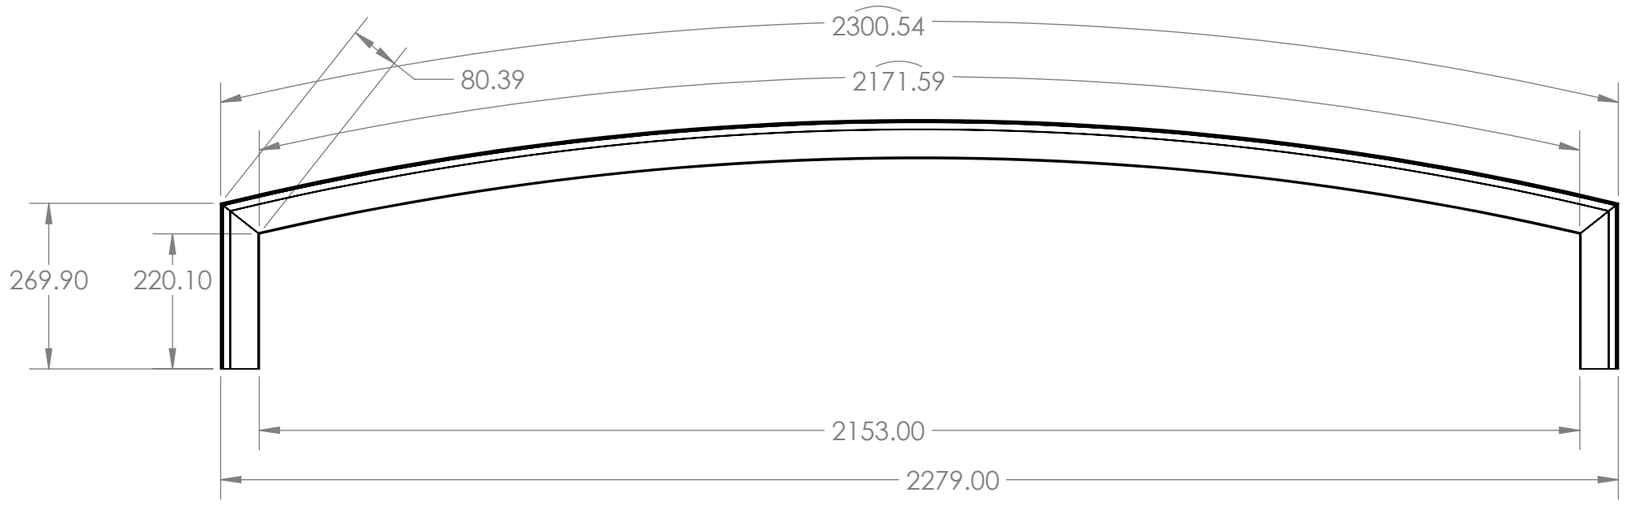

TITLE - PROFILE FOR PANEL NO-1				NIHVA TECHNOLOGIES PVT.LTD.PUNE Website - www.nihva.com
DWG NO - NTPL221-PROF01			QTY - 1	
	NAME	SIGNATURE	DATE	PROJECT NO - NTPL221
DRAWN	D.V.		20.03.2024	PRODUCT - BALCONY ENCLOSURE
CHK'D	P.M.		20.03.2024	SITE LOCATION -
APPV'D	V.T.		20.03.2024	
if any queries contact - supportautomation@nihva.com				REVISION -
ALL DIMENSION ARE IN mm		A3		SCALE - SHEET 6 OF 6